Quadro de Cargas (QD1)

Circuito	Descrição	Esquema	Método de inst.	V (V)	Iluminação (W) 150	Pot. total. (VA)	Pot. total. (W)	Fases	Pot. - R (W)	Pot. - S (W)	Pot. - T (W)	FCT	FCA	In' (A)	Seção (mm2)	Ic (A)	Disj (A)	dV parc (%)	dV total (%)	Status
1	Iluminação 01	F+N+T	B1	220 V	15	2296	2250	R	2250			1.00	0.80	13.0	10	57.0	13.0	2.31	3.14	Ok
2	Iluminação 02	F+N+T	B1	220 V	17	2602	2550	S		2550		1.00	0.80	14.8	10	57.0	13.0	2.70	3.52	Ok
TOTAL					32	4898	4800	R+S	2250	2550	0									

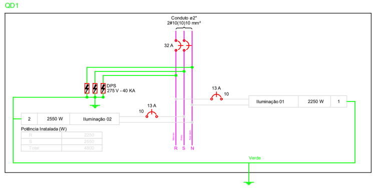

Legenda

⊠	Caixa de passagem de embutir no piso
▭	Entrada de serviço aérea - Saída aérea
◎ 1 150 LED	Luminária 150W
▮	Quadro de distribuição - embutir a 1,50m do piso

Lista de Materiais

Elétrica	**Acessórios uso geral**	
	Fita isolante autofusão 20m	1 pç
	Cabo Unipolar (cobre)	
	Isol.PVC - 450/750V (ref. Pirelli Ecoplus BWF Flexível) 10 mm²	1397.85 m
	Isol.PVC - 450/750V (ref. Pirelli Ecoplus BWF Flexível) 2.5 mm²	1057.05 m
	Caixa de passagem - solo	
	Alvenaria ou prémoldada 400x400x400 mm	17 pç
	Aterramento	
	Haste de aterramento 2400mm x 3/4"	17 pç
	Grampo p/ haste de aterramento Reforçado	17 pç
	Dispositivo de Proteção	
	Disjuntor Unipolar Termomagnético - norma DIN 13 A	2 pç
	Disjuntor bipolar termomagnético (380 V/220 V) - DIN 32 A - 4.5 kA	1 pç
	Dispositivo de proteção contra surto 275 V - 40 KA	3 pç
	Eletroduto PVC flexível	
	Eletroduto leve 3/4"	346.10 m
	Eletroduto pesado 2"	685.90 m
	Lâmpada LED	
	Luminária LED Iluminação Pública Luminária 150W	32 pç
	Poste Ornamental Iluminação Pública	
	Poste aço galvanizado com 1 braço de 3 metros Poste 10m	8 pç
	Poste aço galvanizado com 2 braços de 3 metros Poste 10m	12 pç
	Material p/ entrada serviço	
	Padrão de energia bifásico	1 pç
	Ramal de Entrada Fases, Neutro e Terra	10 mm²
	Haste de aterramento aço/cobre D=3/4", comprimento 2,4 m	1 pç
	Caixa inspeção aterramento 250x250x400 mm	1 pç
	Caixa CMI-02	1 pç
	Poste de Concreto duplo T 100 daN, L=7,0m	1 pç
	Quadro distrib. chapa pintada - embutir	
	Bifásico Cap. 12 disj. unip.	1 pç

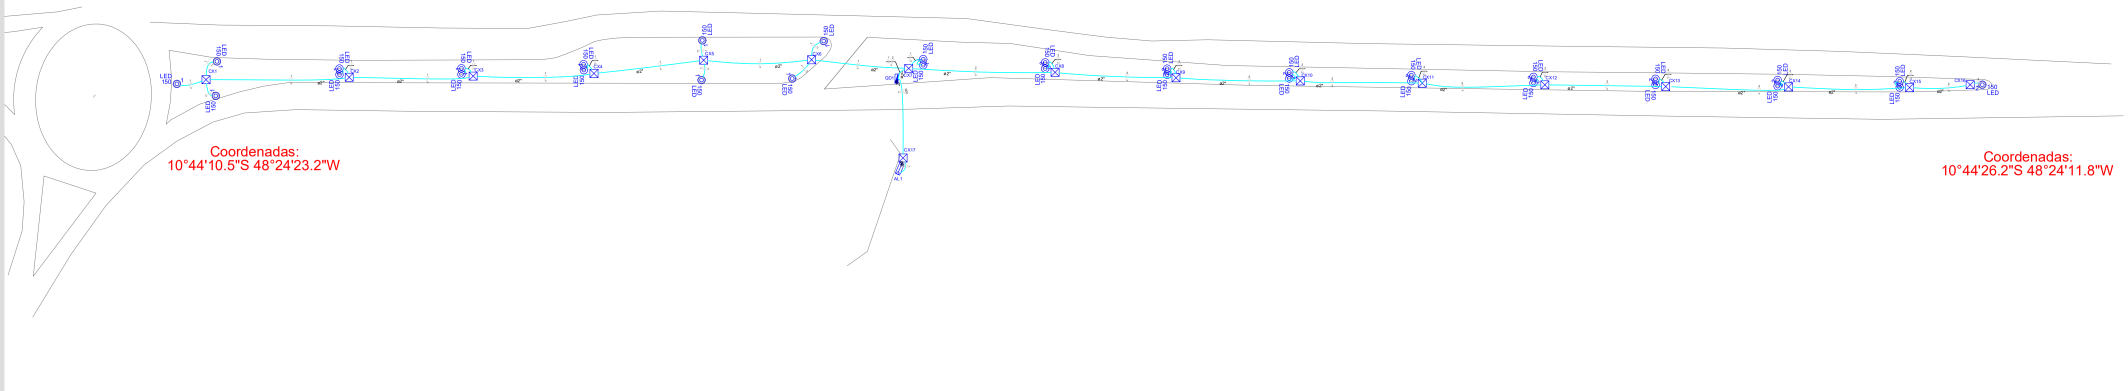

BREVE DESCRITIVO DO EMPREENDIMENTO

Projeto elétrico iluminação pública do Anel Viáriol de Porto Nacional - TO

OBSERVAÇÃO

Sem observações.

DADOS DO PROJETO:

Endereço: Anel Viário
Cidade / Setor: Porto Nacional -TO
Proprietário: Prefeitura Municipal de Porto Nacional - TO
Autor do Projeto: Rodrigo Neres Lompa
Resp. Técnico: Rodrigo Neres Lompa
Coordenadas Geográficas: Fuso: 22L
X: Latitude 783967 Y: Longitude 8811580

Prefeitura Municipal de Porto Nacional - TO
Proprietário:

Rodrigo Neres Lompa
Autor do Projeto
RODRIGO NERES LOMPA:03398659110 Assinado de forma digital por RODRIGO NERES LOMPA:03398659110
2418403335
Nº Crea:

Rodrigo Neres Lompa
Resp. Técnico:
2418403335
Nº Crea:

PROJETO ELETRICO

Nº DESENHO

PROJETO ELÉTRICO ILUMINAÇÃO PÚBLICA ANEL VIÁRIO.

1/8

Projetista: Rodrigo Neres Lompa
Data Completa: 14/01/2026
Escala: DIVERSAS

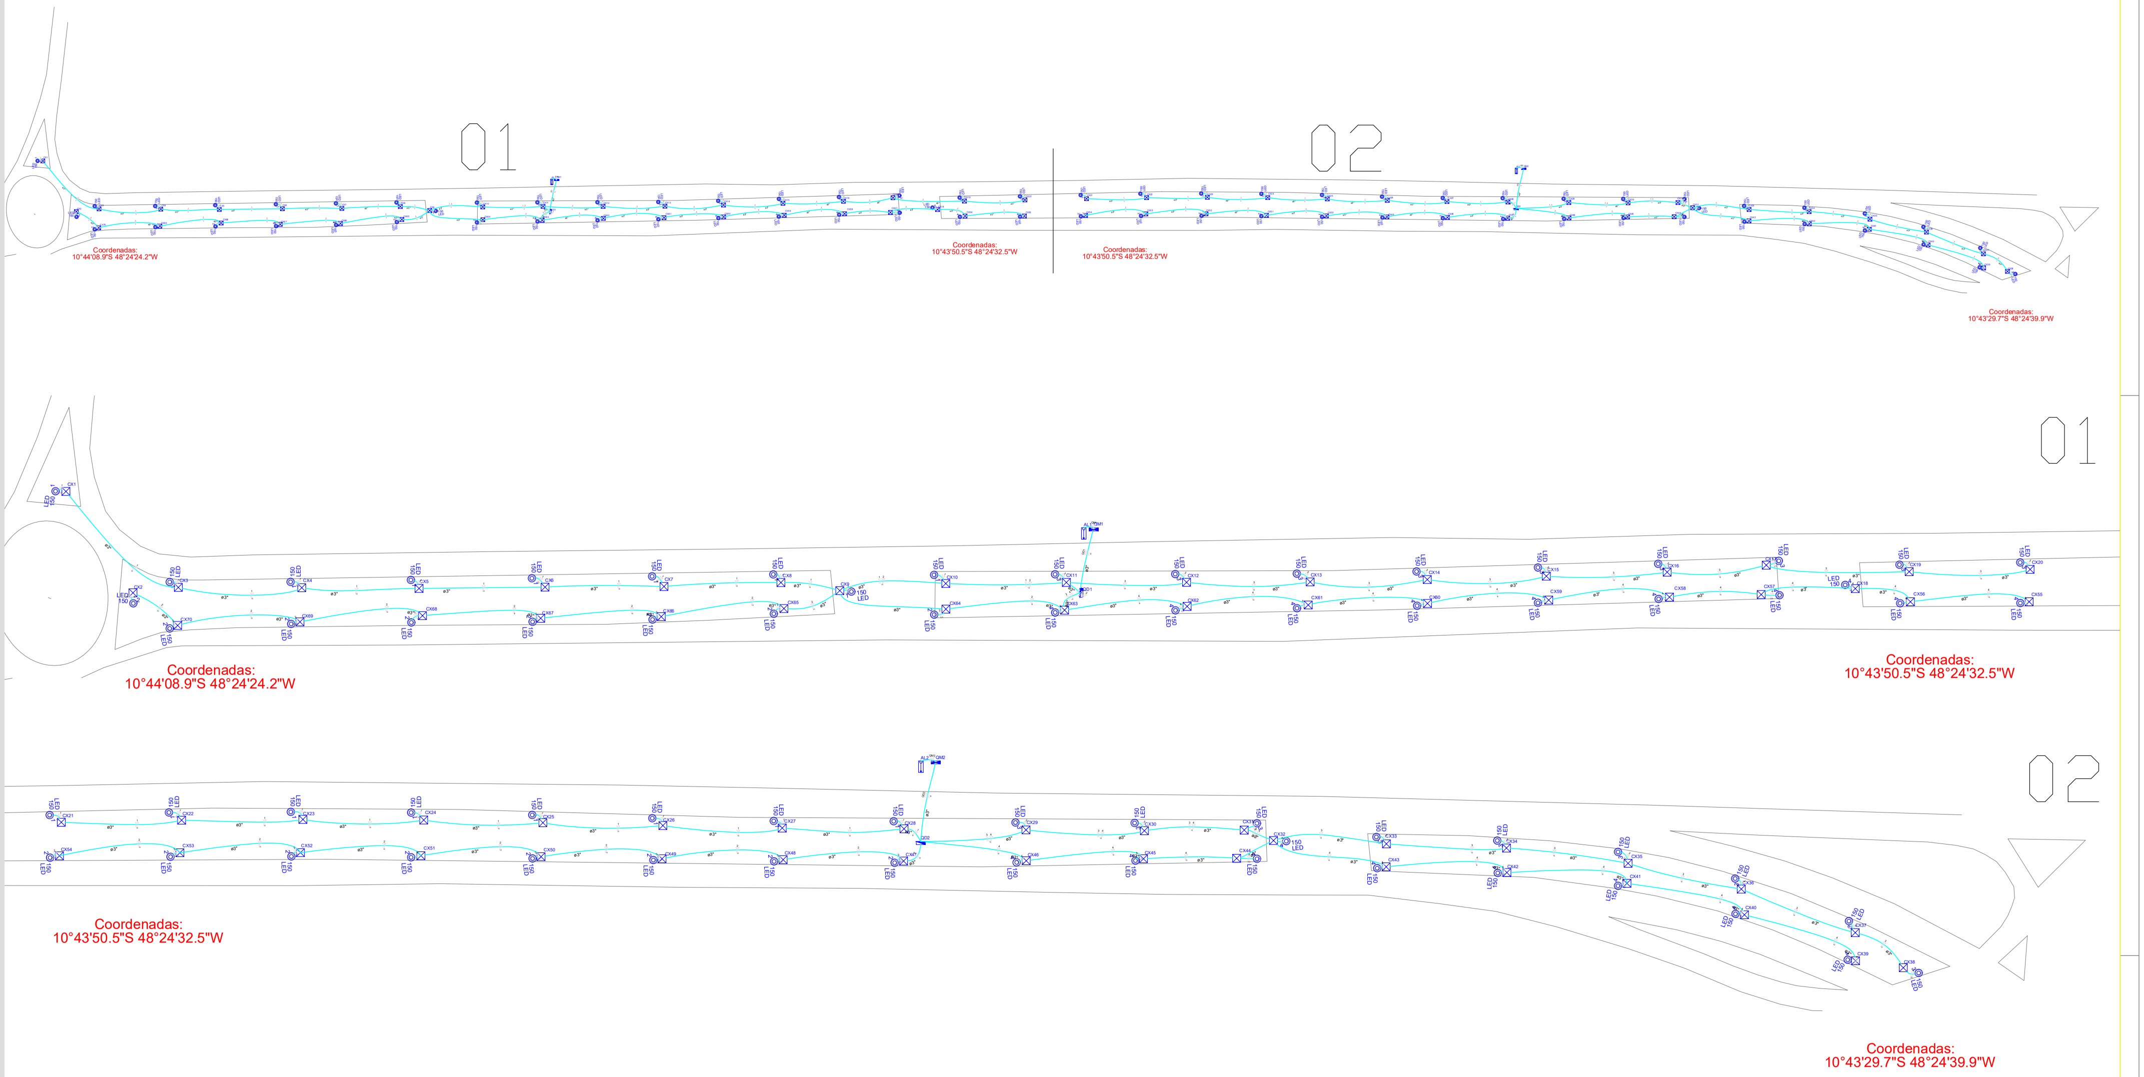
01
02
Coordenadas:
10°44'08.9"S 48°24'24.2"W
Coordenadas:
10°43'50.5"S 48°24'32.5"W
Coordenadas:
10°43'29.7"S 48°24'39.9"W
LED
150
ø3"
QD1
QD2

Quadro de Cargas (QD1)

Circuito	Descrição	Esquema	Método de inst.	V (V)	Iluminação (W) 150	Pot. total. (VA)	Pot. total. (W)	Fases	Pot. - R (W)	Pot. - S (W)	Pot. - T (W)	FCT	FCA	In' (A)	Seção (mm2)	Ic (A)	Disj (A)	dV parc (%)	dV total (%)	Status
1	ILUMINAÇÃO 1	F+N+T	D	220 V	9	1378	1350	R	1350			1.00	0.70	8.9	10	63.0	10.0	2.11	2.88	Ok
2	ILUMINAÇÃO 2	F+N+T	D	220 V	8	1224	1200	R	1200			1.00	0.70	7.0	10	63.0	10.0	1.92	2.69	Ok
3	ILUMINAÇÃO 3	F+N+T	D	220 V	9	1378	1350	S		1350		1.00	0.70	8.9	10	63.0	10.0	1.87	2.64	Ok
4	ILUMINAÇÃO 4	F+N+T	D	220 V	10	1531	1500	S		1500		1.00	0.80	8.7	10	63.0	10.0	2.23	3.00	Ok
TOTAL					36	5510	5400	R+S	2550	2850	0									

Quadro de Cargas (QD2)

Circuito	Descrição	Esquema	Método de inst.	V (V)	Iluminação (W) 150	Pot. total. (VA)	Pot. total. (W)	Fases	Pot. - R (W)	Pot. - S (W)	Pot. - T (W)	FCT	FCA	In' (A)	Seção (mm2)	Ic (A)	Disj (A)	dV parc (%)	dV total (%)	Status
1	ILUMINAÇÃO 5	F+N+T	D	220 V	8	1224	1200	R	1200			1.00	1.00	5.6	10	63.0	10.0	1.48	2.37	Ok
2	ILUMINAÇÃO 6	F+N+T	D	220 V	8	1224	1200	R	1200			1.00	1.00	5.6	10	63.0	10.0	1.50	2.39	Ok
3	ILUMINAÇÃO 7	F+N+T	D	220 V	9	1378	1350	S		1350		1.00	0.80	7.8	10	63.0	10.0	2.17	3.06	Ok
4	ILUMINAÇÃO 8	F+N+T	D	220 V	9	1378	1350	S		1350		1.00	0.80	5.2	10	63.0	10.0	1.64	2.52	Ok
TOTAL					34	5204	5100	R+S	2400	2700	0									

QD1

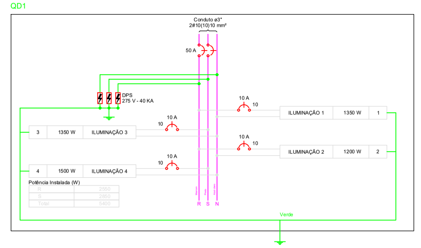

QD2

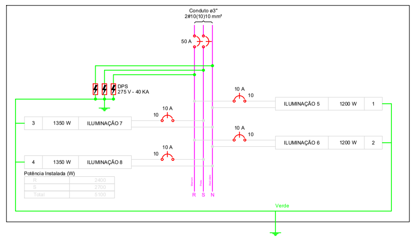

Legenda

⧗	Caixa de medição embutir a 1,60m do piso
☒	Caixa de passagem de embutir no piso
⊸	Entrada de serviço aérea - Saída aérea
1 ◎ 150 LED	Luminária 150W
◪	Quadro de distribuição - embutir a 1,50m do piso

Lista de Materiais

Elétrica

Item	Quantidade
Acessórios uso geral	
Fita isolante autofusão 20m	2 pç
Cabo Unipolar (cobre)	
Isol.PVC - 450/750V (ref. Pirelli Ecoplus BWF Flexível) 10 mm²	5904.94 m
Isol.PVC - 450/750V (ref. Pirelli Ecoplus BWF Flexível) 2,5 mm²	3175.26 m
Caixa de passagem - solo	
Alvenaria ou prémoldada 400x400x400 mm	70 pç
Aterramento	
Haste de aterramento 2400mm x 3/4"	70 pç
Grampo p/ haste de aterramento Reforçado	70 pç
Dispositivo de Proteção	
Disjuntor Unipolar Termomagnético - norma DIN 10 A	8 pç
50 A	2 pç
Dispositivo de proteção contra surto 275 V - 40 KA	6 pç
Dispositivo de Comando	
Contator Tripolar 12 A	2 pç
Relé fotoelétrico 4 pinos 1000 W	2 pç
Base p/ Relé fotoelétrico 4 pinos	2 pç
Eletroduto PVC flexível	
Eletroduto leve 3/4"	1023.90 m
Eletroduto pesado 3"	2855.70 m
Lâmpada LED	
Luminária LED Iluminação Pública Luminária 150W	70 pç
Poste Ornamental Iluminação Pública	
Poste aço galvanizado com braço 3 metros Poste 10m	70 pç
Material p/ entrada serviço	
Padrão de energia bifásico	2 pç
Ramal de Entrada Fases, Neutro e Terra	10 mm²
Haste de aterramento aço/cobre D=3/4", comprimento 2,4 m	1 pç
Caixa inspeção aterramento 250x250x400 mm	1 pç
Caixa CMI-02	1 pç
Poste de Concreto duplo T 100 daN, L=7,0m	1 pç
Quadro distrib. chapa pintada - embutir	
Bifásico Cap. 24 disj. unip.	2 pç

BREVE DESCRITIVO DO EMPREENDIMENTO

Projeto elétrico iluminação pública do Anel Viáriol de Porto Nacional - TO

OBSERVAÇÃO

Sem observações.

DADOS DO PROJETO:

Endereço: Anel Viário
Cidade / Setor: Porto Nacional -TO
Proprietário: Prefeitura Municipal de Porto Nacional - TO
Autor do Projeto: Rodrigo Neres Lompa
Resp. Técnico: Rodrigo Neres Lompa
Coordenadas Geográficas: Fuso: 22L
X: Latitude 783414
Y: Longitude 8812637

Prefeitura Municipal de Porto Nacional - TO
Proprietário:

Rodrigo Neres Lompa
Autor do Projeto
RODRIGO NERES LOMPA:03398659110
Assinado de forma digital por RODRIGO NERES LOMPA:03398659110
2418403335
Nº Crea:

Rodrigo Neres Lompa
Resp. Técnico:
2418403335
Nº Crea:

PROJETO ELETRICO

Nº DESENHO

PROJETO ELÉTRICO ILUMINAÇÃO PÚBLICA ANEL VIÁRIO.

2/8

Projetista: Rodrigo Neres Lompa
Data Completa: 25/07/2025
Escala: DIVERSAS

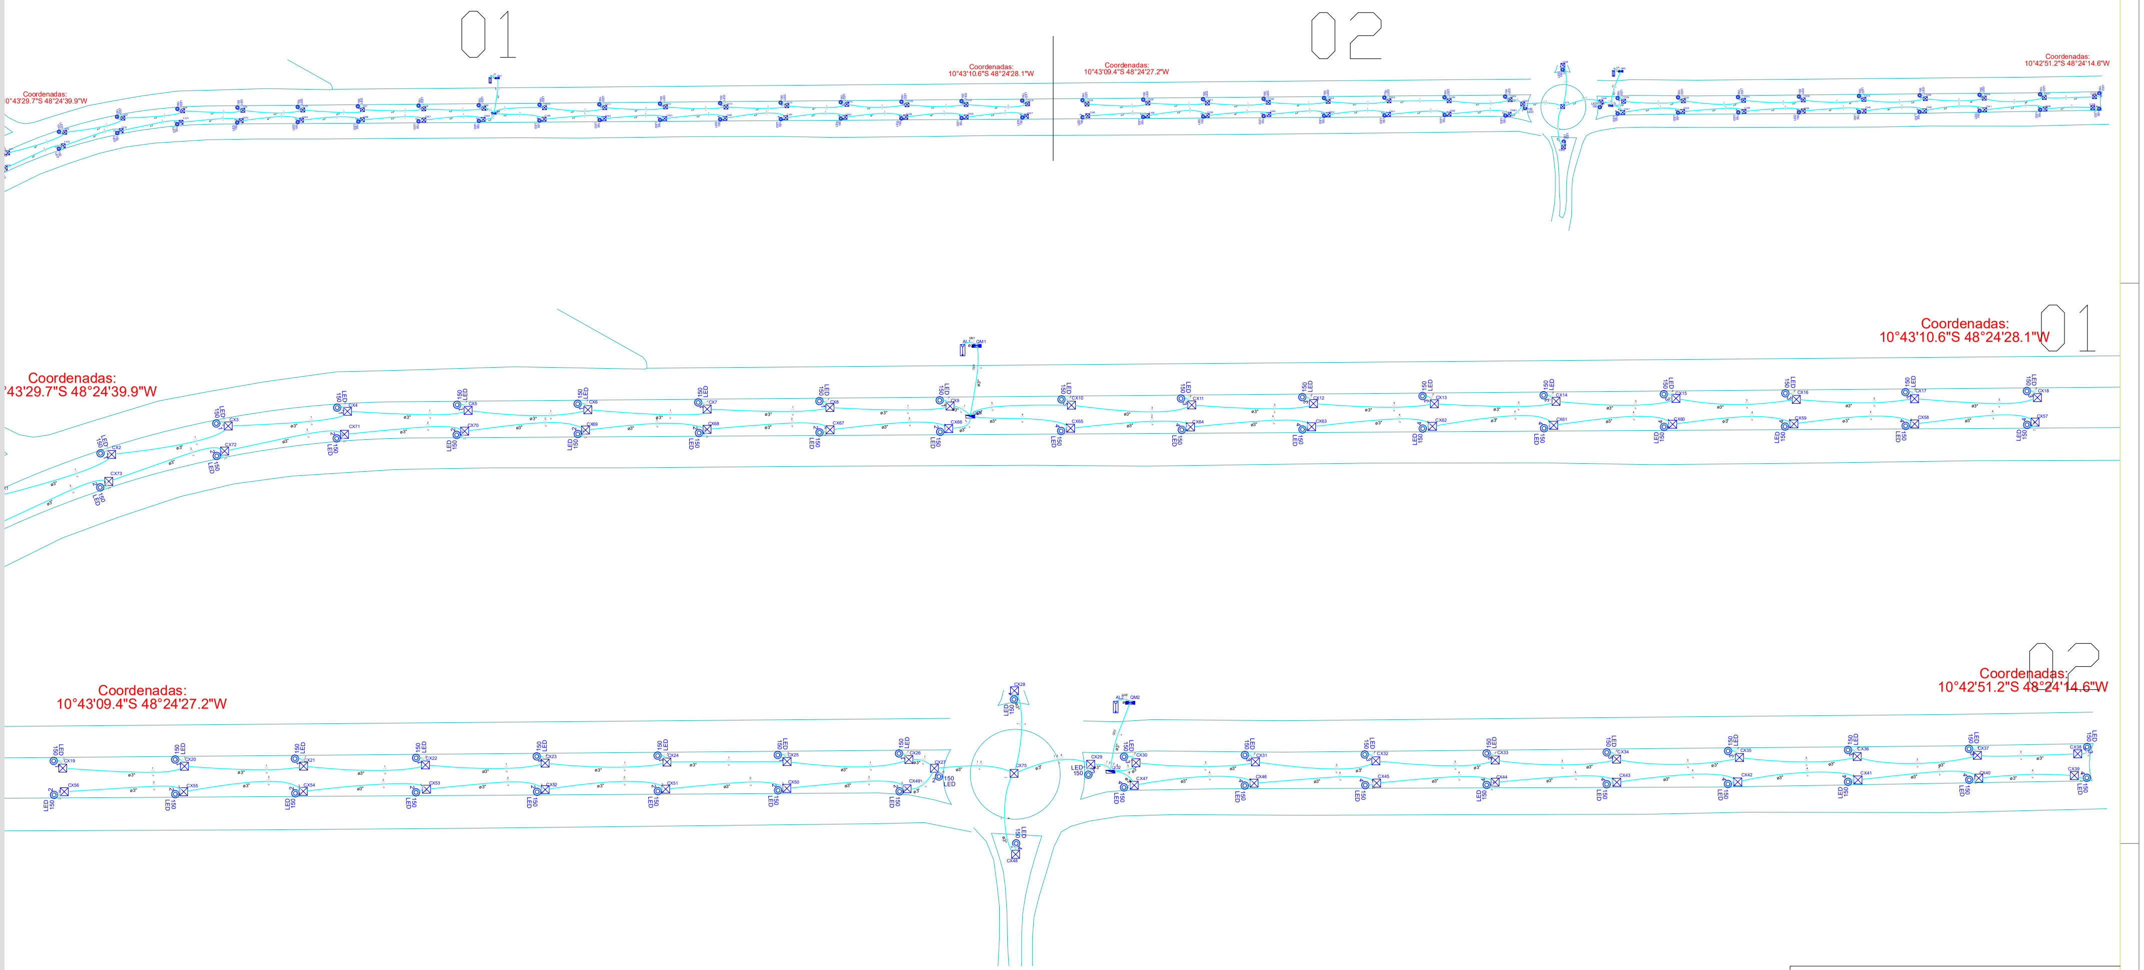
01
02
Coordenadas: 10°43'29.7"S 48°24'39.9"W
Coordenadas: 10°43'10.6"S 48°24'28.1"W
Coordenadas: 10°43'09.4"S 48°24'27.2"W
Coordenadas: 10°42'51.2"S 48°24'14.6"W
150 LED
ø3"

Quadro de Cargas (QD1)

uito	Descrição	Esquema	Método de inst.	V (V)	Iluminação (W) 150	Pot. total. (VA)	Pot. total. (W)	Fases	Pot. - R (W)	Pot. - S (W)	Pot. - T (W)	FCT	FCA	In' (A)	Seção (mm2)	Ic (A)	Disj (A)	dV parc (%)	dV total (%)	Status
	ILUMINAÇÃO 01	F+N+T	D	220 V	9	1378	1350	R	1350			1.00	1.00	6.3	10	63.0	10.0	1.90	2.69	Ok
	ILUMINAÇÃO 02	F+N+T	D	220 V	9	1378	1350	R	1350			1.00	1.00	6.3	10	63.0	10.0	1.91	2.71	Ok
	ILUMINAÇÃO 03	F+N+T	D	220 V	9	1378	1350	S		1350		1.00	1.00	6.3	10	63.0	10.0	2.19	2.99	Ok
	ILUMINAÇÃO 04	F+N+T	D	220 V	9	1378	1350	S		1350		1.00	1.00	6.3	10	63.0	10.0	2.19	2.98	Ok
AL					36	5510	5400	R+S	2700	2700	0									

QD1

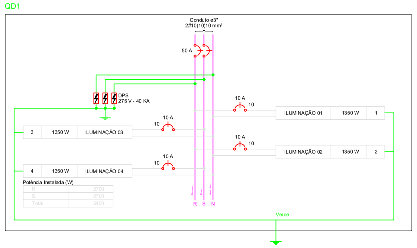

Quadro de Cargas (QD2)

Circuito	Descrição	Esquema	Método de inst.	V (V)	Iluminação (W) 150	Pot. total. (VA)	Pot. total. (W)	Fases	Pot. - R (W)	Pot. - S (W)	Pot. - T (W)	FCT	FCA	In' (A)	Seção (mm2)	Ic (A)	Disj (A)	dV parc (%)	dV total (%)	Status
1	ILUMINAÇÃO 05	F+N+T	D	220 V	9	1378	1350	R	1350			1.00	0.65	9.6	10	63.0	10.0	2.14	3.03	Ok
2	ILUMINAÇÃO 06	F+N+T	D	220 V	9	1378	1350	R	1350			1.00	0.65	9.6	10	63.0	10.0	2.19	3.08	Ok
3	ILUMINAÇÃO 07	F+N+T	D	220 V	10	1531	1500	S		1500		1.00	0.65	6.3	10	63.0	10.0	1.90	2.79	Ok
4	ILUMINAÇÃO 08	F+N+T	D	220 V	10	1531	1500	S		1500		1.00	0.65	6.3	10	63.0	10.0	1.91	2.80	Ok
TOTAL					38	5816	5700	R+S	2700	3000	0									

QD2

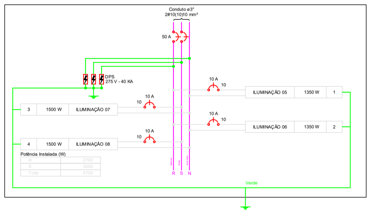

Legenda

⧗	Caixa de medição embutir a 1,60m do piso
☒	Caixa de passagem de embutir no piso
⊸	Entrada de serviço aérea - Saída aérea
◎ 150 LED	Luminária 150W
◢	Quadro de distribuição - embutir a 1,50m do piso

Lista de Materiais

Elétrica		
Acessórios uso geral		
	Fita isolante autofusão 20m	2 pç
Cabo Unipolar (cobre)		
	Isol.PVC - 450/750V (ref. Pirelli Ecoplus BWF Flexível) 10 mm²	6260.00 m
	Isol.PVC - 450/750V (ref. Pirelli Ecoplus BWF Flexível) 2,5 mm²	3161.83 m
Caixa de passagem - solo		
	Alvenaria ou prémoldada 400x400x400 mm	74 pç
Aterramento		
	Haste de aterramento 2400mm x 3/4"	74 pç
	Grampo p/ haste de aterramento Reforçado	74 pç
Dispositivo de Proteção		
	Disjuntor Unipolar Termomagnético - norma DIN 10 A	8 pç
	50 A	2 pç
	Dispositivo de proteção contra surto 275 V - 40 KA	6 pç
Dispositivo de Comando		
	Contator Tripolar 12 A	2 pç
	Relé fotoelétrico 4 pinos 1000 W	2 pç
	Base p/ Relé fotoelétrico 4 pinos	2 pç
Eletroduto PVC flexível		
	Eletroduto leve 3/4"	1028.60 m
	Eletroduto pesado 3"	3054.30 m
Lâmpada LED		
	Luminária LED Iluminação Pública Luminária 150W	74 pç
Poste Ornamental Iluminação Pública		
	Poste aço galvanizado com braço 3 metros Poste 10m	74 pç
Material p/ entrada serviço		
	Padrão de energia bifásico	2 pç
	Ramal de Entrada Fases, Neutro e Terra	10 mm²
	Haste de aterramento aço/cobre D=3/4", comprimento 2,4 m	1 pç
	Caixa inspeção aterramento 250x250x400 mm	1 pç
	Caixa CMI-02	1 pç
	Poste de Concreto duplo T 100 daN, L=7,0m	1 pç
Quadro distrib. chapa pintada - embutir		
	Bifásico Cap. 20 disj. unip.	2 pç

BREVE DESCRITIVO DO EMPREENDIMENTO

Projeto elétrico iluminação pública do Anel Viário de Porto Nacional - TO

OBSERVAÇÃO

Sem observações.

DADOS DO PROJETO:

Endereço: Anel Viário
Cidade / Setor: Porto Nacional -TO
Proprietário: Prefeitura Municipal de Porto Nacional - TO
Autor do Projeto: Rodrigo Neres Lompa
Resp. Técnico: Rodrigo Neres Lompa
Coordenadas Geográficas: Fuso: 22L
X: Latitude 783533
Y: Longitude 8813789

Prefeitura Municipal de Porto Nacional - TO
Proprietário:

RODRIGO NERES LOMPA:03398659110 Assinado de forma digital por RODRIGO NERES LOMPA:03398659110

Rodrigo Neres Lompa
Autor do Projeto
2418403335
Nº Crea:

Rodrigo Neres Lompa
Resp. Técnico:
2418403335
Nº Crea:

PROJETO ELETRICO

Nº DESENHO

PROJETO ELÉTRICO ILUMINAÇÃO PÚBLICA ANEL VIÁRIO.

3/8

Projetista: Rodrigo Neres Lompa
Data Completa: 14/01/2026
Escala: DIVERSAS

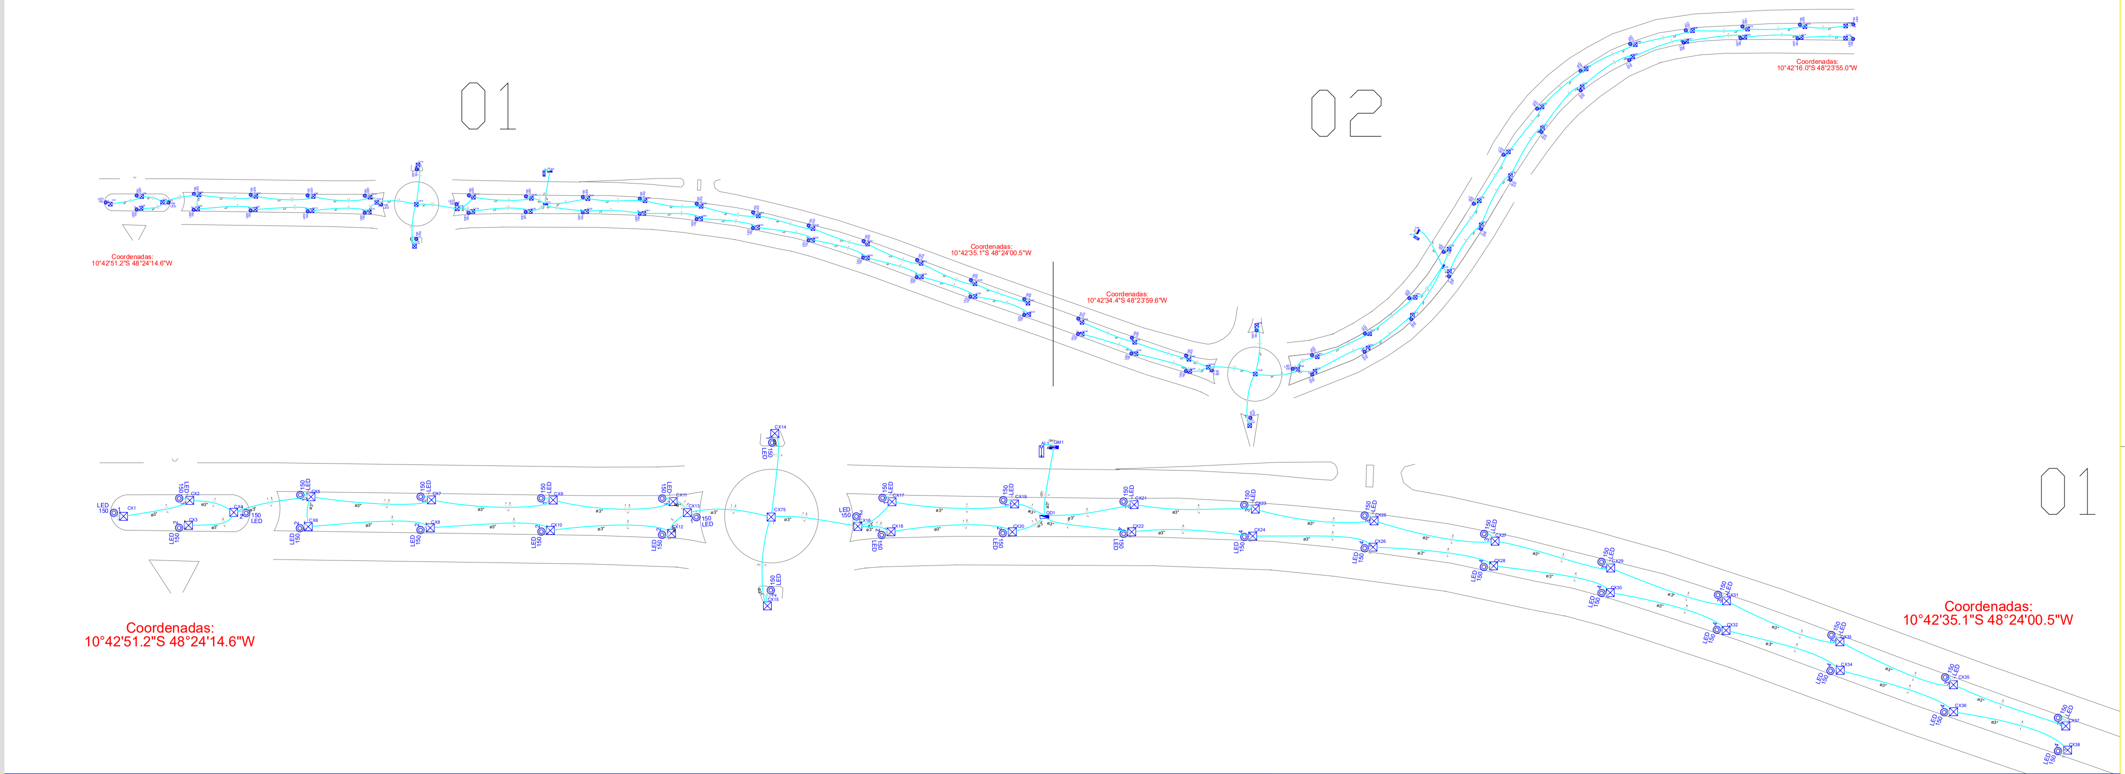
01
02
Coordenadas:
10°42'16.0"S 48°23'55.0"W
Coordenadas:
10°42'51.2"S 48°24'14.6"W
Coordenadas:
10°42'35.1"S 48°24'00.5"W
Coordenadas:
10°42'34.4"S 48°23'59.6"W
Coordenadas:
10°42'51.2"S 48°24'14.6"W
Coordenadas:
10°42'35.1"S 48°24'00.5"W
150 LED
CX1
CX75
QD1
ø3"

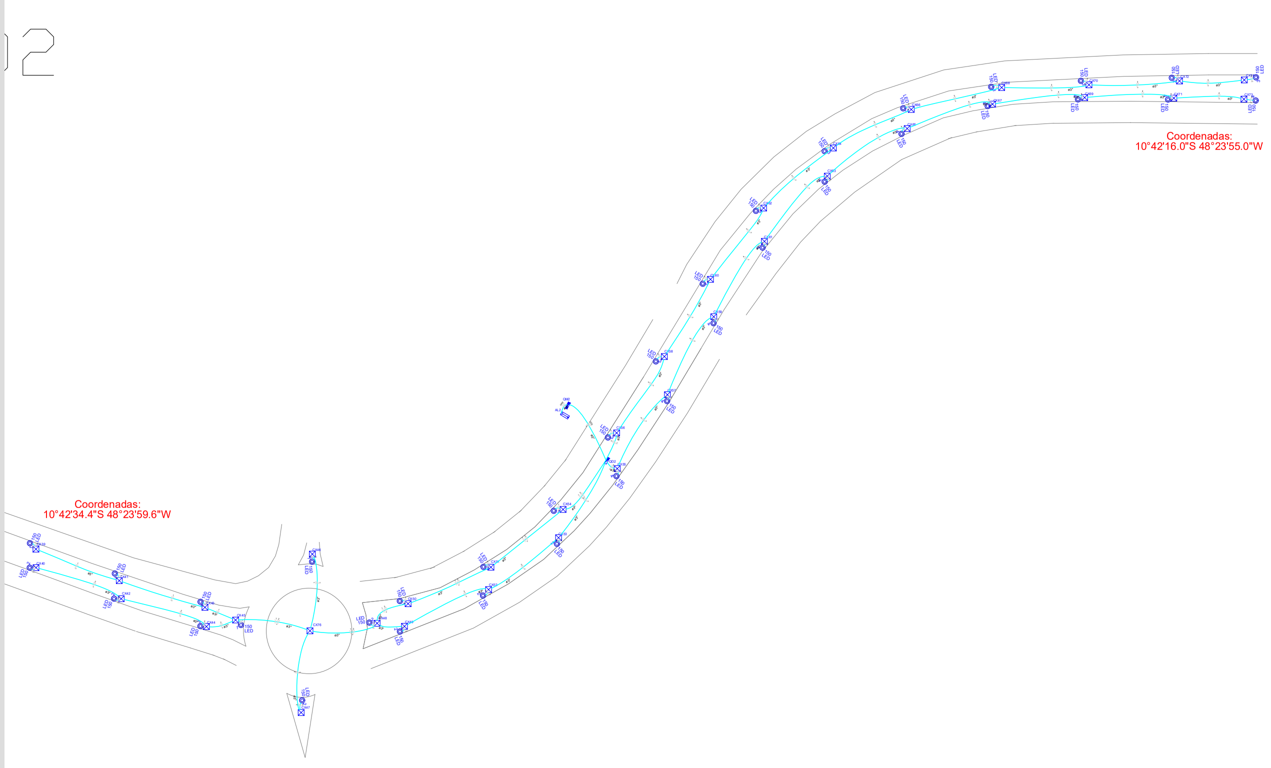

Quadro de Cargas (QD1)

Circuito	Descrição	Esquema	Método de inst.	V (V)	Iluminação (W) 150	Pot. total. (VA)	Pot. total. (W)	Fases	Pot. - R (W)	Pot. - S (W)	Pot. - T (W)	FCT	FCA	In' (A)	Seção (mm2)	Ic (A)	Disj (A)	dV parc (%)	dV total (%)	Status
1	ILUMINAÇÃO 01	F+N+T	B1	220 V	10	1531	1500	R	1500			1.00	0.80	7.0	10	57.0	10.0	1.96	2.88	Ok
2	ILUMINAÇÃO 02	F+N+T	D	220 V	10	1531	1500	R	1500			1.00	0.80	8.7	10	63.0	10.0	1.59	2.51	Ok
3	ILUMINAÇÃO 03	F+N+T	D	220 V	9	1378	1350	S		1350		1.00	1.00	6.3	10	63.0	10.0	2.15	3.07	Ok
4	ILUMINAÇÃO 04	F+N+T	D	220 V	9	1378	1350	S		1350		1.00	1.00	6.3	10	63.0	10.0	2.15	3.07	Ok
TOTAL					38	5816	5700	R+S	3000	2700	0									

QD1

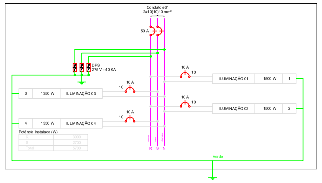

Lista de Materiais

Elétrica	
Acessórios uso geral	
Fita isolante autofusão 20m	2 pç
Cabo Unipolar (cobre)	
Isol.PVC - 450/750V (ref. Pirelli Ecoplus BWF Flexível) 10 mm²	6371.00 m
Isol.PVC - 450/750V (ref. Pirelli Ecoplus BWF Flexível) 2,5 mm²	3337.24 m
Caixa de passagem - solo	
Alvenaria ou prémoldada 400x400x400 mm	74 pç
Aterramento	
Haste de aterramento 2400mm x 3/4"	74 pç
Grampo p/ haste de aterramento Reforçado	74 pç
Dispositivo de Proteção	
Disjuntor Unipolar Termomagnético - norma DIN 10 A	8 pç
50 A	2 pç
Dispositivo de proteção contra surto 275 V - 40 KA	6 pç
Dispositivo de Comando	
Contator Tripolar 12 A	2 pç
Relé fotoelétrico 4 pinos 1000 W	2 pç
Base p/ Relé fotoelétrico 4 pinos	2 pç
Eletroduto PVC flexível	
Eletroduto leve 3/4"	1027.00 m
Eletroduto pesado 3"	2940.80 m
Lâmpada LED	
Luminária LED Iluminação Pública Luminária 150W	74 pç
Poste Ornamental Iluminação Pública	
Poste aço galvanizado com braço 3 metros Poste 10m	74 pç
Material p/ entrada serviço	
Padrão de energia bifásico	2 pç
Ramal de Entrada Fases, Neutro e Terra	10 mm²
Haste de aterramento aço/cobre D=3/4", comprimento 2,4 m	1 pç
Caixa inspeção aterramento 250x250x400 mm	1 pç
Caixa CMI-02	1 pç
Poste de Concreto duplo T 100 daN, L=7,0m	1 pç
Quadro distrib. chapa pintada - embutir	
Bifásico Cap. 24 disj. unip.	2 pç

Quadro de Cargas (QD2)

Circuito	Descrição	Esquema	Método de inst.	V (V)	Iluminação (W) 150	Pot. total. (VA)	Pot. total. (W)	Fases	Pot. - R (W)	Pot. - S (W)	Pot. - T (W)	FCT	FCA	In' (A)	Seção (mm2)	Ic (A)	Disj (A)	dV parc (%)	dV total (%)	Status
1	ILUMINAÇÃO 05	F+N+T	D	220 V	8	1224	1200	R	1200			1.00	0.80	7.0	10	63.0	10.0	1.63	2.72	Ok
2	ILUMINAÇÃO 06	F+N+T	D	220 V	8	1224	1200	R	1200			1.00	0.80	4.3	10	63.0	10.0	1.28	2.37	Ok
3	ILUMINAÇÃO 07	F+N+T	D	220 V	10	1531	1500	S		1500		1.00	1.00	7.0	10	63.0	10.0	2.41	3.50	Ok
4	ILUMINAÇÃO 08	F+N+T	D	220 V	10	1531	1500	S		1500		1.00	1.00	7.0	10	63.0	10.0	2.34	3.44	Ok
TOTAL					36	5510	5400	R+S	2400	3000	0									

QD2

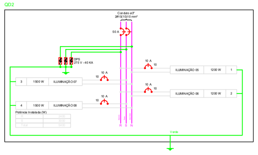

Legenda

⧗	Caixa de medição embutir a 1,60m do piso
☒	Caixa de passagem de embutir no piso
⊸	Entrada de serviço aérea - Saída aérea
◎ 150 LED	Luminária 150W
◤	Quadro de distribuição - embutir a 1,50m do piso

BREVE DESCRITIVO DO EMPREENDIMENTO

Projeto elétrico iluminação pública do Anel Viáriol de Porto Nacional - TO

OBSERVAÇÃO

Sem observações.

DADOS DO PROJETO:

Endereço: Anel Viário
Cidade / Setor: Porto Nacional -TO
Proprietário: Prefeitura Municipal de Porto Nacional - TO
Autor do Projeto: Rodrigo Neres Lompa
Resp. Técnico: Rodrigo Neres Lompa
Coordenadas Geográficas: Fuso: 22L
X: Latitude 784428 Y: Longitude 8814935

Prefeitura Municipal de Porto Nacional - TO
Proprietário:

RODRIGO NERES LOMPA:03398659110
Assinado de forma digital por RODRIGO NERES LOMPA:03398659110

Rodrigo Neres Lompa
Autor do Projeto
2418403335
Nº Crea:

Rodrigo Neres Lompa
Resp. Técnico:
2418403335
Nº Crea:

PROJETO ELETRICO
Nº DESENHO

PROJETO ELÉTRICO ILUMINAÇÃO PÚBLICA ANEL VIÁRIO.
4/8

Projetista:	Data Completa:	Escala:
Rodrigo Neres Lompa	14/01/2026	DIVERSAS

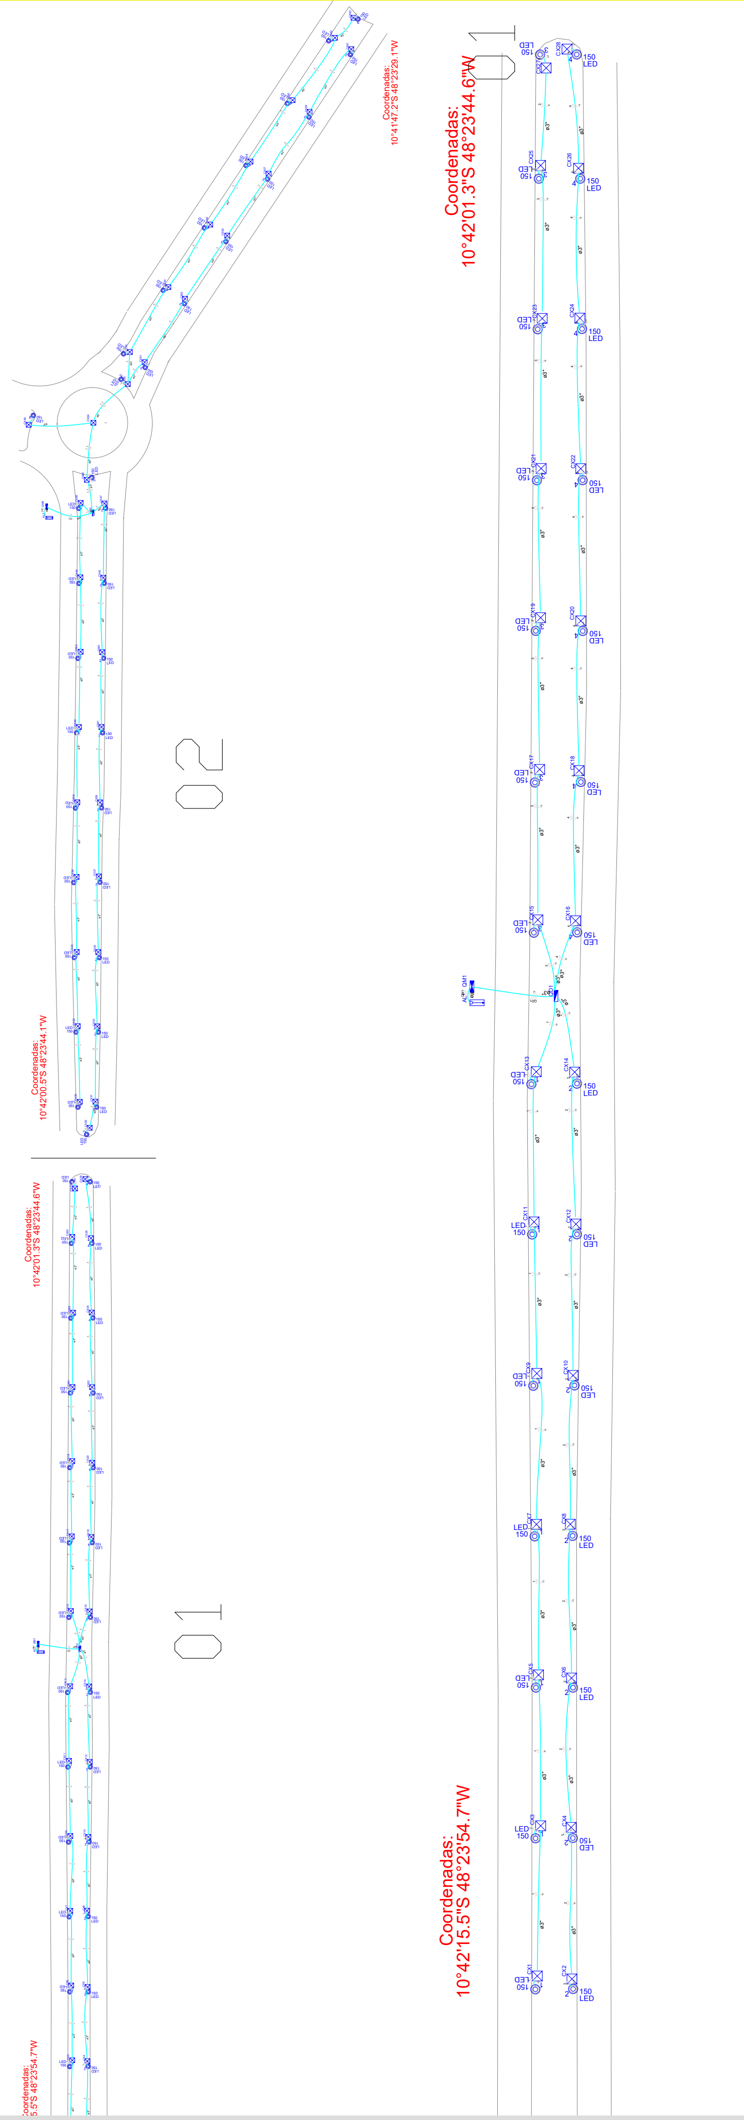
Coordenadas: 10°41'47.2"S 48°23'29.1"W
Coordenadas: 10°42'00.5"S 48°23'44.1"W
Coordenadas: 10°42'01.3"S 48°23'44.6"W
Coordenadas: 10°42'15.5"S 48°23'54.7"W
01
02
150 LED
QM1
ø3"

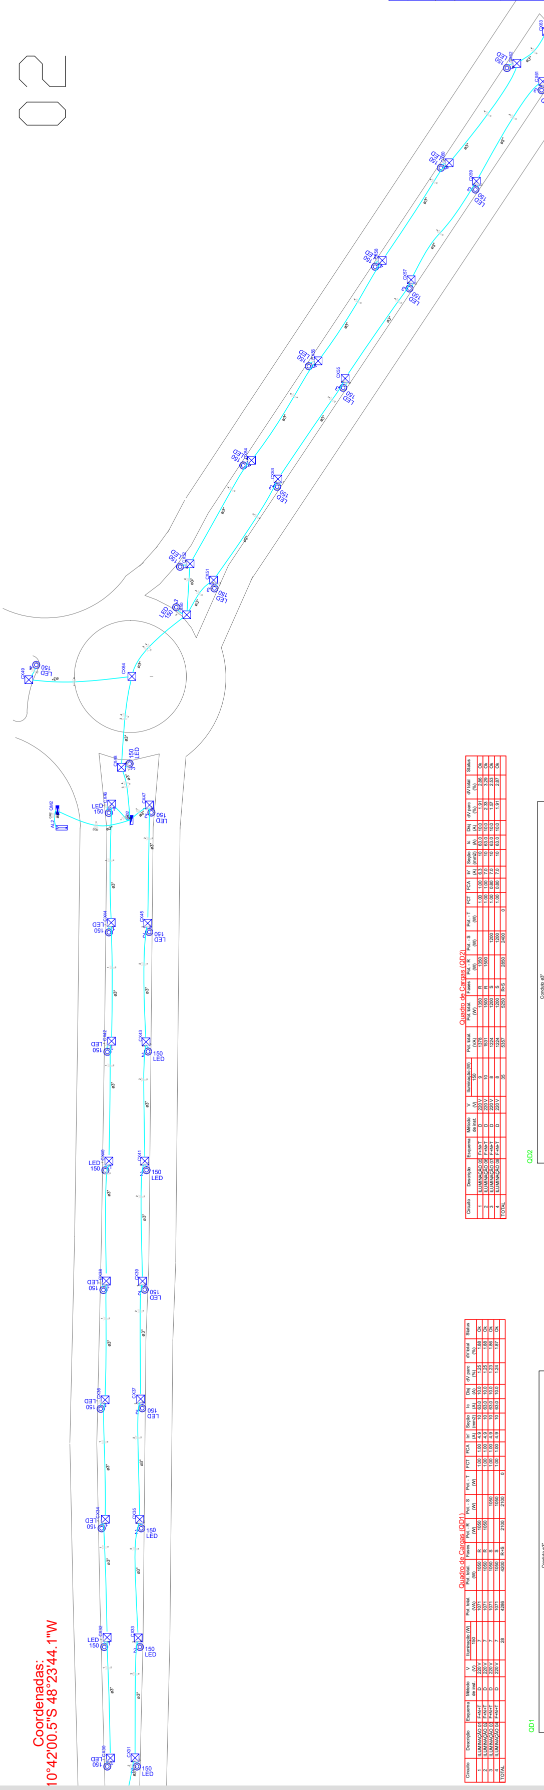
02
Coordenadas: 10°41'47.2"S 48°23'29.1"W
Coordenadas: 10°42'00.5"S 48°23'44.1"W
150 LED
QM2
ø3"

Lista de Materiais

Elétrica	
Acessórios uso geral	
Fita isolante autofusão	
20m	2 pç
Cabo Unipolar (cobre)	
Isol.PVC - 450/750V (ref. Pirelli Ecoplus BWF Flexível) 10 mm²	5262.00 m
Isol.PVC - 450/750V (ref. Pirelli Ecoplus BWF Flexível) 2,5 mm²	2626.50 m
Caixa de passagem - solo	
Alvenaria ou prémoldada 400x400x400 mm	63 pç
Aterramento	
Haste de aterramento 2400mm x 3/4"	63 pç
Grampo p/ haste de aterramento Reforçado	63 pç
Dispositivo de Proteção	
Disjuntor Unipolar Termomagnético - norma DIN	
10 A	8 pç
50 A	2 pç
Dispositivo de proteção contra surto 275 V - 40 KA	6 pç
Dispositivo de Comando	
Contator Tripolar 12 A	2 pç
Relé fotoelétrico 4 pinos 1000 W	2 pç
Base p/ Relé fotoelétrico 4 pinos	2 pç
Eletroduto PVC flexível	
Eletroduto leve 3/4"	854.30 m
Eletroduto pesado 3"	2567.10 m
Lâmpada LED	
Luminária LED Iluminação Pública	
Luminária 150W	63 pç
Poste Ornamental Iluminação Pública	
Poste aço galvanizado com braço 3 metros	
Poste 10m	63 pç
Material p/ entrada serviço	
Padrão de energia bifásico	2 pç
Ramal de Entrada	
Fases, Neutro e Terra	10 mm²
Haste de aterramento aço/cobre D=3/4", comprimento 2,4 m	1 pç
Caixa inspeção aterramento 250x250x400 mm	1 pç
Caixa CMI-02	1 pç
Poste de Concreto duplo T 100 daN, L=7,0m	1 pç
Quadro distrib. chapa pintada - embutir	
Bifásico	
Cap. 24 disj. unip.	2 pç

BREVE DESCRITIVO DO EMPREENDIMENTO

Projeto elétrico iluminação pública do Anel Viáriol de Porto Nacional - TO

OBSERVAÇÃO

Sem observações.

DADOS DO PROJETO:

Endereço: Anel Viário
Cidade / Setor: Porto Nacional -TO
Proprietário: Prefeitura Municipal de Porto Nacional - TO
Autor do Projeto: Rodrigo Neres Lompa
Resp. Técnico: Rodrigo Neres Lompa
Coordenadas Geográficas: Fuso: 22L
X: Latitude 784959 Y: Longitude 8816059

Prefeitura Municipal de Porto Nacional - TO
Proprietário:

RODRIGO NERES LOMPA:03398659110
Assinado de forma digital por RODRIGO NERES LOMPA:03398659110

Rodrigo Neres Lompa
Autor do Projeto
2418403335
Nº Crea:

Rodrigo Neres Lompa
Resp. Técnico:
2418403335
Nº Crea:

PROJETO ELETRICO

PROJETO ELÉTRICO ILUMINAÇÃO PÚBLICA ANEL VIÁRIO.

Nº DESENHO 5/8

Projetista: Rodrigo Neres Lompa
Data Completa: 14/01/2026
Escala: DIVERSAS

Legenda

⧓	Caixa de medição embutir a 1,60m do piso
⊠	Caixa de passagem de embutir no piso
↑	Entrada de serviço aérea - Saída aérea
◎ 150 LED 1	Luminária 150W
◪	Quadro de distribuição - embutir a 1,50m do piso

Quadro de Cargas (QD2)

Circuito	Descrição	Esquema	Método de inst.	V (V)	Iluminação (W) 150	Pot. total. (VA)	Pot. total. (W)	Fases	Pot. - R (W)	Pot. - S (W)	Pot. - T (W)	FCT	FCA	In' (A)	Seção (mm2)	Ic (A)	Disj (A)	dV parc (%)	dV total (%)	Status
1	ILUMINAÇÃO 05	F+N+T	D	220 V	9	1378	1350	R	1350			1.00	1.00	6.3	10	63.0	10.0	1.91	2.86	Ok
2	ILUMINAÇÃO 06	F+N+T	D	220 V	10	1531	1500	R	1500			1.00	1.00	7.0	10	63.0	10.0	2.33	3.29	Ok
3	ILUMINAÇÃO 07	F+N+T	D	220 V	8	1224	1200	S		1200		1.00	0.80	7.0	10	63.0	10.0	1.57	2.53	Ok
4	ILUMINAÇÃO 08	F+N+T	D	220 V	8	1224	1200	S		1200		1.00	0.80	7.0	10	63.0	10.0	1.91	2.87	Ok
TOTAL					35	5357	5250	R+S	2850	2400	0									

QD2

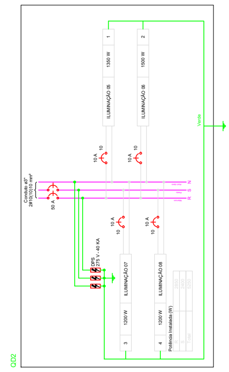

Quadro de Cargas (QD1)

Circuito	Descrição	Esquema	Método de inst.	V (V)	Iluminação (W) 150	Pot. total. (VA)	Pot. total. (W)	Fases	Pot. - R (W)	Pot. - S (W)	Pot. - T (W)	FCT	FCA	In' (A)	Seção (mm2)	Ic (A)	Disj (A)	dV parc (%)	dV total (%)	Status
1	ILUMINAÇÃO 01	F+N+T	D	220 V	7	1071	1050	R	1050			1.00	1.00	4.9	10	63.0	10.0	1.25	1.88	Ok
2	ILUMINAÇÃO 02	F+N+T	D	220 V	7	1071	1050	R	1050			1.00	1.00	4.9	10	63.0	10.0	1.25	1.88	Ok
3	ILUMINAÇÃO 03	F+N+T	D	220 V	7	1071	1050	S		1050		1.00	1.00	4.9	10	63.0	10.0	1.23	1.86	Ok
4	ILUMINAÇÃO 04	F+N+T	D	220 V	7	1071	1050	S		1050		1.00	1.00	4.9	10	63.0	10.0	1.24	1.87	Ok
TOTAL					28	4286	4200	R+S	2100	2100	0									

QD1

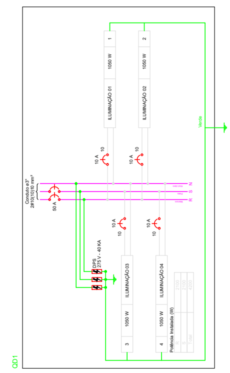

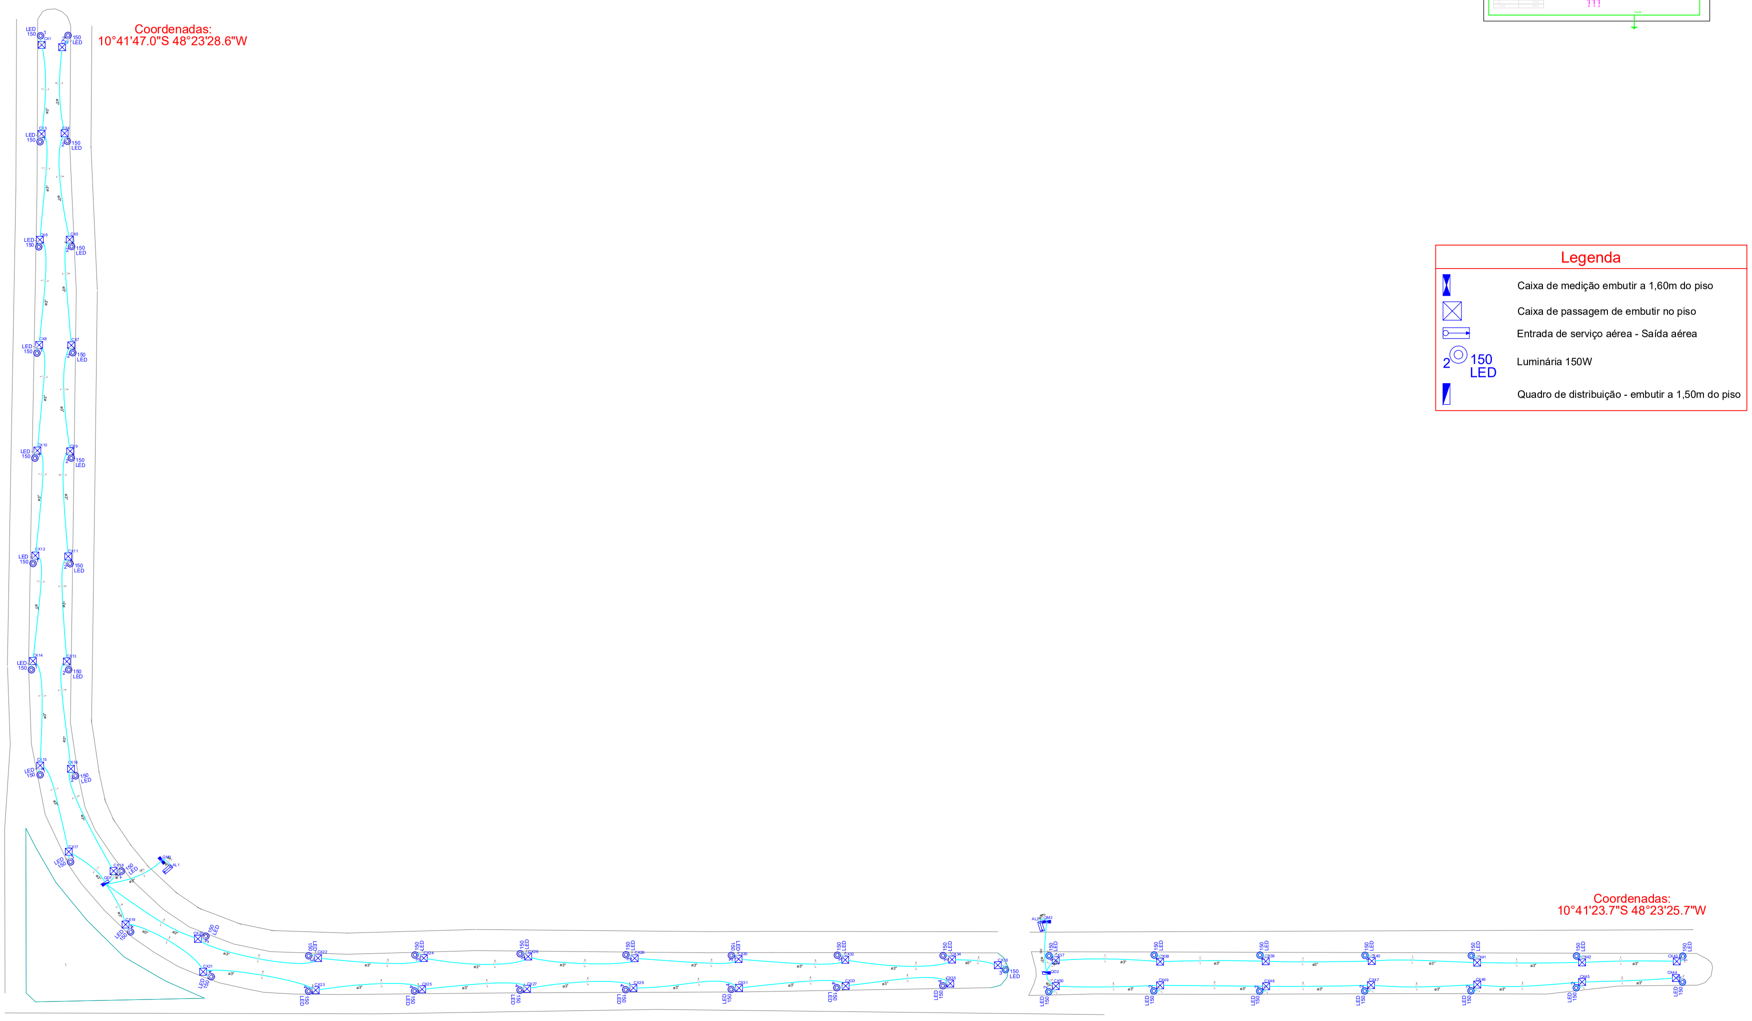

Quadro de Cargas (QD1)

Circuito	Descrição	Esquema	Método de inst.	V (V)	Iluminação (W) 150	Pot. total (VA)	Pot. total (W)	Fases	Pot. - R (W)	Pot. - S (W)	Pot. - T (W)	FCT	FCA	In' (A)	Seção (mm2)	Ic (A)	Disj (A)	dV parc (%)	dV total (%)	Status
1	ILUMINAÇÃO 01	F+N+T	D	220 V	9	1378	1350	R	1350			1.00	1.00	6.3	10	73.0	10.0	1.96	2.79	Ok
2	ILUMINAÇÃO 02	F+N+T	D	220 V	9	1378	1350	R	1350			1.00	1.00	6.3	10	63.0	10.0	1.90	2.73	Ok
3	ILUMINAÇÃO 03	F+N+T	D	220 V	9	1378	1350	S		1350		1.00	1.00	6.3	10	63.0	10.0	2.30	3.13	Ok
4	ILUMINAÇÃO 04	F+N+T	D	220 V	9	1378	1350	S		1350		1.00	1.00	6.3	10	63.0	10.0	1.98	2.81	Ok
TOTAL					36	5510	5400	R+S	2700	2700	0									

QD1

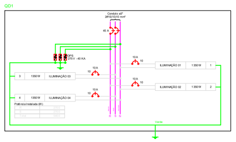

Quadro de Cargas (QD2)

Circuito	Descrição	Esquema	Método de inst.	V (V)	Iluminação (W) 150	Pot. total (VA)	Pot. total (W)	Fases	Pot. - R (W)	Pot. - S (W)	Pot. - T (W)	FCT	FCA	In' (A)	Seção (mm2)	Ic (A)	Disj (A)	dV parc (%)	dV total (%)	Status
1	ILUMINAÇÃO 06	F+N+T	D	220 V	7	1071	1050	R	1050			1.00	1.00	4.9	6	47.0	10.0	1.85	2.77	Ok
2	ILUMINAÇÃO 07	F+N+T	D	220 V	7	1071	1050	R	1050			1.00	1.00	4.9	6	47.0	10.0	1.86	2.78	Ok
TOTAL					14	2143	2100	R	2100	0	0									

QD2

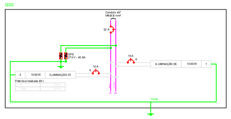

Legenda

⧗	Caixa de medição embutir a 1,60m do piso
☒	Caixa de passagem de embutir no piso
⊸	Entrada de serviço aérea - Saída aérea
2 ◎ 150 LED	Luminária 150W
◪	Quadro de distribuição - embutir a 1,50m do piso

Lista de Materiais

Elétrica	**Acessórios uso geral**	
	Fita isolante autofusão 20m	2 pç
	Cabo Unipolar (cobre)	
	Isol.PVC - 450/750V (ref. Pirelli Ecoplus BWF Flexível) 10 mm²	3029.00 m
	Isol.PVC - 450/750V (ref. Pirelli Ecoplus BWF Flexível) 6 mm²	1702.88 m
	Isol.PVC - 450/750V (ref. Pirelli Ecoplus BWF Flexível) 2,5 mm²	2042.52 m
	Caixa de passagem - solo	
	Alvenaria ou prémoldada 400x400x400 mm	50 pç
	Aterramento	
	Haste de aterramento 2400mm x 3/4"	50 pç
	Grampo p/ haste de aterramento Reforçado	50 pç
	Dispositivo de Proteção	
	Disjuntor Unipolar Termomagnético - norma DIN 10 A	6 pç
	32 A	1 pç
	50 A	1 pç
	Dispositivo de proteção contra surto 275 V - 40 KA	5 pç
	Dispositivo de Comando	
	Contator Tripolar 12 A	2 pç
	Relé fotoelétrico 4 pinos 1000 W	2 pç
	Base p/ Relé fotoelétrico 4 pinos	2 pç
	Eletroduto PVC flexível	
	Eletroduto leve 3/4"	677.50 m
	Eletroduto pesado 3"	2071.80 m
	Lâmpada LED	
	Luminária LED Iluminação Pública Luminária 150W	50 pç
	Poste Ornamental Iluminação Pública	
	Poste aço galvanizado com braço 3 metros Poste 10m	50 pç
	Material p/ entrada serviço	
	Padrão de energia bifásico	1 pç
	Ramal de Entrada Fases, Neutro e Terra	10 mm²
	Haste de aterramento aço/cobre D=3/4", comprimento 2,4 m	1 pç
	Caixa inspeção aterramento 250x250x400 mm	1 pç
	Caixa CMI-02	1 pç
	Poste de Concreto duplo T 100 daN, L=7,0m	1 pç
	Padrão de energia monofásico	1 pç
	Ramal de Entrada Fases, Neutro e Terra	6 mm²
	Haste de aterramento aço/cobre D=3/4", comprimento 2,4 m	1 pç
	Caixa inspeção aterramento 250x250x400 mm	1 pç
	Caixa CMI-02	1 pç
	Poste de Concreto duplo T 100 daN, L=7,0m	1 pç
	Quadro distrib. chapa pintada - embutir	
	Barr. bif., no Fuse+disj. geral - UL (Ref. Cemar) Cap. 20 disj. unip. - In barr. 100 A	1 pç
	Quadro distrib. chapa pintada - embutir	
	Sem barr. - DIN (Ref. Cemar) Cap. 12 disj. unip.	1 pç

BREVE DESCRITIVO DO EMPREENDIMENTO

Projeto elétrico iluminação pública do Anel Viário de Porto Nacional - TO

OBSERVAÇÃO

Sem observações.

DADOS DO PROJETO:

Endereço: Anel Viário
Cidade / Setor: Porto Nacional -TO
Proprietário: Prefeitura Municipal de Porto Nacional - TO
Autor do Projeto: Rodrigo Neres Lompa
Resp. Técnico: Rodrigo Neres Lompa
Coordenadas Geográficas: Fuso: 22L
X: Latitude 785567 Y: Longitude 8816863

Prefeitura Municipal de Porto Nacional - TO
Proprietário:

Rodrigo Neres Lompa
Autor do Projeto
2418403335
Nº Crea:

RODRIGO NERES LOMPA:03398659110
Assinado de forma digital por RODRIGO NERES LOMPA:03398659110

Rodrigo Neres Lompa
Resp. Técnico:
2418403335
Nº Crea:

PROJETO ELETRICO
Nº DESENHO

PROJETO ELÉTRICO ILUMINAÇÃO PÚBLICA ANEL VIÁRIO.
6/7

Projetista: Rodrigo Neres Lompa
Data Completa: 14/01/2026
Escala: DIVERSAS

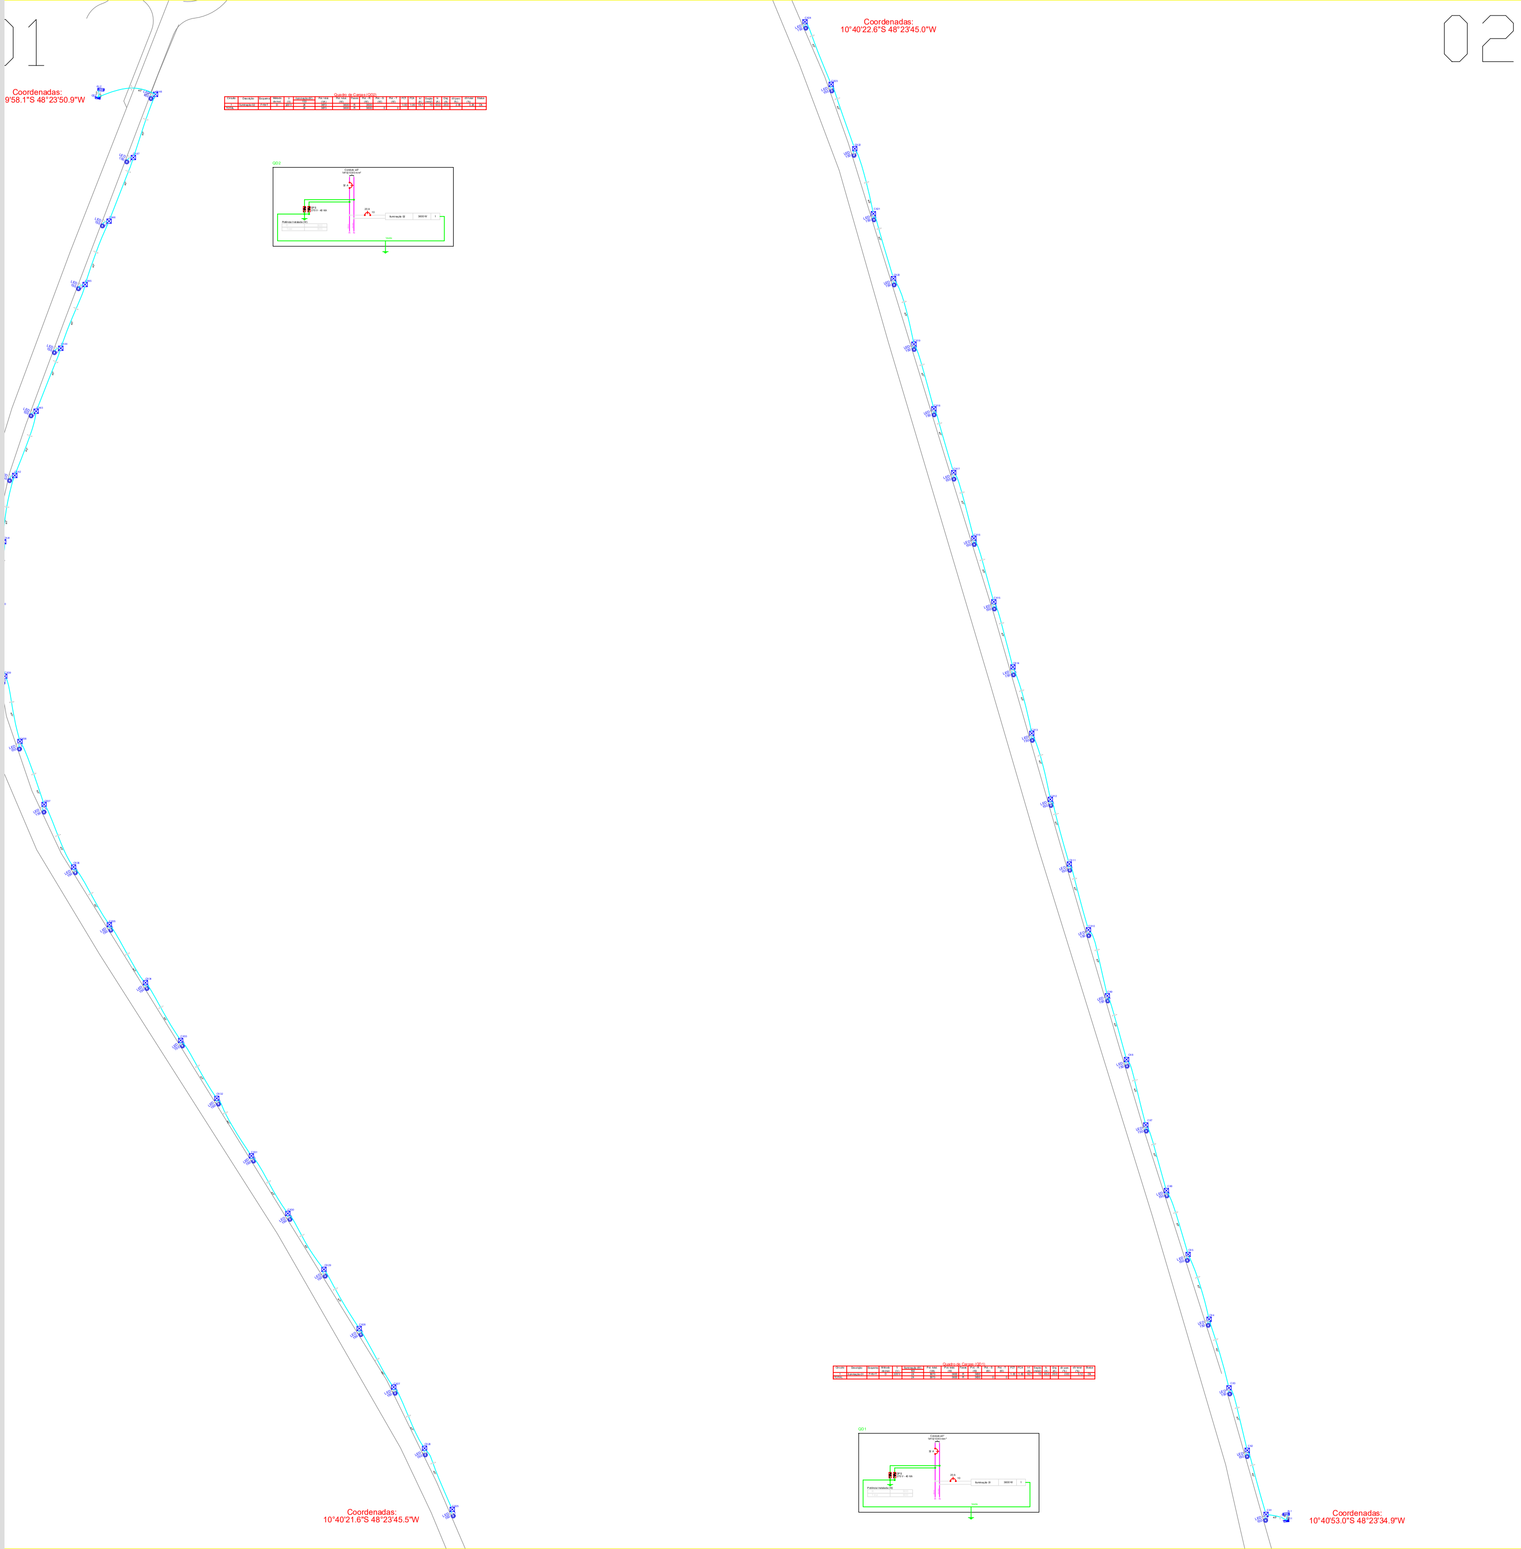
01
Coordenadas:
9°58.1"S 48°23'50.9"W
Coordenadas:
10°40'22.6"S 48°23'45.0"W
Coordenadas:
10°40'21.6"S 48°23'45.5"W
Coordenadas:
10°40'53.0"S 48°23'34.9"W
02

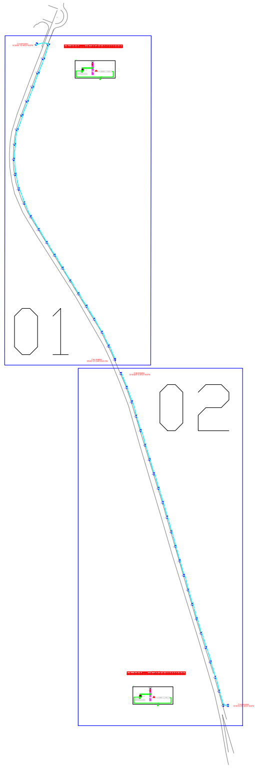

Lista de Materiais

Elétrica	**Acessórios uso geral**	
	Fita isolante autofusão 20m	2 pç
	Cabo Unipolar (cobre)	
	Isol.PVC - 450/750V (ref. Pirelli Ecoplus BWF Flexível) 10 mm²	4196.00 m
	Isol.PVC - 450/750V (ref. Pirelli Ecoplus BWF Flexível) 2,5 mm²	2043.20 m
	Caixa de passagem - solo	
	Alvenaria ou prémoldada 400x400x400 mm	48 pç
	Aterramento	
	Haste de aterramento 2400mm x 3/4"	48 pç
	Grampo p/ haste de aterramento Reforçado	48 pç
	Dispositivo de Proteção	
	Disjuntor Unipolar Termomagnético - norma DIN	
	20 A	2 pç
	32 A	2 pç
	Dispositivo de proteção contra surto 275 V - 40 KA	4 pç
	Dispositivo de Comando	
	Contator Tripolar 12 A	2 pç
	Relé fotoelétrico 4 pinos 1000 W	2 pç
	Base p/ Relé fotoelétrico 4 pinos	2 pç
	Eletroduto PVC flexível	
	Eletroduto leve 3/4"	681.10 m
	Eletroduto pesado 3"	2097.80 m
	Lâmpada LED	
	Luminária LED Iluminação Pública Luminária 150W	48 pç
	Poste Ornamental Iluminação Pública	
	Poste aço galvanizado com braço 3 metros Poste 10m	48 pç
	Material p/ entrada serviço	
	Padrão de energia monofásico	2 pç
	Ramal de Entrada Fases, Neutro e Terra	10 mm²
	Haste de aterramento aço/cobre D=3/4", comprimento 2,4 m	1 pç
	Caixa inspeção aterramento 250x250x400 mm	1 pç
	Caixa CMI-02	1 pç
	Poste de Concreto duplo T 100 daN, L=7,0m	1 pç
	Quadro distrib. chapa pintada - embutir	
	Sem barr. - DIN (Ref. Cemar) Cap. 12 disj. unip.	2 pç

Legenda

☒	Caixa de passagem de embutir no piso
○→	Entrada de serviço aérea - Saída aérea
1 ◎ 150 LED	Luminária 150W
▮	Quadro de distribuição - embutir a 1,50m do piso

BREVE DESCRITIVO DO EMPREENDIMENTO

Projeto elétrico iluminação pública do Anel Viáriol de Porto Nacional - TO

OBSERVAÇÃO

Sem observações.

DADOS DO PROJETO:

Endereço: Anel Viário
Cidade / Setor: Porto Nacional -TO
Proprietário: Prefeitura Municipal de Porto Nacional - TO
Autor do Projeto: Rodrigo Neres Lompa
Resp. Técnico: Rodrigo Neres Lompa
Coordenadas Geográficas: Fuso: 22L
X: Latitude 784965 Y: Longitude 8818775

Prefeitura Municipal de Porto Nacional - TO
Proprietário:

RODRIGO NERES LOMPA:03398659110 Assinado de forma digital por RODRIGO NERES LOMPA:03398659110

Rodrigo Neres Lompa 2418403335
Autor do Projeto Nº Crea:

Rodrigo Neres Lompa 2418403335
Resp. Técnico: Nº Crea:

PROJETO ELETRICO

Nº DESENHO

PROJETO ELÉTRICO ILUMINAÇÃO PÚBLICA ANEL VIÁRIO.

7/8

Projetista: Rodrigo Neres Lompa
Data Completa: 14/01/2026
Escala: DIVERSAS

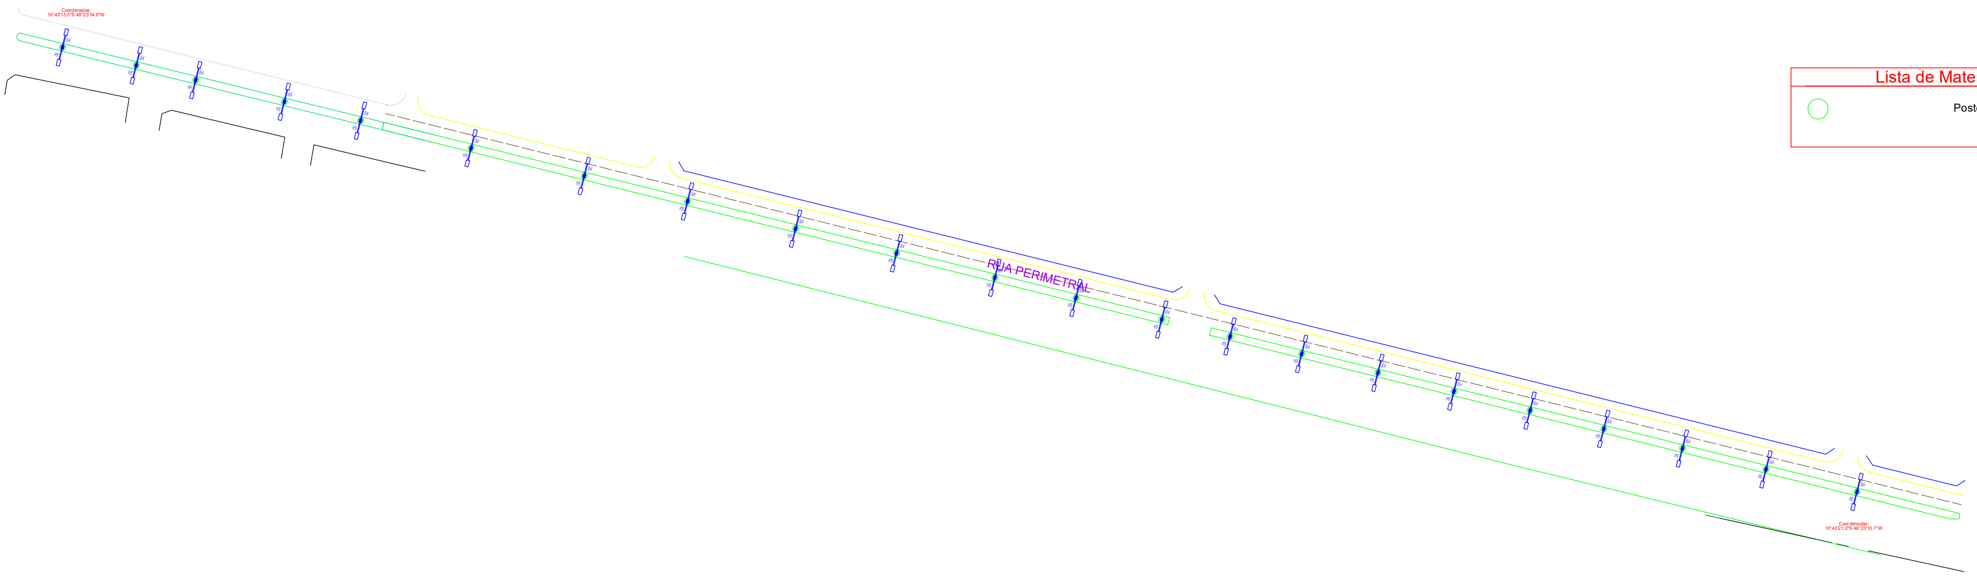

Lista de Materiais

Elétrica	Acessórios uso geral	
	Fita isolante autofusão 20m	1 pç
	Cabo Unipolar (cobre)	
	Isol.HEPR - ench.XLPE - 0,6/1kV 2.5 mm²	440.00 m
	Luminária Iluminação pública	
	LED 150W	44 pç
	Dispositivo de Iluminação	
	Relé fotoelétrico 1000W, 220V	22 pç
	Base p/ relé	22 pç
	Dispositivos Eletricos	
	Conector Perfurante 10mm-95mm	22 pç

Lista de Materiais

○	Poste Existente

DADOS DO PROJETO:

Endereço: Rua Perimetral

Cidade / Setor: Porto Nacional / Setor das Mansões

Proprietário: Secretaria Municipal de Infraestrutura e Desenvolvivento Urbano

Autor do Projeto: Rodrigo Neres Lompa

Resp. Técnico: Engenheiro Eletricista Rodrigo Neres Lompa

Coordenadas Geográficas (UTM): FUSO: 22L

785446 Y: 8813595

RODRIGO NERES LOMPA:03398659110 Assinado de forma digital por RODRIGO NERES LOMPA:03398659110

Resp. Técnico:

2418403335

Nº Crea:

LEVANTAMENTO ILUMINAÇÃO SETOR DAS MANSÕES

PRANCHA

LEVANTAMENTO ILUMINAÇÃO RUA PERIMETRAL

1/1

Projetista:	Data Completa:	Escala:
Rodrigo Neres Lompa	14/01/2026	DIVERSAS

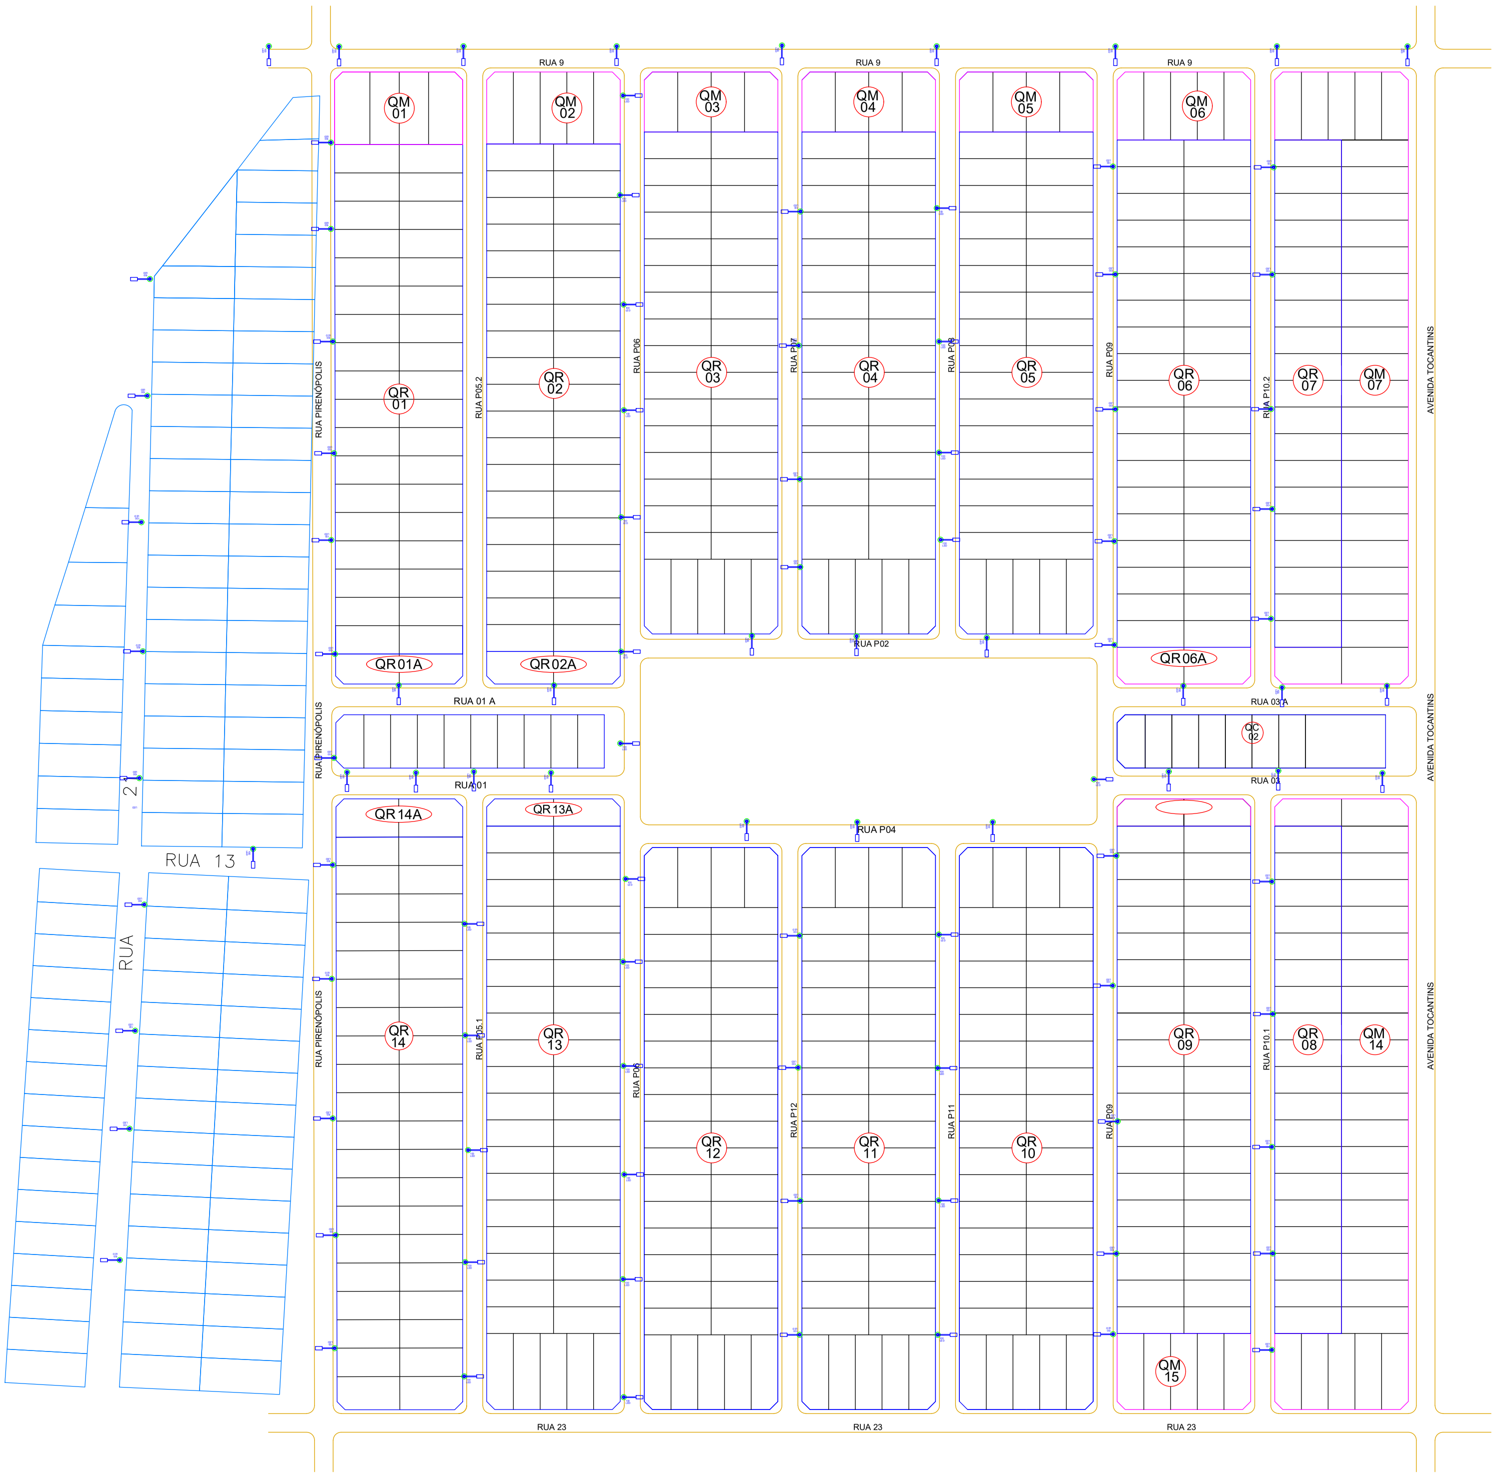

Lista de Materiais

Elétrica	Acessórios uso geral	
	Fita isolante autofusão 20m	2 pç
	Cabo Unipolar (cobre)	
	Isol.HEPR - ench.XLPE - 0,6/1kV 2.5 mm²	847.00 m
	Luminária Iluminação pública	
	LED 100W	121 pç
	Dispositivo de Iluminação	
	Relé fotoelétrico 1000W, 220V	121 pç
	Dispositivos Eletricos	
	Conector Perfurante 10mm-95mm	242 pç

DADOS DO PROJETO:

Endereço: Irmâ Edila

Cidade / Setor: Porto Nacional / Irmâ Edila

Proprietário: Secretaria Municipal de Infraestrutura e Desenvolvivento Urbano

Autor do Projeto: Rodrigo Neres Lompa

Resp. Técnico: Engenheiro Eletricista Rodrigo Neres Lompa

Coordenadas Geográficas (UTM): FUSO: 22L
783673 Y: 8818628

RODRIGO NERES LOMPA:03398659110 Assinado de forma digital por RODRIGO NERES LOMPA:03398659110

Resp. Técnico:

Nº Crea: 2418403335

LEVANTAMENTO ILUMINAÇÃO IRMÃ EDILA

PRANCHA

LEVANTAMENTO ILUMINAÇÃO IRMÂ EDILA

1/1

Projetista: Rodrigo Neres Lompa
Data Completa: 16/03/2026
Escala: DIVERSAS