
Documento assinado digitalmente por **RODRIGO NERES LOMPA**, em 20/08/2026 09:13:40

Confira a autenticidade com o código **miiRtOEZg** no endereço https://portonacional.gep.digital/verificacao

Início: 10°40'54.9"S 48°32'25.6"W

Fim: 10°40'59.9"S 48°32'04.8"W

Lista de Materiais	
Conjunto de poste ornamental	
Solar 9 metros	
90w	23 pç

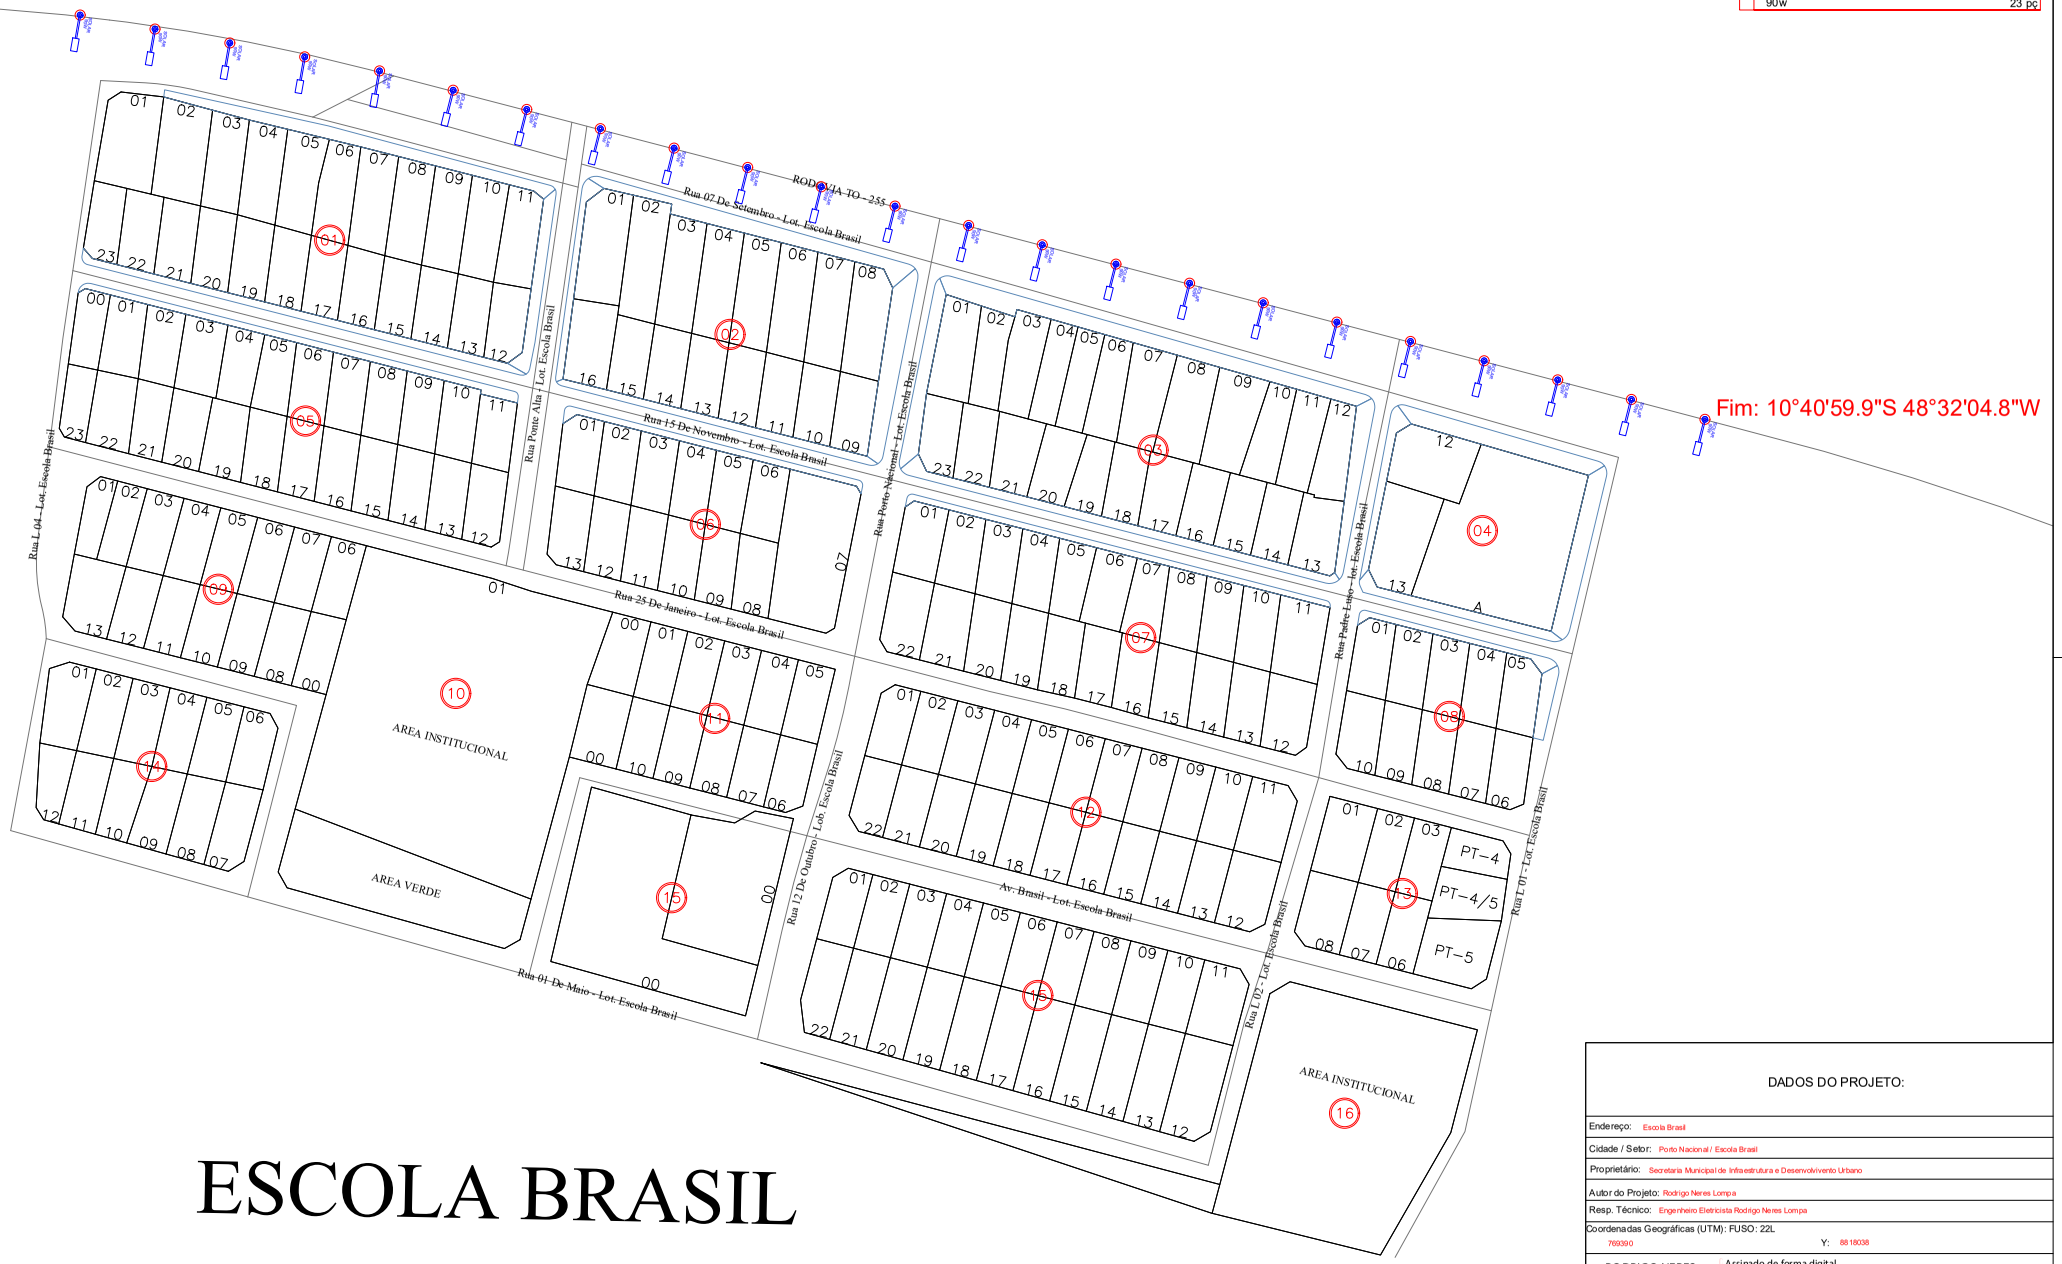

ESCOLA BRASIL

DADOS DO PROJETO:	
Endereço:	Escola Brasil
Cidade / Setor:	Porto Nacional / Escola Brasil
Proprietário:	Secretaria Municipal de Infraestrutura e Desenvolvivento Urbano
Autor do Projeto:	Rodrigo Neres Lompa
Resp. Técnico:	Engenheiro Eletricista Rodrigo Neres Lompa
Coordenadas Geográficas (UTM): FUSO: 22L	
769390	Y: 8818038

RODRIGO NERES LOMPA:03398659110 — Assinado de forma digital por RODRIGO NERES LOMPA:03398659110

Resp. Técnico: — 2418403335 — Nº Crea:

LEVANTAMENTO ILUMINAÇÃO ESCOLA BRASIL	PRANCHA
LEVANTAMENTO ILUMINAÇÃO SOLAR ESCOLA BRASIL	1/1

Projetista:	Data Completa:	Escala:
Rodrigo Neres Lompa	14/01/2026	DIVERSAS

PORTO NACIONAL

Documento assinado digitalmente por **RODRIGO NERES LOMPA**, em 20/08/2026 09:13:40

Confira a autenticidade com o código **miifRtOEZg** no endereço https://portonacional.gep.digital/verificacao

Quadro de Cargas (QD1)

Circuito	Descrição	Esquema	Método de inst.	V (V)	Iluminação (W)	Pot. total (VA)	Pot. total (W)	Fases	Pot. - R (W)	Pot. - S (W)	Pot. - T (W)	FCT	FCA	Iz (A)	Seção (mm2)	Ic (A)	Dut (%)	dV parc (%)	dV total (%)	Status
1	Iluminação 01	F+N+T	E	220 V	11	1664	1600	R	1600			1,00	0,65	10,7	10	10,0	10,0	0,91	0,91	Ok
2	Iluminação 02	F+N+T	E	220 V	11	1664	1600	R	1600			1,00	0,65	10,7	10	10,0	10,0	0,91	0,91	Ok
3	Iluminação 03	F+N+T	E	220 V	10	1561	1500	S		1500		1,00	0,65	10,7	10	10,0	10,0	0,85	0,85	Ok
4	Iluminação 04	F+N+T	E	220 V	10	1561	1500	S		1500		1,00	0,65	10,7	10	10,0	10,0	0,85	0,85	Ok
TOTAL					41	6290	6100	R+S	3200	3000	0									

Lista de Materiais

Acessórios uso geral
- Fita isolante autofusão 20m — 1,00
- Cabo Unipolar (cobre) 1kV PVC - 450/750V (ref. Pirelli Ecoplus BWF Flexível)
  - 10 mm² — 40,00 m
  - 2,5 mm² — 410,00 m

Dispositivo de Proteção
- Disjuntor Unipolar Termomagnético - norma DIN 10 A — 4 (+)
- Disjuntor bipolar termomagnético (380 V/220 V) - DIN) 50 A - 4,5 kA — 1 (+)
- Dispositivo de proteção contra surto 275 V - 40 kA — 3 (+)

Dispositivo de Comando
- Relé fotoelétrico 4 pinos 1000 W — 41 (+)

Condutor (Ir rede aérea de distribuição)
- Perfurante 1,5 a 10 mm² — 82 (+)

Haste
- Iluminação Pública 3,00m — 41 (+)

Poste de Concreto
- Duplo T - DT Poste 10 metros — 41 (+)

Luminária LED
- Luminária LED Iluminação Pública Luminária 150W — 41 (+)


Material de aterramento
- Padrão de entrega bifásico Haste de Aço 5/8" — 1 (+)
- Fase, Neutro e Terra — 10 m (+)
- Haste de aterramento apotcobre — 1 (+)
- D=3/4", comprimento 2,4 m
- Caixa inspeção aterramento 250x250x400 mm — 1 (+)
- Caixa CM-02 — 1 (+)
- Poste de Concreto duplo T 100 daN, h=9,0m — 1 (+)


Quadro de dis. (Caixa pintada - embutir)
- Sem barramento — 1,00

Legenda

- Caixa de medição embutir a 1,60m do piso
- Entrada de serviço aérea
- 150 LED — Luminária 150W
- Quadro de distribuição - embutir a 1,50m do piso

QD1

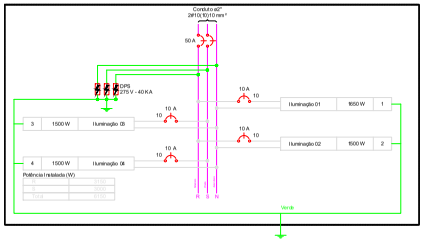

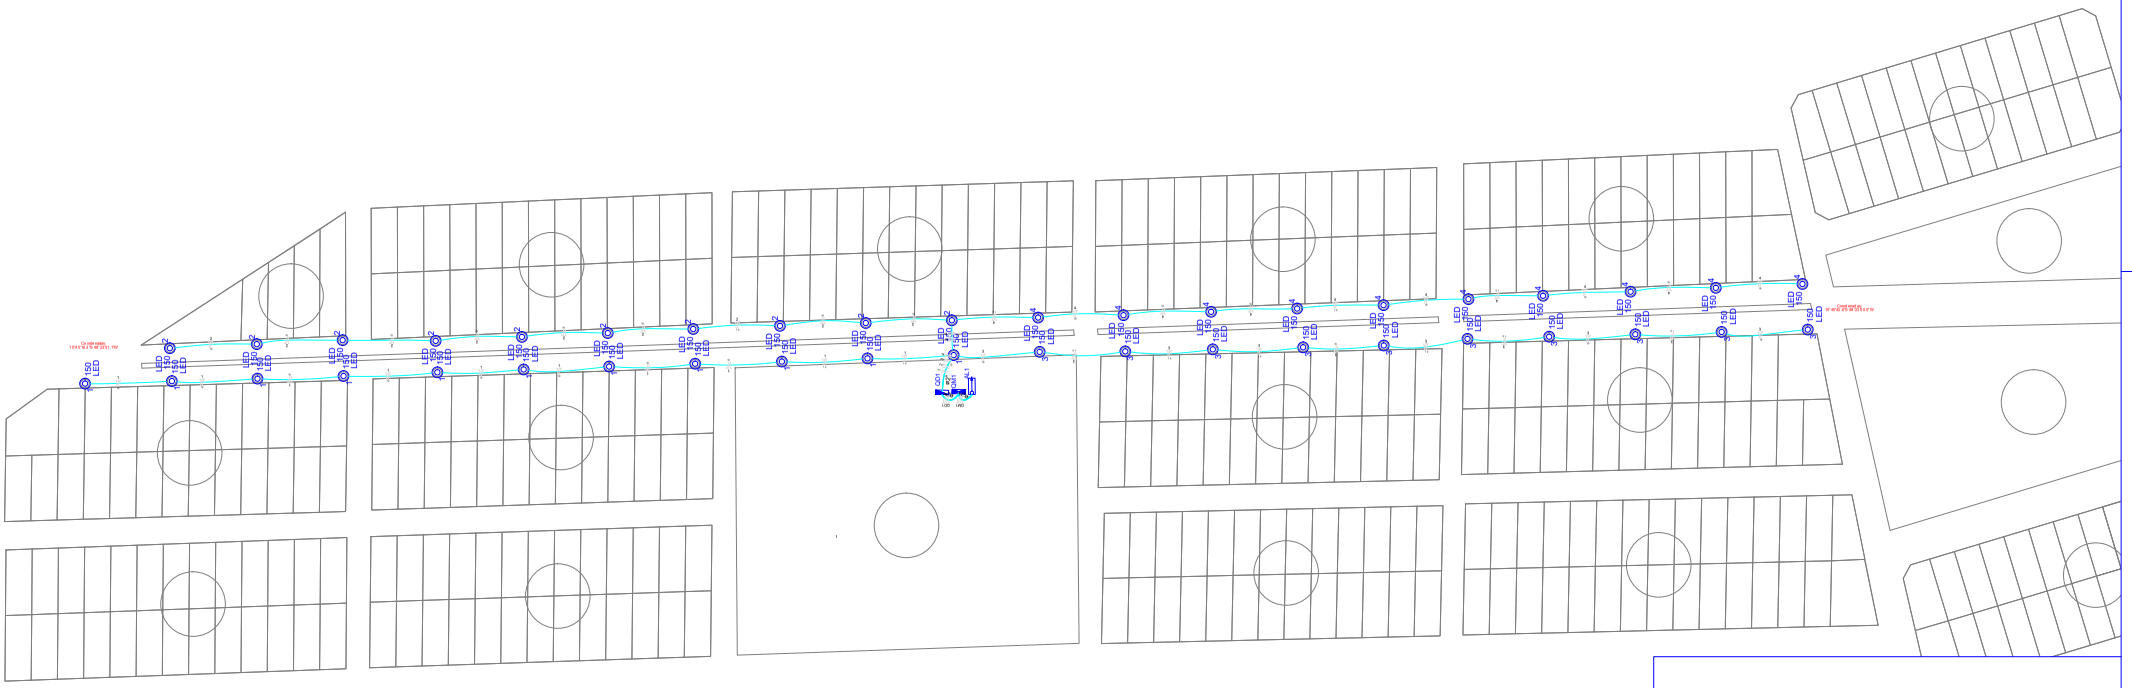

DADOS DO PROJETO:

Endereço:	Av. I
Cidade / Setor:	Porto Nacional / Novo Horizonte
Proprietário:	Secretaria Municipal de Infraestrutura e Desenvolvivento Urbano
Autor do Projeto:	Rodrigo Neres Lompa
Resp. Técnico:	Engenheiro Eletricista Rodrigo Neres Lompa
Coordenadas Geográficas (UTM): FUSO: 22L	
X: 784716	Y: 8818858

RODRIGO NERES LOMPA:03398659110 — Assinado de forma digital por RODRIGO NERES LOMPA:03398659110


Resp. Técnico: — 2418403335 Nº Crea:

LEVANTAMENTO ILUMINAÇÃO SETOR DAS MANSÕES

LEVANTAMENTO AV. I

PRANCHA 1/1

Projetista:	Data Completa:	Escala:
Rodrigo Neres Lompa	14/01/2026	DIVERSAS

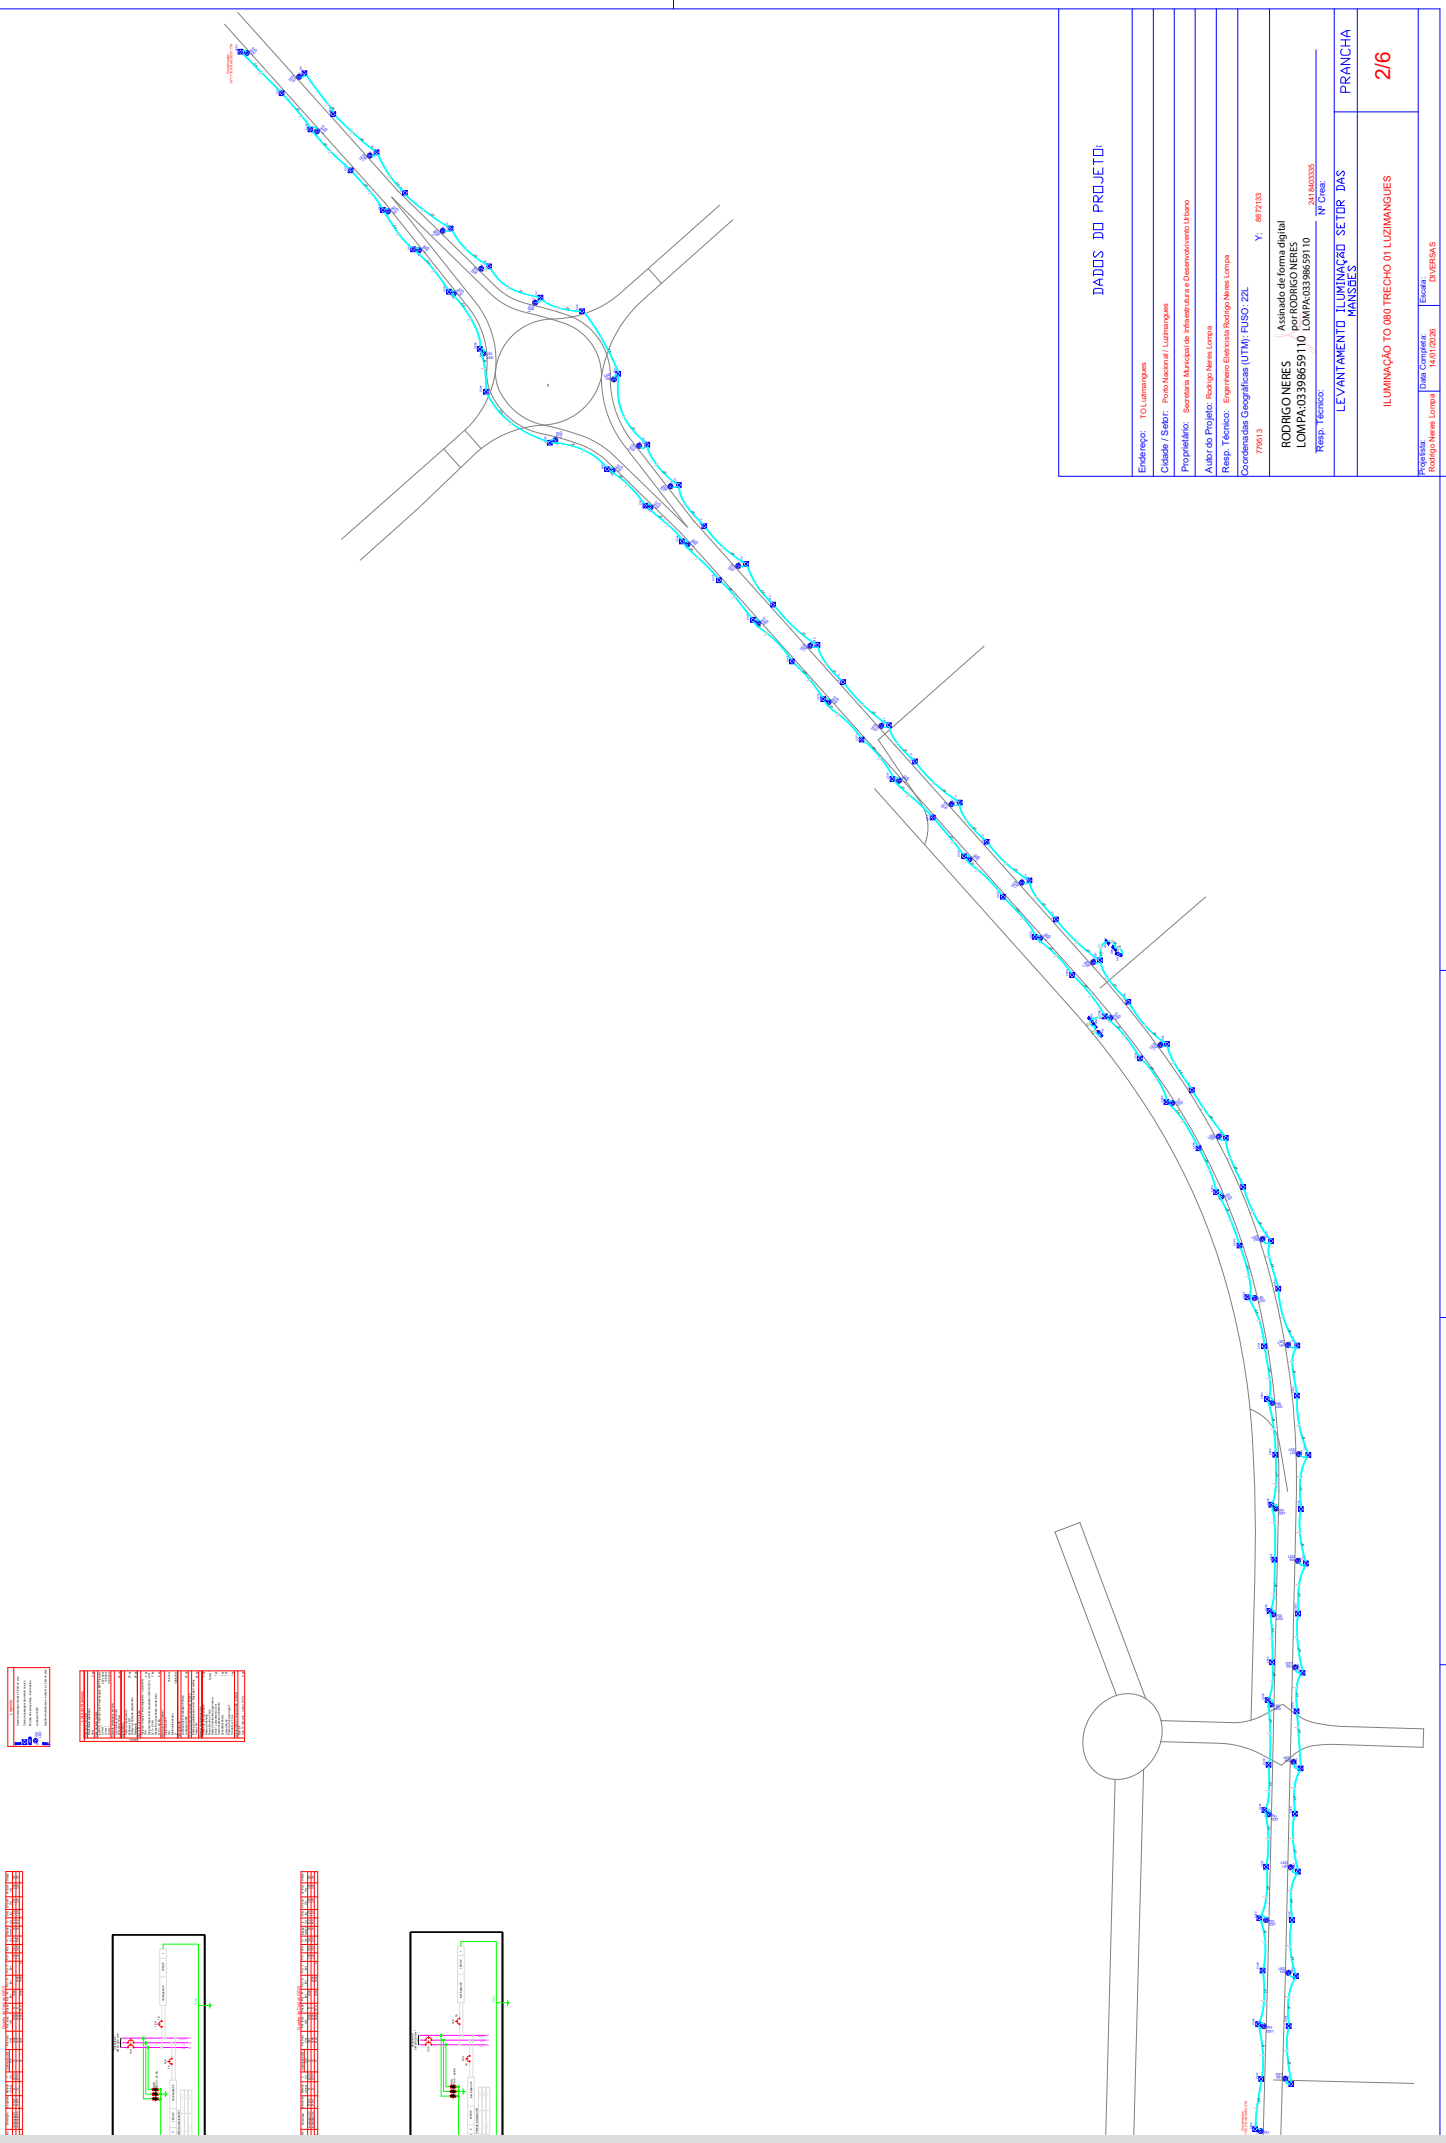

DADOS DO PROJETO:

Endereço: TO Luzimangues

Cidade / Setor: Porto Nacional / Luzimangues

Proprietário: Secretaria Municipal de Infraestrutura e Desenvolvimento Urbano

Autor do Projeto: Rodrigo Neres Lompa

Resp. Técnico: Engenheiro Eletricista Rodrigo Neres Lompa

Coordenadas Geográficas (UTM); FUSO: 22L

X: 779513 Y: 8972133

RODRIGO NERES LOMPA:03398659110 Assinado de forma digital por RODRIGO NERES LOMPA:03398659110

Resp. Técnico: Nº Crea: 241940533D

LEVANTAMENTO ILUMINAÇÃO SETOR DAS MANGUEIS

PRANCHA 2/6


ILUMINAÇÃO TO 080 TRECHO 01 LUZIMANGUES

Proprietário: Rodrigo Neres Lompa | Data Completa: 14/01/2026 | Escala: DIVERSAS


PORTO NACIONAL


Documento assinado digitalmente por
RODRIGO NERES LOMPA, em 20/08/2026 09:13:40

Confira a autenticidade com o código **miifRtOEZg**
no endereço https://portonacional.gep.digital/verificacao

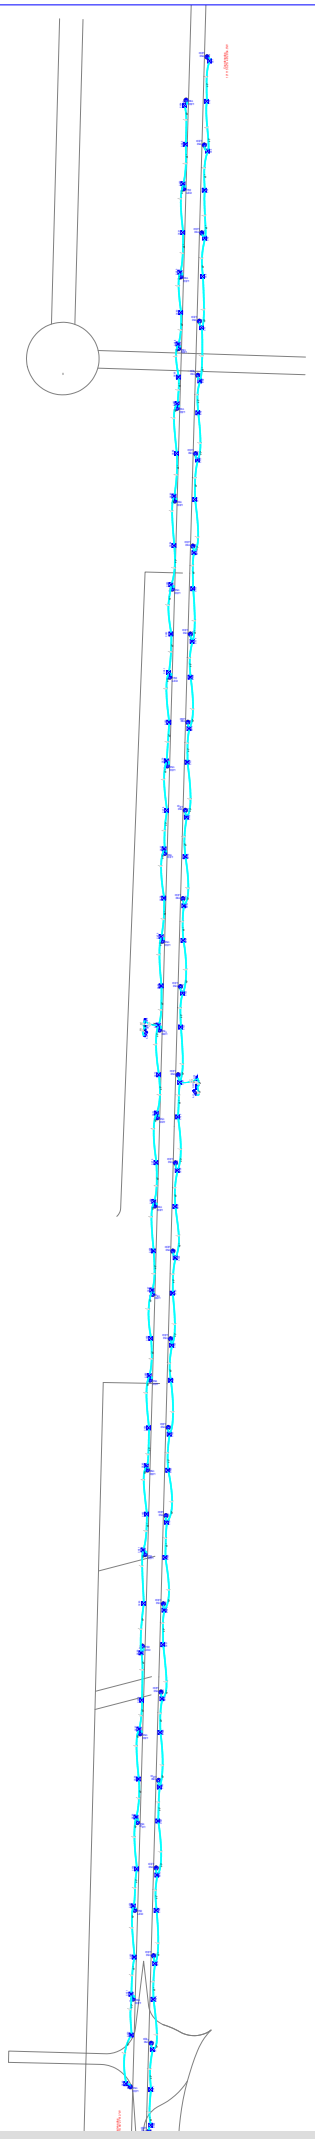



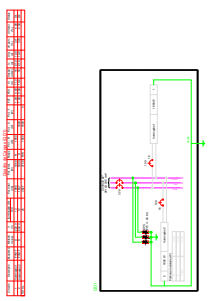

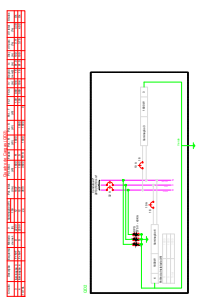

DADOS DO PROJETO:

Endereço: TO Luzimangues

Cidade / Setor: Porto Nacional / Luzimangues

Proprietário: Secretaria Municipal de Infraestrutura e Desenvolvimento Urbano

Autor do Projeto: Rodrigo Neres Lompa

Resp. Técnico: Engenheiro Eletricista Rodrigo Neres Lompa

Coordenadas Geográficas (UTM); FUSO: 22L

X: 779513 Y: 8872133

RODRIGO NERES LOMPA:03398659110 Assinado de forma digital por RODRIGO NERES LOMPA:03398659110

Resp. Técnico:

Nº Crea: 241940533D

LEVANTAMENTO ILUMINAÇÃO SETOR DAS MANSÕES

PRANCHA 3/6

ILUMINAÇÃO TO 080 TRECHO 02 LUZIMANGUES

Propietário: Rodrigo Neres Lompa | Data: Completa 14/01/2026 | Escala: DIVERSAS


PORTO NACIONAL

Documento assinado digitalmente por
RODRIGO NERES LOMPA, em 20/08/2026 09:13:40

Confira a autenticidade com o código **miifRtOEZg**
no endereço https://portonacional.gep.digital/verificacao


Documento assinado digitalmente por **RODRIGO NERES LOMPA**, em 20/08/2026 09:13:40

Confira a autenticidade com o código **miifRtOEZg** no endereço https://portonacional.gep.digital/verificacao

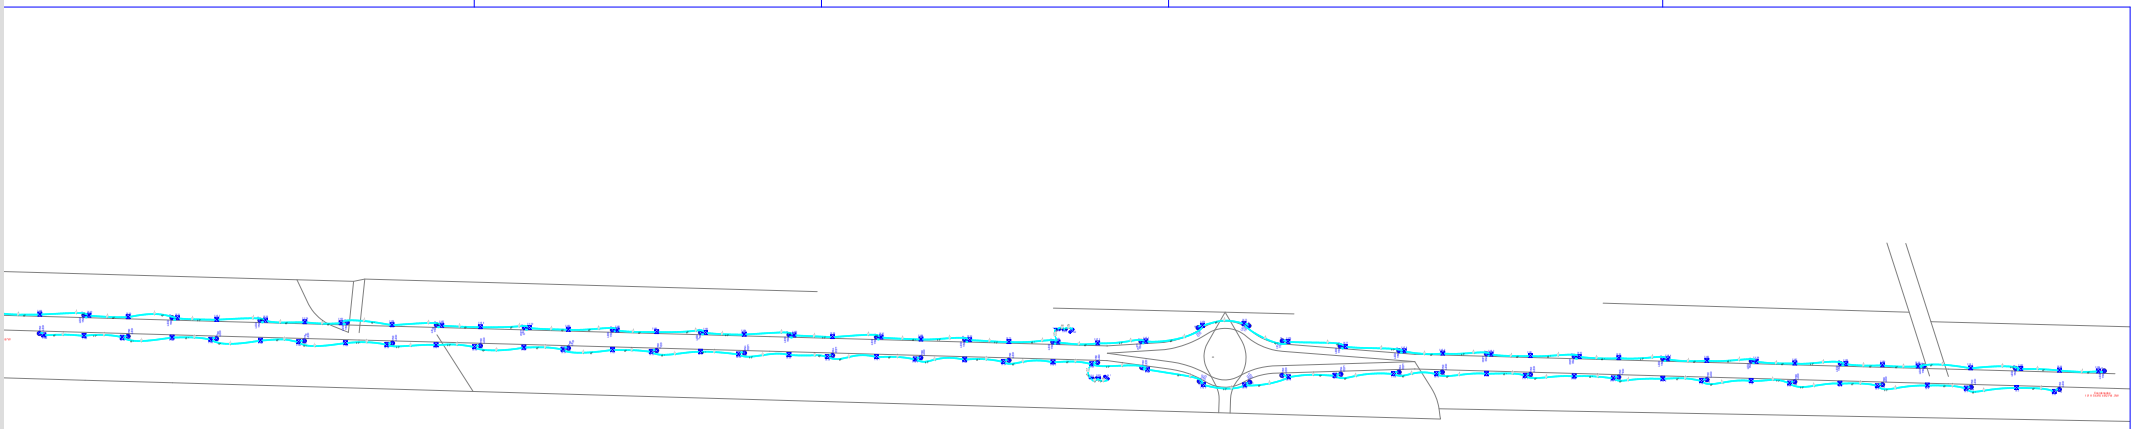






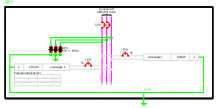





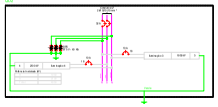

DADOS DO PROJETO:

Endereço:	TO Luzimangues
Cidade / Setor:	Porto Nacional / Luzimangues
Proprietário:	Secretaria Municipal de Infraestrutura e Desenvolvivento Urbano
Autor do Projeto:	Rodrigo Neres Lompa
Resp. Técnico:	Engenheiro Eletricista Rodrigo Neres Lompa
Coordenadas Geográficas (UTM): FUSO: 22L	
779513	Y: 8872133

RODRIGO NERES LOMPA:03398659110 Assinado de forma digital por RODRIGO NERES LOMPA:03398659110

Resp. Técnico: 2418403335 Nº Crea:


LEVANTAMENTO ILUMINAÇÃO SETOR DAS MANSÕES


PRANCHA

ILUMINAÇÃO TO 080 TRECHO 03 LUZIMANGUES

4/6

Projetista:	Data Completa:	Escala:
Rodrigo Neres Lompa	14/01/2026	DIVERSAS

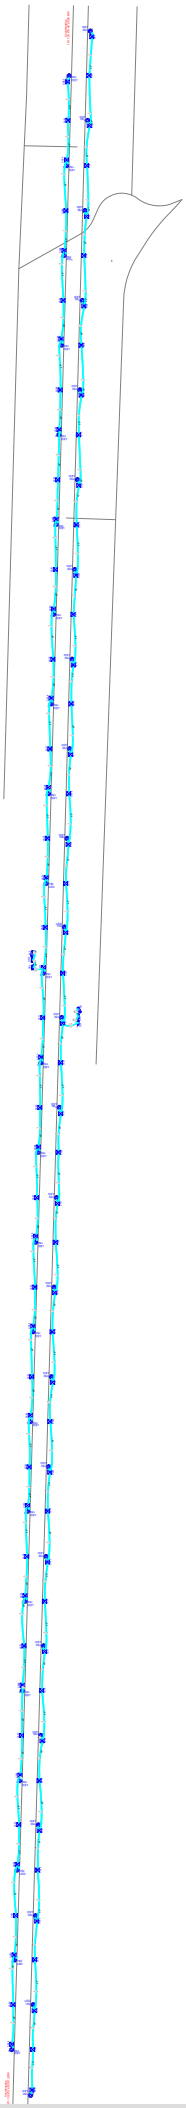

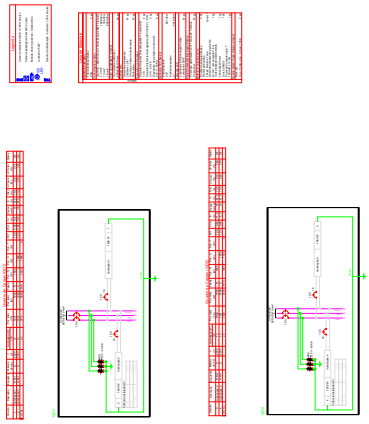

DADOS DO PROJETO:

Endereço: TO Luzimangues

Cidade / Setor: Porto Nacional / Luzimangues

Proprietário: Secretaria Municipal de Infraestrutura e Desenvolvimento Urbano

Autor do Projeto: Rodrigo Neres Lompa

Resp. Técnico: Engenheiro Eletricista Rodrigo Neres Lompa

Coordenadas Geográficas (UTM); FUSO: 22L

X: 779513 Y: 8872133

RODRIGO NERES LOMPA:03398659110 Assinado de forma digital por RODRIGO NERES LOMPA:03398659110

Resp. Técnico: Nº Creal: 241940033D

LEVANTAMENTO ILUMINAÇÃO SETOR DAS MANSÕES

PRANCHA 5/6


ILUMINAÇÃO TO 080 TRECHO 04 LUZIMANGUES

Proprietário: Rodrigo Neres Lompa | Data: Completa 14/07/2026 | Escala: DIVERSAS


PORTO NACIONAL

Documento assinado digitalmente por
RODRIGO NERES LOMPA, em 20/08/2026 09:13:40

Confira a autenticidade com o código **miifRtOEZg**
no endereço https://portonacional.gep.digital/verificacao

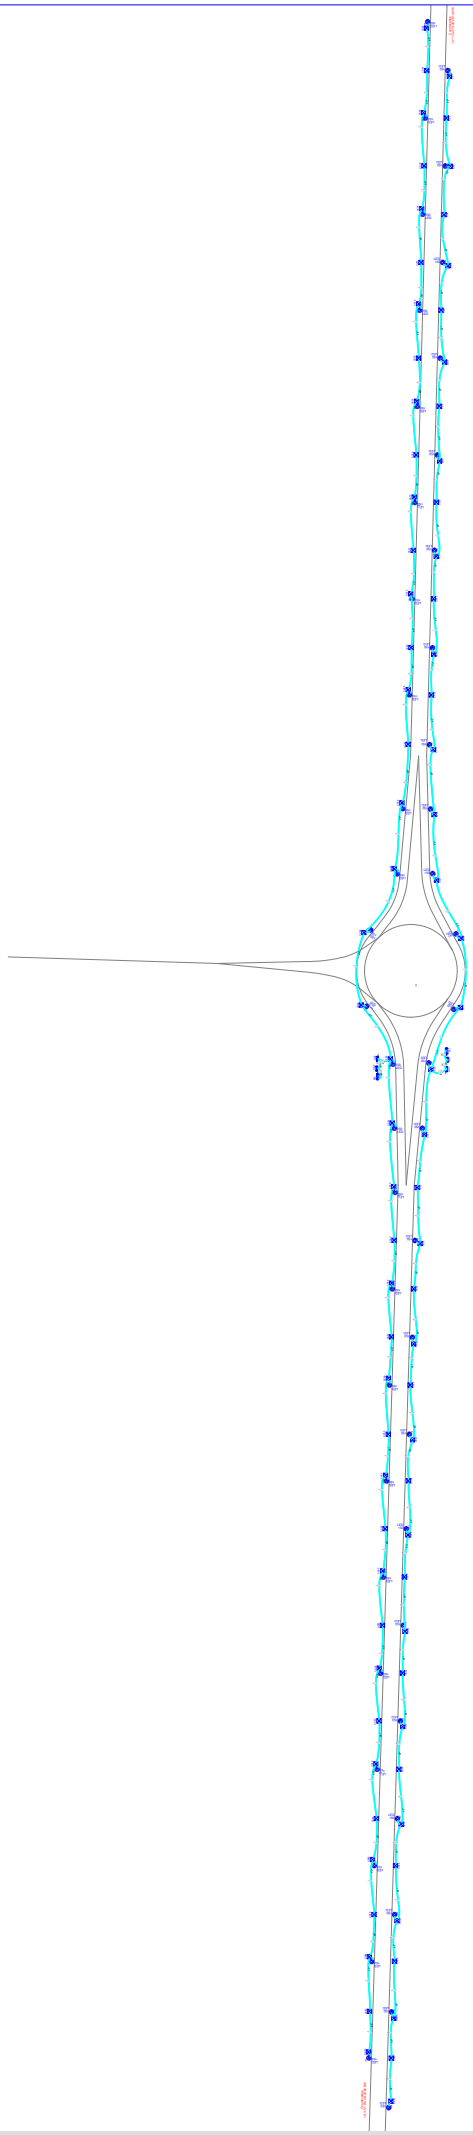



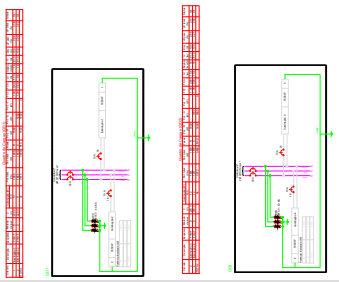

DADOS DO PROJETO:

Endereço: TO Luzimangues

Cidade / Setor: Porto Nacional / Luzimangues

Proprietário: Secretaria Municipal de Infraestrutura e Desenvolvimento Urbano

Autor do Projeto: Rodrigo Neres Lompa

Resp. Técnico: Engenheiro Eletricista Rodrigo Neres Lompa

Coordenadas Geográficas (UTM); FUSO: 22L

X: 779513 Y: 8872133

RODRIGO NERES LOMPA:03398659110 Assinado de forma digital por RODRIGO NERES LOMPA:03398659110

Nº Creal: 241940533D

Resp. Técnico:

LEVANTAMENTO ILUMINAÇÃO SETOR DAS MANGUEIRAS

ILUMINAÇÃO TO 080 TRECHO 05 LUZIMANGUES

PRANCHA 6/6

Proprietário: Rodrigo Neres Lompa | Data: Completa 14/01/2026 | Escala: DIVERSAS

PORTO NACIONAL

Documento assinado digitalmente por
RODRIGO NERES LOMPA, em 20/08/2026 09:13:40

Confira a autenticidade com o código **miifRtOEZg**
no endereço https://portonacional.gep.digital/verificacao