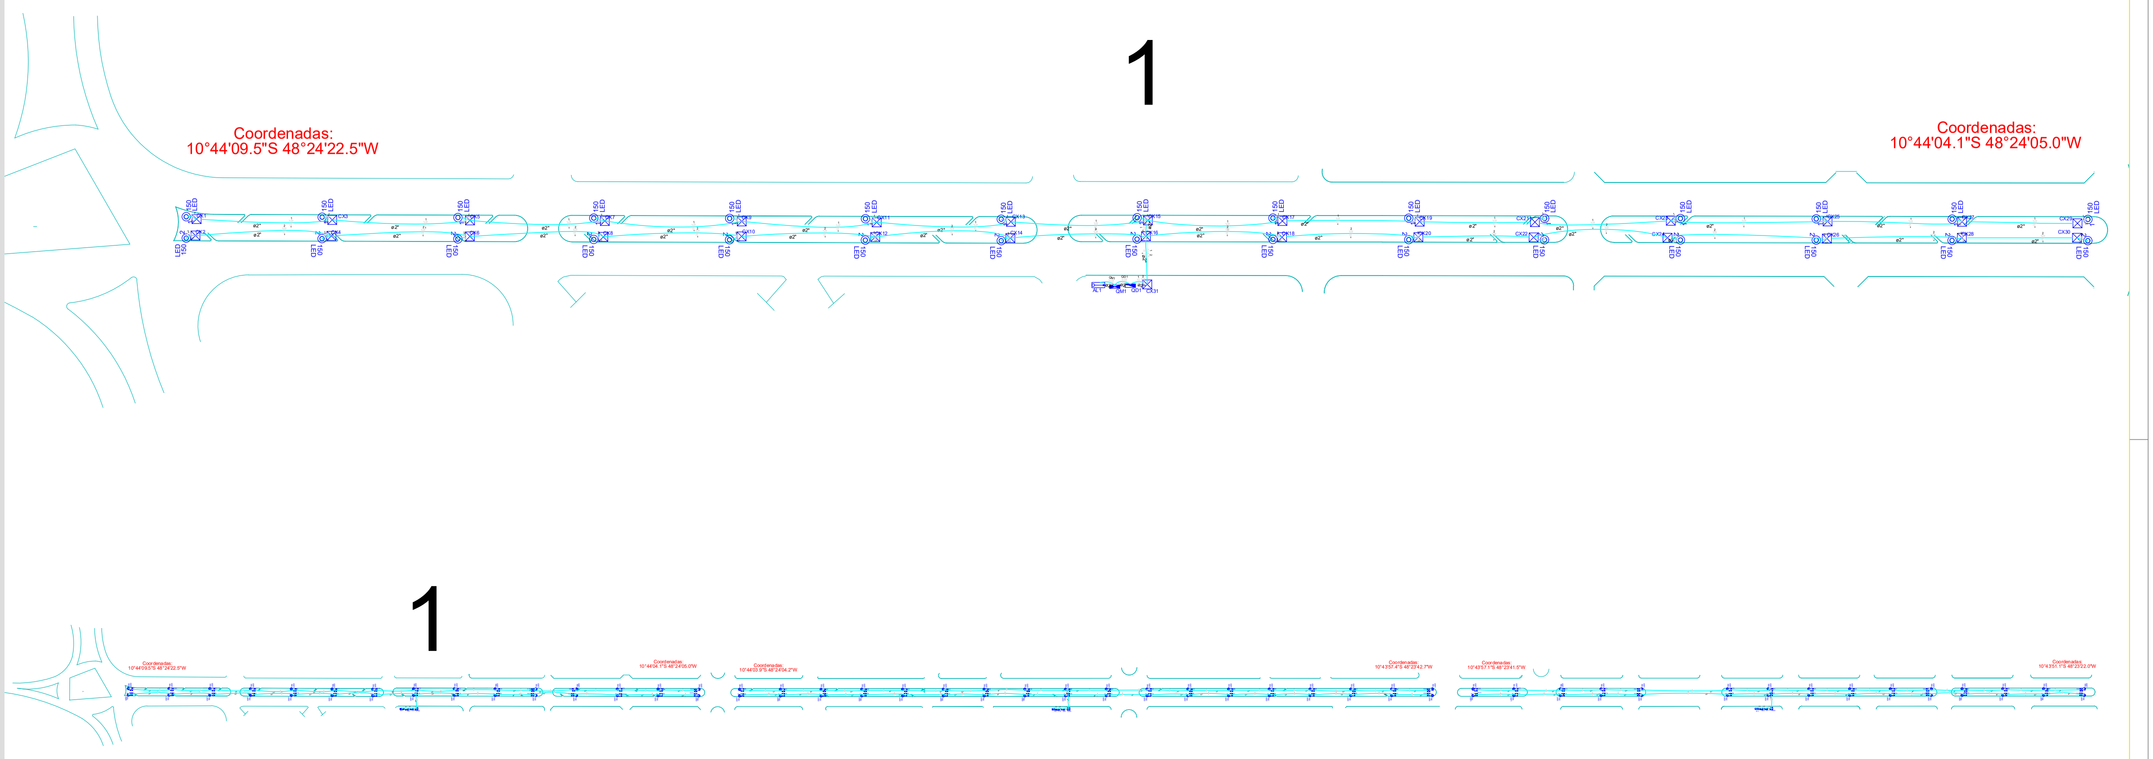

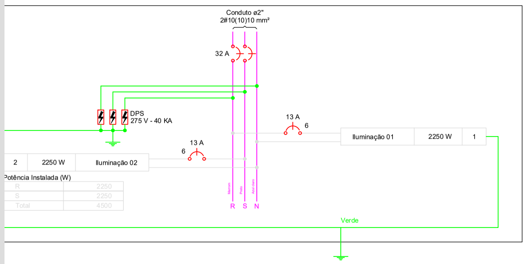

Quadro de Cargas (QD1)

Circuito	Descrição	Esquema	Método de inst.	V (V)	Iluminação (W) 150	Pot. total. (VA)	Pot. total. (W)	Fases	Pot. - R (W)	Pot. - S (W)	Pot. - T (W)	FCT	FCA	In' (A)	Seção (mm2)	Ic (A)	Disj (A)	dV parc (%)	dV total (%)	Status
1	Iluminação 01	F+N+T	D	220 V	15	2296	2250	R	2250			1.00	0.80	13.0	6	47.0	13.0	3.12	3.51	Ok
2	Iluminação 02	F+N+T	D	220 V	15	2296	2250	S		2250		1.00	0.80	13.0	6	47.0	13.0	2.97	3.36	Ok
TOTAL					30	4592	4500	R+S	2250	2250	0									

Lista de Materiais

Elétrica

Acessórios uso geral	
Fita isolante autofusão 20m	6 pç
Cabo Unipolar (cobre)	
Isol.PVC - 450/750V (ref. Pirelli Ecoplus BWF Flexível)	
10 mm²	271.30 m
6 mm²	8238.00 m
2,5 mm²	3909,80 m
Caixa de passagem - solo	
Alvenaria ou pré-moldado 400x400x400 mm	99 pç
Aterramento	
Haste de aterramento 2400mm x 3/4"	96 pç
Grampo p/ haste de aterramento Reforçado	96 pç
Dispositivo de Proteção	
Disjuntor Unipolar Termomagnético - norma DIN 13 A	6 pç
Disjuntor bipolar termomagnético (380 V/220 V) - DIN 32 A - 4.5 kA	3 pç
Dispositivo de proteção contra surto 275 V - 40 KA	15 pç
Dispositivo de Comando	
Contator Tripolar 12 A	3 pç
Relé fotoelétrico 4 pinos 1000 W	3 pç
Base p/ Relé fotoelétrico 4 pinos	3 pç
Eletroduto PVC flexível	
Eletroduto leve 3/4"	1287.30 m
Eletroduto pesado 2"	4157.60 m
Lâmpada LED	
Luminária LED Iluminação Pública Luminária 150W	96 pç
Poste Ornamental Iluminação Pública	
Poste aço galvanizado com braço 3 metros Poste 10m	96 pç
Material p/ entrada serviço	
Padrão de energia bifásico	3 pç
Ramal de Entrada Fases, Neutro e Terra	10 mm²
Haste de aterramento aço/cobre D=3/4", comprimento 2,4 m	1 pç
Caixa inspeção aterramento 250x250x400 mm	1 pç
Caixa CMI-02	1 pç
Poste de Concreto duplo T 100 daN, L=7,0m	1 pç
Quadro distrib. chapa pintada - embutir	
Bifásico Cap. 12 disj. unip.	3 pç

Legenda

⧗	Caixa de medição embutir a 1,60m do piso
☒	Caixa de passagem de embutir no piso
⊸	Entrada de serviço aérea - Saída aérea
◎ 150 LED	Luminária 150W
◢	Quadro de distribuição - embutir a 1,50m do piso

BREVE DESCRITIVO DO EMPREENDIMENTO

Projeto elétrico iluminação pública do Anel Viáriol de Porto Nacional - TO

OBSERVAÇÃO

Sem observações.

DADOS DO PROJETO:

Endereço: Avenida Francisco Dantas
Cidade / Setor: Porto Nacional -TO
Proprietário: Prefeitura Municipal de Porto Nacional - TO
Autor do Projeto: Rodrigo Neres Lompa
Resp. Técnico: Rodrigo Neres Lompa
Coordenadas Geográficas: Fuso: 22L
X: Latitude 784644 Y: Longitude 8812296

Prefeitura Municipal de Porto Nacional - TO
Proprietário:

Rodrigo Neres Lompa
Autor do Projeto
2418403335
Nº Crea:

RODRIGO NERES LOMPA:03398659110
Assinado de forma digital por RODRIGO NERES LOMPA:03398659110

Rodrigo Neres Lompa
Resp. Técnico:
2418403335
Nº Crea:

PROJETO ELETRICO
Nº DESENHO

PROJETO ELÉTRICO ILUMINAÇÃO PÚBLICA AVENIDA FRANCISCO DANTAS.
1/3

Projetista: Rodrigo Neres Lompa
Data Completa: 14/01/2026
Escala: DIVERSAS

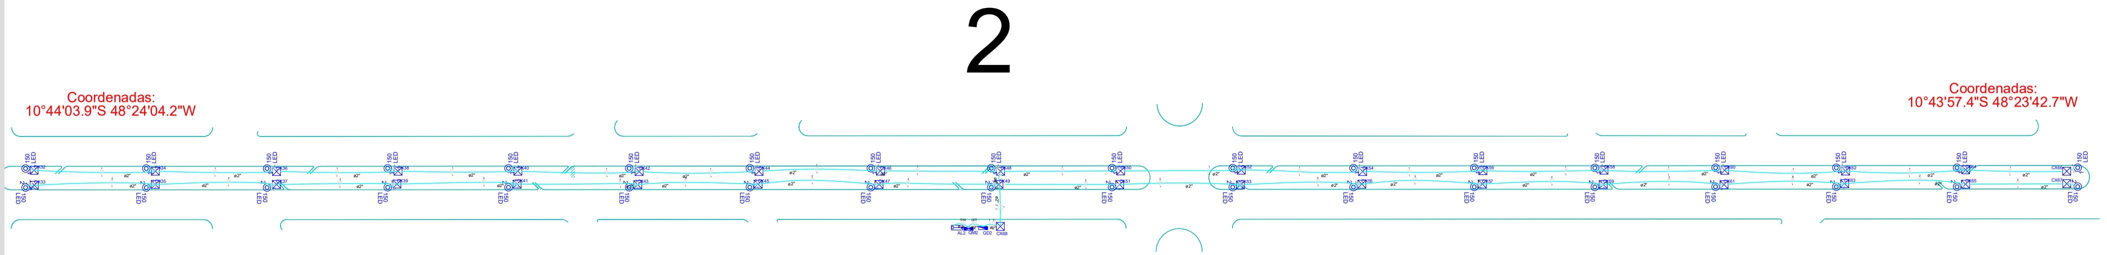

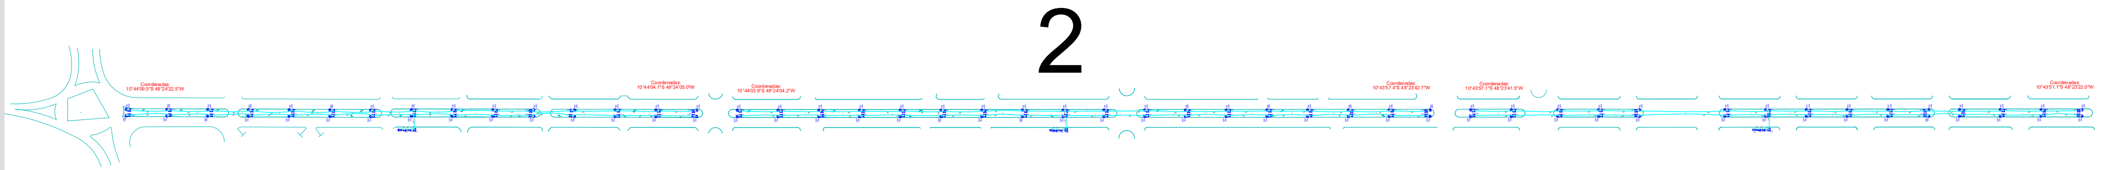
2
Coordenadas:
10°44'09.5"S 48°24'22.5"W
Coordenadas:
10°44'04.1"S 48°24'05.0"W
Coordenadas:
10°44'03.9"S 48°24'04.2"W
Coordenadas:
10°43'57.4"S 48°23'42.7"W
Coordenadas:
10°43'57.1"S 48°23'41.5"W
Coordenadas:
10°43'51.1"S 48°23'22.0"W

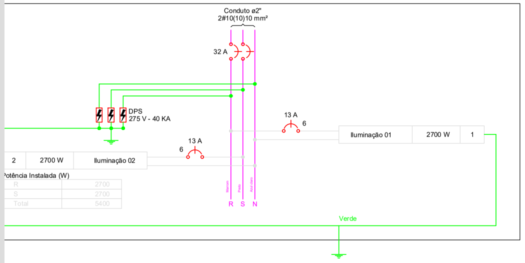

Quadro de Cargas (QD2)

Circuito	Descrição	Esquema	Método de inst.	V (V)	Iluminação (W) 150	Pot. total. (VA)	Pot. total. (W)	Fases	Pot. - R (W)	Pot. - S (W)	Pot. - T (W)	FCT	FCA	In' (A)	Seção (mm2)	Ic (A)	Disj (A)	dV parc (%)	dV total (%)	Status
1	Iluminação 01	F+N+T	D	220 V	18	2755	2700	R	2700			1.00	0.80	15.7	6	47.0	13.0	2.80	3.26	Ok
2	Iluminação 02	F+N+T	D	220 V	18	2755	2700	S		2700		1.00	0.80	15.7	6	47.0	13.0	2.71	3.16	Ok
TOTAL					36	5510	5400	R+S	2700	2700	0									

Lista de Materiais

Elétrica	
Acessórios uso geral	
Fita isolante autofusão 20m	6 pç
Cabo Unipolar (cobre)	
Isol.PVC - 450/750V (ref. Pirelli Ecoplus BWF Flexível)	
10 mm²	271.30 m
6 mm²	8238.00 m
2,5 mm²	3909,80 m
Caixa de passagem - solo	
Alvenaria ou pré-moldado 400x400x400 mm	99 pç
Aterramento	
Haste de aterramento 2400mm x 3/4"	96 pç
Grampo p/ haste de aterramento Reforçado	96 pç
Dispositivo de Proteção	
Disjuntor Unipolar Termomagnético - norma DIN 13 A	6 pç
Disjuntor bipolar termomagnético (380 V/220 V) - DIN 32 A - 4.5 kA	3 pç
Dispositivo de proteção contra surto 275 V - 40 KA	15 pç
Dispositivo de Comando	
Contator Tripolar 12 A	3 pç
Relé fotoelétrico 4 pinos 1000 W	3 pç
Base p/ Relé fotoelétrico 4 pinos	3 pç
Eletroduto PVC flexível	
Eletroduto leve 3/4"	1287.30 m
Eletroduto pesado 2"	4157.60 m
Lâmpada LED	
Luminária LED Iluminação Pública Luminária 150W	96 pç
Poste Ornamental Iluminação Pública	
Poste aço galvanizado com braço 3 metros Poste 10m	96 pç
Material p/ entrada serviço	
Padrão de energia bifásico	3 pç
Ramal de Entrada Fases, Neutro e Terra	10 mm²
Haste de aterramento aço/cobre D=3/4", comprimento 2,4 m	1 pç
Caixa inspeção aterramento 250x250x400 mm	1 pç
Caixa CMI-02	1 pç
Poste de Concreto duplo T 100 daN, L=7,0m	1 pç
Quadro distrib. chapa pintada - embutir	
Bifásico Cap. 12 disj. unip.	3 pç

Legenda

◪	Caixa de medição embutir a 1,60m do piso
☒	Caixa de passagem de embutir no piso
⊸	Entrada de serviço aérea - Saída aérea
◎ 1 150 LED	Luminária 150W
◩	Quadro de distribuição - embutir a 1,50m do piso

BREVE DESCRITIVO DO EMPREENDIMENTO

Projeto elétrico iluminação pública do Anel Viáriol de Porto Nacional - TO

OBSERVAÇÃO

Sem observações.

DADOS DO PROJETO:

Endereço: Avenida Francisco Dantas
Cidade / Setor: Porto Nacional -TO
Proprietário: Prefeitura Municipal de Porto Nacional - TO
Autor do Projeto: Rodrigo Neres Lompa
Resp. Técnico: Rodrigo Neres Lompa
Coordenadas Geográficas: Fuso: 22L
X: Latitude 784646
Y: Longitude 8812304

Prefeitura Municipal de Porto Nacional - TO
Proprietário:

Rodrigo Neres Lompa
Autor do Projeto
2418403335
Nº Crea:

RODRIGO NERES LOMPA:03398659110
Assinado de forma digital por RODRIGO NERES LOMPA:03398659110

Rodrigo Neres Lompa
Resp. Técnico:
2418403335
Nº Crea:

PROJETO ELETRICO

Nº DESENHO

PROJETO ELÉTRICO ILUMINAÇÃO PÚBLICA AVENIDA FRANCISCO DANTAS.

2/3

Projetista: Rodrigo Neres Lompa
Data Completa: 14/01/2026
Escala: DIVERSAS

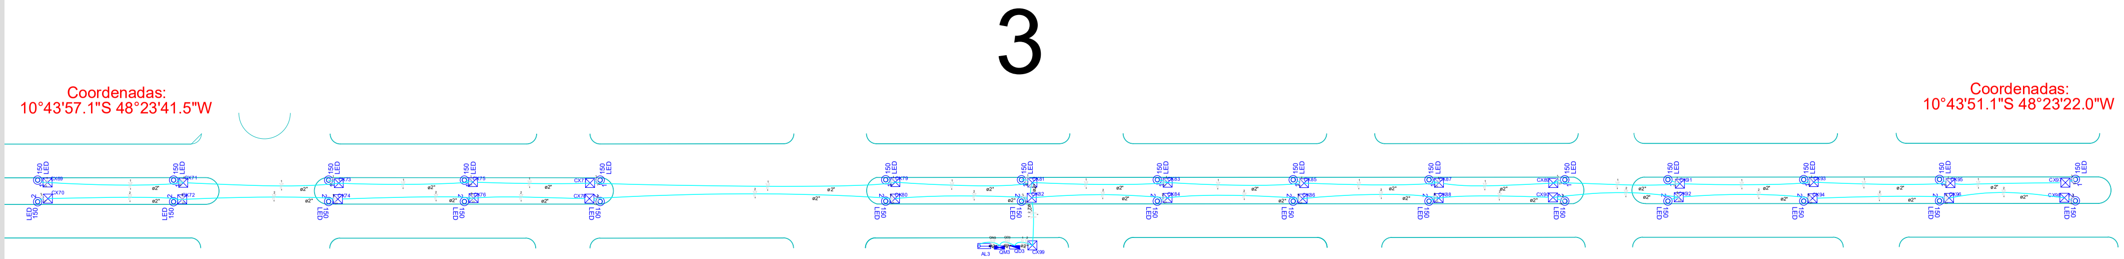

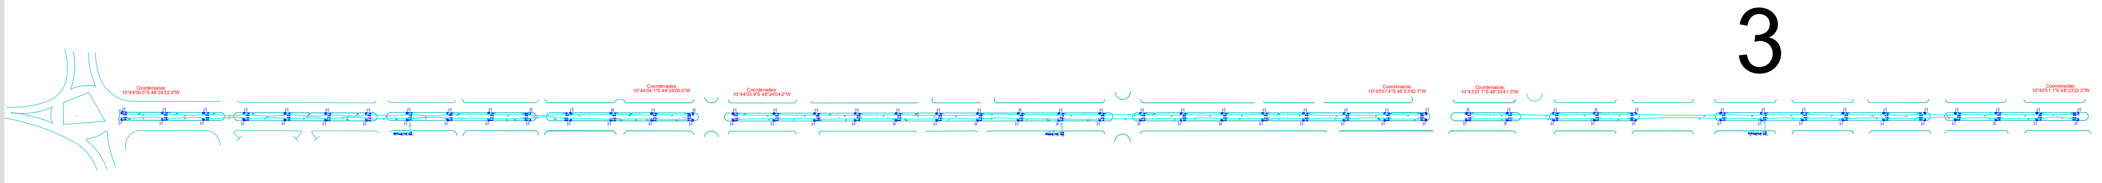
3
Coordenadas:
10°44'09.5"S 48°24'22.5"W
Coordenadas:
10°44'04.1"S 48°24'05.0"W
Coordenadas:
10°44'03.9"S 48°24'04.2"W
Coordenadas:
10°43'57.4"S 48°23'42.7"W
Coordenadas:
10°43'57.1"S 48°23'41.5"W
Coordenadas:
10°43'51.1"S 48°23'22.0"W

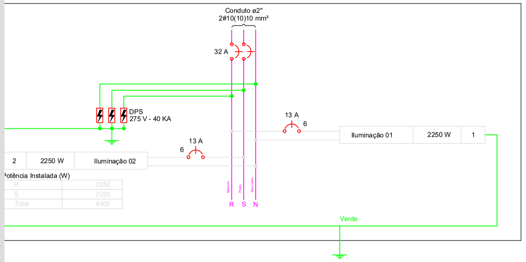

Quadro de Cargas (QD3)

Circuito	Descrição	Esquema	Método de inst.	V (V)	Iluminação (W) 150	Pot. total. (VA)	Pot. total. (W)	Fases	Pot. - R (W)	Pot. - S (W)	Pot. - T (W)	FCT	FCA	In' (A)	Seção (mm2)	Ic (A)	Disj (A)	dV parc (%)	dV total (%)	Status
1	Iluminação 01	F+N+T	D	220 V	15	2296	2250	R	2250			1.00	0.80	13.0	6	47.0	13.0	3.67	4.05	Ok
2	Iluminação 02	F+N+T	D	220 V	15	2296	2250	S		2250		1.00	0.80	13.0	6	47.0	13.0	3.53	3.91	Ok
TOTAL					30	4592	4500	R+S	2250	2250	0									

Lista de Materiais

Elétrica	**Acessórios uso geral**	
	Fita isolante autofusão 20m	6 pç
	Cabo Unipolar (cobre)	
	Isol.PVC - 450/750V (ref. Pirelli Ecoplus BWF Flexível)	
	10 mm²	271.30 m
	6 mm²	8238.00 m
	2,5 mm²	3909,80 m
	Caixa de passagem - solo	
	Alvenaria ou pré-moldado 400x400x400 mm	99 pç
	Aterramento	
	Haste de aterramento 2400mm x 3/4"	96 pç
	Grampo p/ haste de aterramento Reforçado	96 pç
	Dispositivo de Proteção	
	Disjuntor Unipolar Termomagnético - norma DIN 13 A	6 pç
	Disjuntor bipolar termomagnético (380 V/220 V) - DIN 32 A - 4.5 kA	3 pç
	Dispositivo de proteção contra surto 275 V - 40 KA	15 pç
	Dispositivo de Comando	
	Contator Tripolar 12 A	3 pç
	Relé fotoelétrico 4 pinos 1000 W	3 pç
	Base p/ Relé fotoelétrico 4 pinos	3 pç
	Eletroduto PVC flexível	
	Eletroduto leve 3/4"	1287.30 m
	Eletroduto pesado 2"	4157.60 m
	Lâmpada LED	
	Luminária LED Iluminação Pública Luminária 150W	96 pç
	Poste Ornamental Iluminação Pública	
	Poste aço galvanizado com braço 3 metros Poste 10m	96 pç
	Material p/ entrada serviço	
	Padrão de energia bifásico	3 pç
	Ramal de Entrada Fases, Neutro e Terra	10 mm²
	Haste de aterramento aço/cobre D=3/4'', comprimento 2,4 m	1 pç
	Caixa inspeção aterramento 250x250x400 mm	1 pç
	Caixa CMI-02	1 pç
	Poste de Concreto duplo T 100 daN, L=7,0m	1 pç
	Quadro distrib. chapa pintada - embutir	
	Bifásico Cap. 12 disj. unip.	3 pç

Legenda

⧗	Caixa de medição embutir a 1,60m do piso
☒	Caixa de passagem de embutir no piso
⊸	Entrada de serviço aérea - Saída aérea
1 ◎ 150 LED	Luminária 150W
◢	Quadro de distribuição - embutir a 1,50m do piso

BREVE DESCRITIVO DO EMPREENDIMENTO

Projeto elétrico iluminação pública do Anel Viáriol de Porto Nacional - TO

OBSERVAÇÃO

Sem observações.

DADOS DO PROJETO:

Endereço: Avenida Francisco Dantas
Cidade / Setor: Porto Nacional -TO
Proprietário: Prefeitura Municipal de Porto Nacional - TO
Autor do Projeto: Rodrigo Neres Lompa
Resp. Técnico: Rodrigo Neres Lompa
Coordenadas Geográficas: Fuso: 22L
X: Latitude 784646
Y: Longitude 8812304

Prefeitura Municipal de Porto Nacional - TO
Proprietário:

RODRIGO NERES LOMPA:03398659110 Assinado de forma digital por RODRIGO NERES LOMPA:03398659110

Rodrigo Neres Lompa
Autor do Projeto
2418403335
Nº Crea:

Rodrigo Neres Lompa
Resp. Técnico:
2418403335
Nº Crea:

PROJETO ELETRICO
Nº DESENHO

PROJETO ELÉTRICO ILUMINAÇÃO PÚBLICA AVENIDA FRANCISCO DANTAS.

3/3

Projetista: Rodrigo Neres Lompa
Data Completa: 14/01/2026
Escala: DIVERSAS

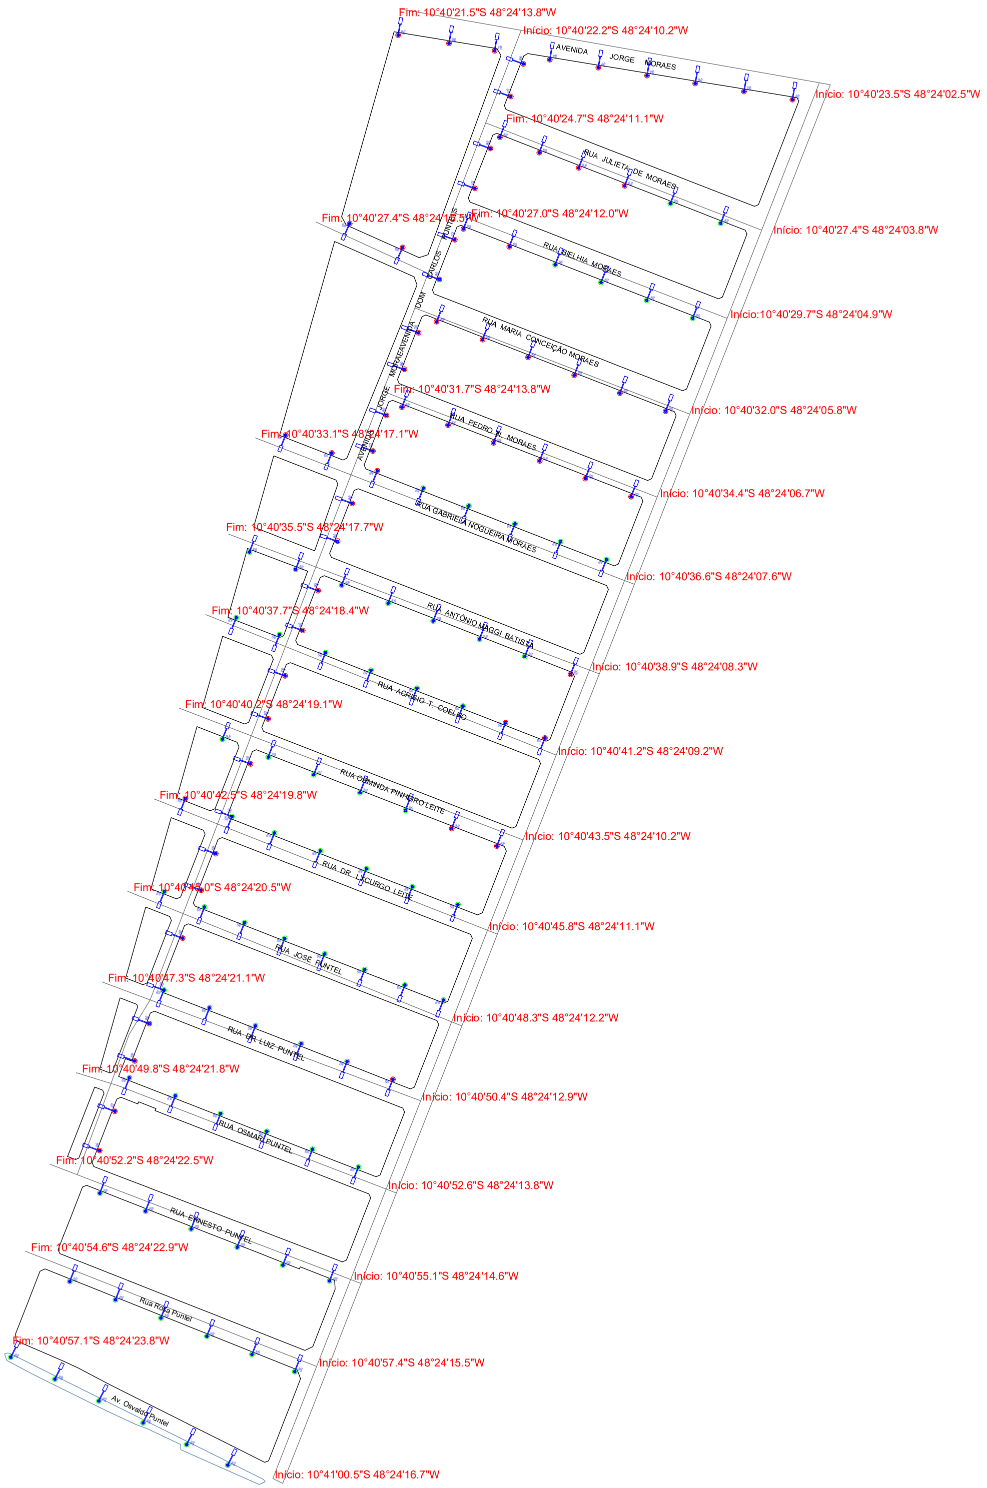
Fim: 10°40'21.5"S 48°24'13.8"W
Início: 10°40'22.2"S 48°24'10.2"W
AVENIDA JORGE MORAES
Início: 10°40'23.5"S 48°24'02.5"W
Fim: 10°40'24.7"S 48°24'11.1"W
RUA JULIETA DE MORAES
Fim: 10°40'27.4"S 48°24'16.5"W
Fim: 10°40'27.0"S 48°24'12.0"W
Início: 10°40'27.4"S 48°24'03.8"W
DOM CARLOS
RUA DELHIA MORAES
Início:10°40'29.7"S 48°24'04.9"W
RUA MARIA CONCEIÇÃO MORAES
AVENIDA JORGE MORAES
Fim: 10°40'31.7"S 48°24'13.8"W
RUA PEDRO L. MORAES
Início: 10°40'32.0"S 48°24'05.8"W
Fim: 10°40'33.1"S 48°24'17.1"W
RUA GABRIELA NOGUEIRA MORAES
Início: 10°40'34.4"S 48°24'06.7"W
Fim: 10°40'35.5"S 48°24'17.7"W
Início: 10°40'36.6"S 48°24'07.6"W
Fim: 10°40'37.7"S 48°24'18.4"W
RUA ANTÔNIO MAGGI BATISTA
Início: 10°40'38.9"S 48°24'08.3"W
Fim: 10°40'40.2"S 48°24'19.1"W
RUA ACRISIO T. COELHO
Início: 10°40'41.2"S 48°24'09.2"W
Fim: 10°40'42.5"S 48°24'19.8"W
RUA OLMINDA PINHEIRO LEITE
Início: 10°40'43.5"S 48°24'10.2"W
Fim: 10°40'45.0"S 48°24'20.5"W
RUA DR. LICURGO LEITE
Início: 10°40'45.8"S 48°24'11.1"W
RUA JOSE PUNTEL
Fim: 10°40'47.3"S 48°24'21.1"W
Início: 10°40'48.3"S 48°24'12.2"W
RUA DR. LUIZ PUNTEL
Fim: 10°40'49.8"S 48°24'21.8"W
Início: 10°40'50.4"S 48°24'12.9"W
RUA OSMAR PUNTEL
Fim: 10°40'52.2"S 48°24'22.5"W
Início: 10°40'52.6"S 48°24'13.8"W
RUA ERNESTO PUNTEL
Fim: 10°40'54.6"S 48°24'22.9"W
Início: 10°40'55.1"S 48°24'14.6"W
Rua Rosa Puntel
Fim: 10°40'57.1"S 48°24'23.8"W
Início: 10°40'57.4"S 48°24'15.5"W
Av. Osvaldo Puntel
Início: 10°41'00.5"S 48°24'16.7"W

Lista de Materiais

Elétrica	Acessórios uso geral	
	Fita isolante autofusão 20m	3 pç
	Cabo Unipolar (cobre)	
	Isol.HEPR - ench.XLPE - 0,6/1kV 2.5 mm²	605.00 m
	Cabo Duplex (alumínio)	
	Alumínio 0,6/1kV 10 mm²	1702.00 m
	Braço iluminação pública	
	Aço galvanizado 1.5 metros	65 pç
	Luminária Iluminação pública	
	LED 100W	149 pç
	Poste de Concreto	
	Poste Duplo T - DT 10.00 metros	63 pç
	Dispositivo de Iluminação	
	Relé fotoelétrico 1000W, 220V	142 pç
	Base p/ relé	142 pç
	Dispositivos Eletricos	
	Conector Perfurante 10mm-95mm	298 pç

Lista de Materiais

	Cabo Duplex 10mm²
○	Poste Inexistente
○	Poste Existente

DADOS DO PROJETO:

Endereço: Setor Guaxupé

Cidade / Setor: Porto Nacional / Guaxupé

Proprietário: Secretaria Municipal de Infraestrutura e Desenvolvivento Urbano

Autor do Projeto: Rodrigo Neres Lompa

Resp. Técnico: Engenheiro Eletricista Rodrigo Neres Lompa

Coordenadas Geográficas (UTM): FUSO: 22L
784082 Y: 8818553

RODRIGO NERES LOMPA:03398659110 Assinado de forma digital por RODRIGO NERES LOMPA:03398659110
Resp. Técnico:
2418403335
Nº Crea:

LEVANTAMENTO ILUMINAÇÃO GUAXUPÉ | PRANCHA

LEVANTAMENTO ILUMINAÇÃO GUAXUPÉ | 1/1

Projetista: Rodrigo Neres Lompa | Data Completa: 14/01/2026 | Escala: DIVERSAS

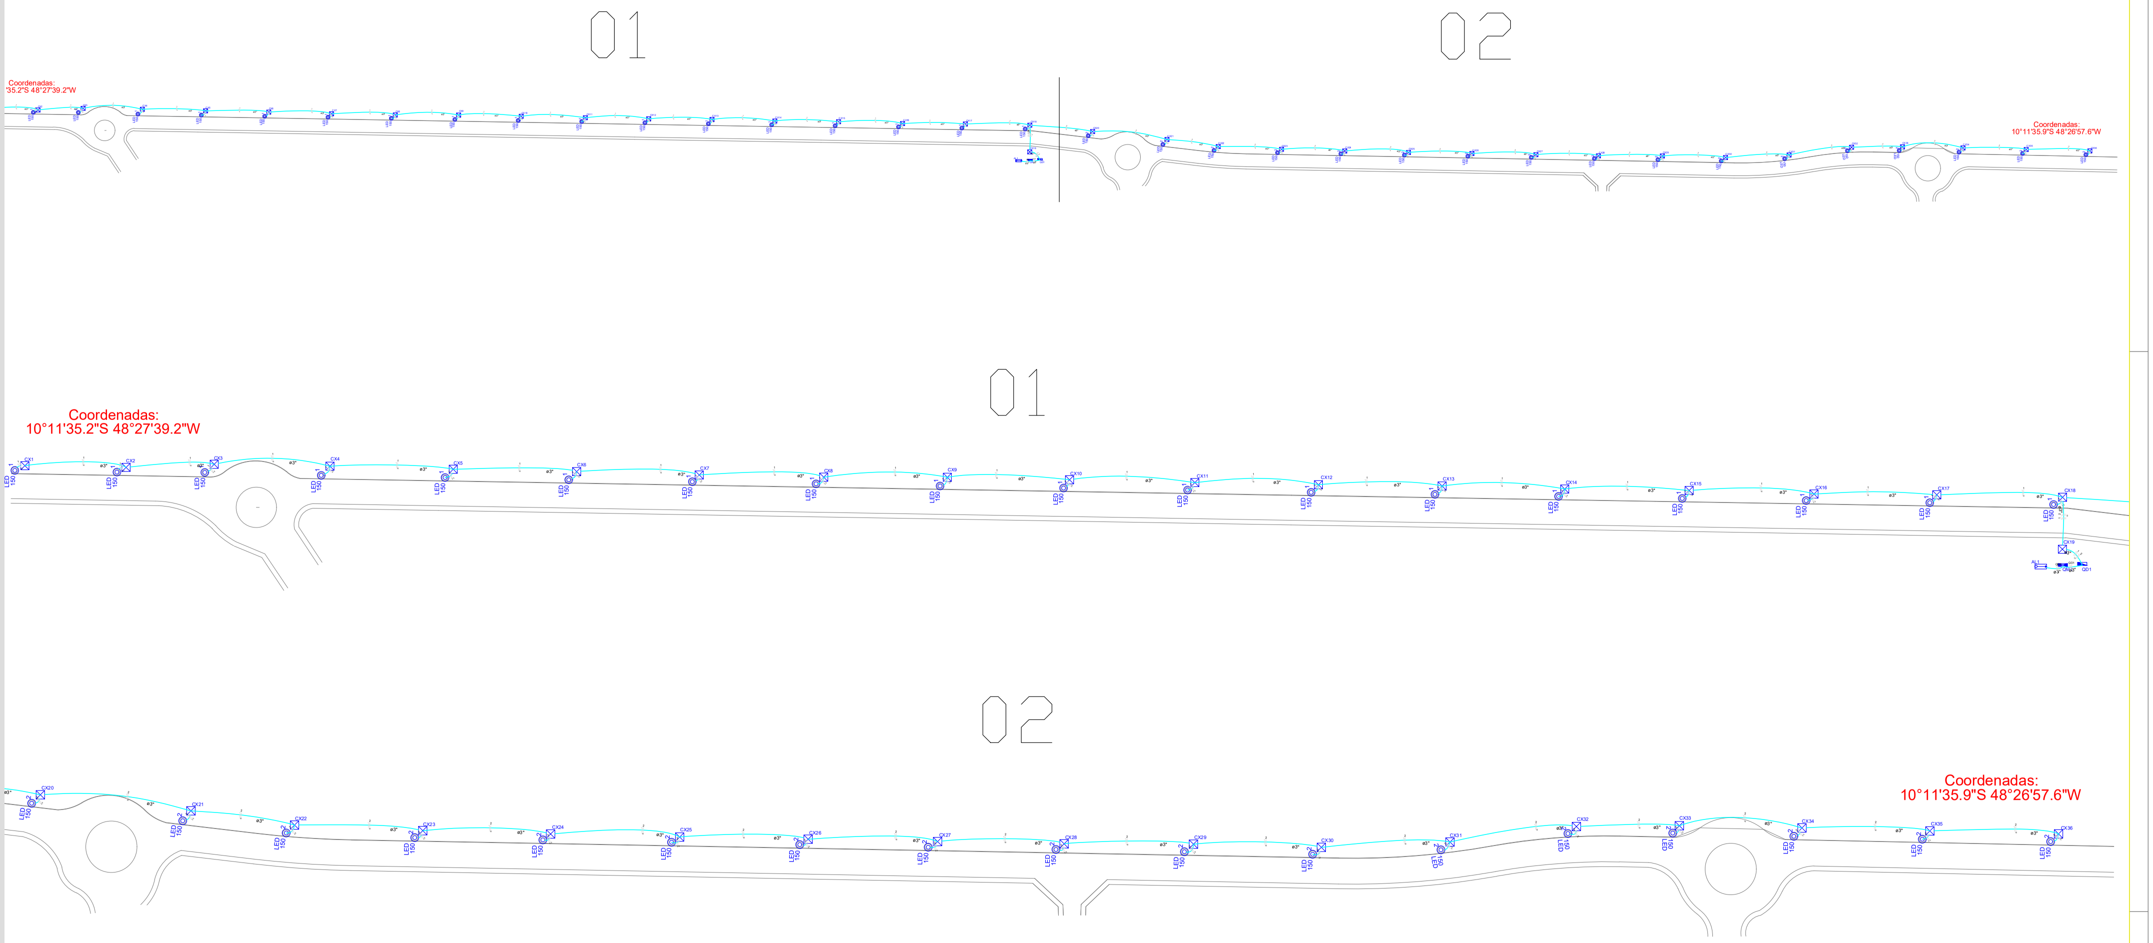

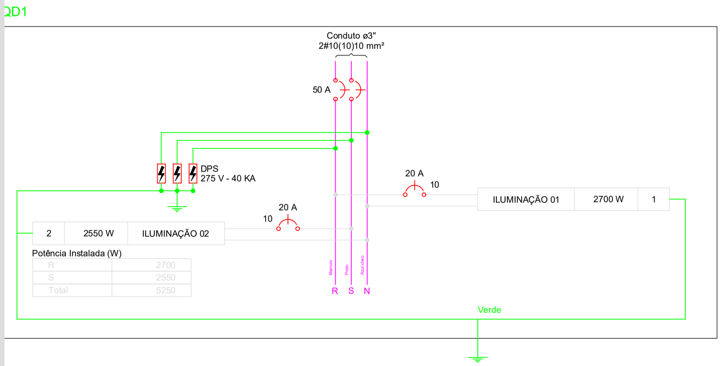

Lista de Materiais

Elétrica

Acessórios uso geral	
Fita isolante autofusão 20m	1 pç
Cabo Unipolar (cobre)	
Isol.PVC - 450/750V (ref. Pirelli Piras Ecoplus Flexíve) 2,5 mm²	1473.70 m
Isol.PVC - 450/750V (ref. Pirelli Piras Ecoplus Flexível) 10 mm²	3078.90 m
Caixa de passagem - embutir	
Aço pintada (ref Brum) 400x400x150 mm	36 pç
Aterramento	
Haste de aterramento 2400mm x 3/4"	35 pç
Grampo p/ haste de aterramento Reforçado	35 pç
Dispositivo de Proteção	
Disjuntor Unipolar Termomagnético - norma DIN 20 A	2 pç
Disjuntor bipolar termomagnético - norma DIN 50 A	1 pç
Dispositivo de proteção contra surto 275 V - 40 KA	3 pç
Dispositivo de Comando	
Contator Tripolar 12 A	1 pç
Relé fotoelétrico 4 pinos 1000 W	1 pç
Base p/ Relé fotoelétrico 4 pinos	1 pç
Eletroduto PVC flexível	
Eletroduto leve 3/4"	484.40 m
Eletroduto pesado 3"	1518.00 m
Lâmpada LED	
Luminária LED Iluminação Pública Luminária 150W	35 pç
Poste Ornamental Iluminação Pública	
Poste aço galvanizado com braço 3 metros Poste 10m	35 pç
Material p/ entrada serviço	
Padrão de energia bifásico	1 pç
Ramal de Entrada Fases, Neutro e Terra	10 mm²
Haste de aterramento aço/cobre D=3/4", comprimento 2,4 m	1 pç
Caixa inspeção aterramento 250x250x400 mm	1 pç
Caixa CMI-02	1 pç
Poste de Concreto duplo T 100 daN, L=7,0m	1 pç
Quadro distrib. chapa pintada - embutir	
Bifásico Cap. 24 disj. unip.	1 pç

Quadro de Cargas (QD1)

Circuito	Descrição	Esquema	Método de inst.	V (V)	Iluminação (W) 150	Pot. total. (VA)	Pot. total. (W)	Fases	Pot. - R (W)	Pot. - S (W)	Pot. - T (W)	FCT	FCA	In' (A)	Seção (mm2)	Ic (A)	Disj (A)	dV parc (%)	dV total (%)	Status
1	ILUMINAÇÃO 01	F+N+T	D	220 V	18	2755	2700	R	2700			1.00	0.80	15.7	10	63.0	20.0	3.27	3.82	Ok
2	ILUMINAÇÃO 02	F+N+T	D	220 V	17	2602	2550	S		2550		1.00	0.80	14.8	10	63.0	20.0	3.25	3.81	Ok
TOTAL					35	5357	5250	R+S	2700	2550	0									

Legenda

⧗	Caixa de medição embutir a 1,60m do piso
☒	Caixa de passagem de embutir no piso
⊸	Entrada de serviço aérea - Saída aérea
1 ◎ 150 LED	Luminária 150W
◢	Quadro de distribuição - embutir a 1,50m do piso

BREVE DESCRITIVO DO EMPREENDIMENTO

Projeto elétrico iluminação pública da Marginal Sul, Luzimangues, Porto Nacional - TO

OBSERVAÇÃO

Sem observações.

DADOS DO PROJETO:

Endereço: Marginal Sul
Cidade / Setor: Porto Nacional -TO/Luzimangues
Proprietário: Prefeitura Municipal de Porto Nacional - TO
Autor do Projeto: Rodrigo Neres Lompa
Resp. Técnico: Rodrigo Neres Lompa
Coordenadas Geográficas: Fuso: 22L
X: Latitude 777893 Y: Longitude 8872178

Prefeitura Municipal de Porto Nacional - TO
Proprietário:

Rodrigo Neres Lompa
Autor do Projeto
2418403335
Nº Crea:

RODRIGO NERES LOMPA:03398659110 Assinado de forma digital por RODRIGO NERES LOMPA:03398659110

Rodrigo Neres Lompa
Resp. Técnico:
2418403335
Nº Crea:

PROJETO ELETRICO
Nº DESENHO

PROJETO ELÉTRICO ILUMINAÇÃO PÚBLICA MARGINAL SUL.
1/2

Projetista: Rodrigo Neres Lompa
Data Completa: 14/01/2026
Escala: DIVERSAS

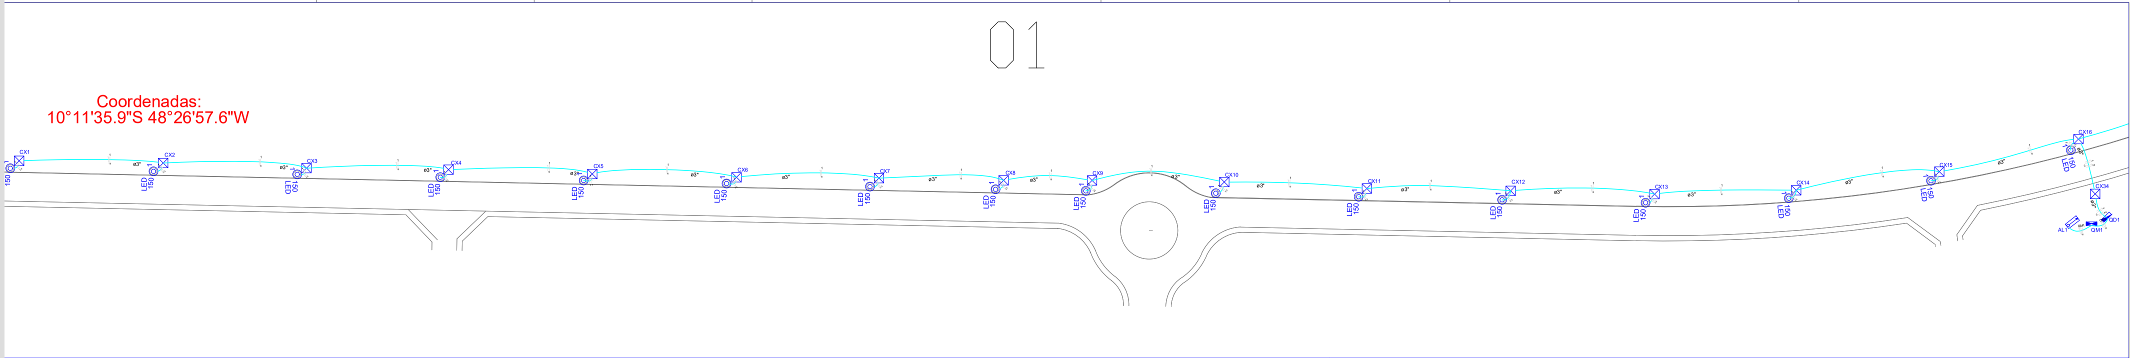

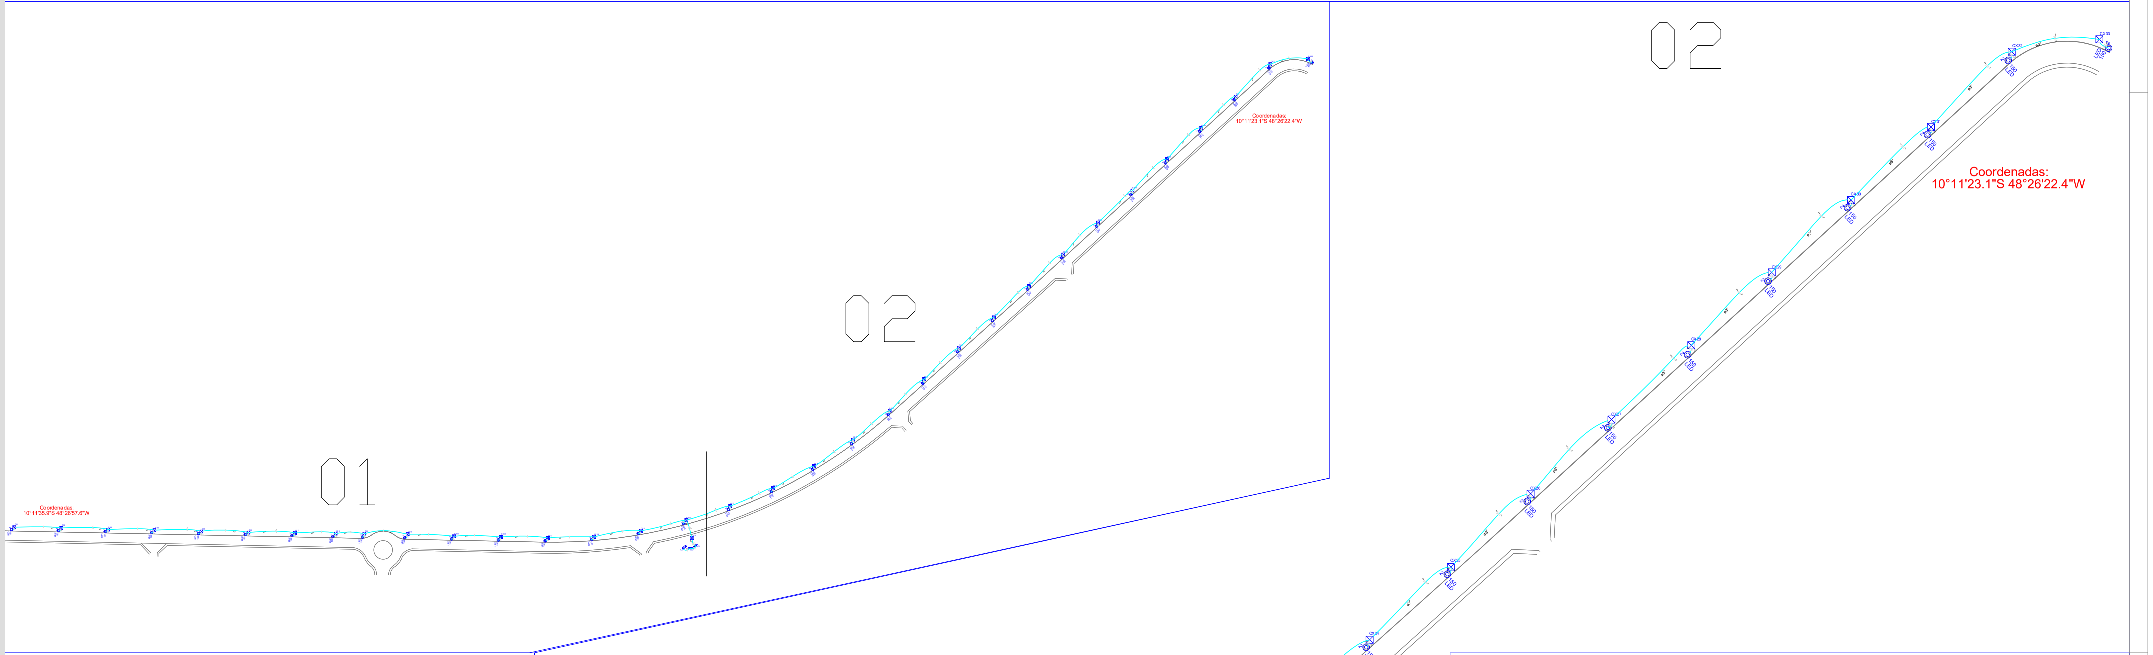

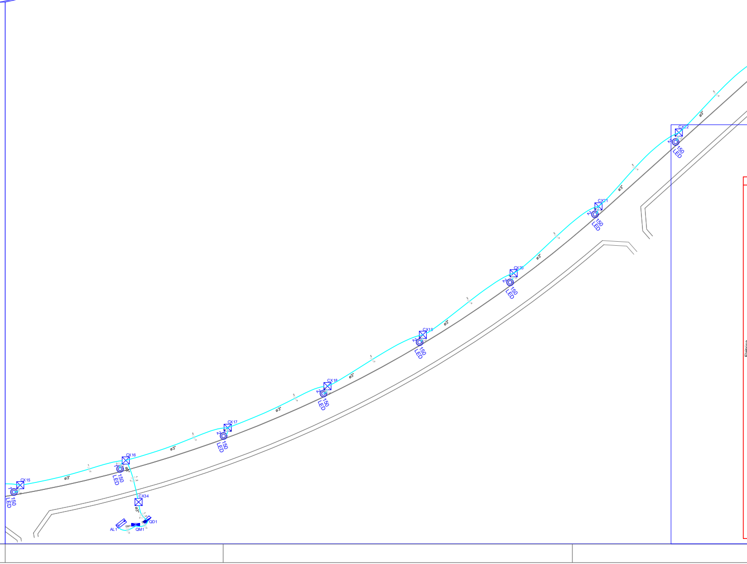

Quadro de Cargas (QD1)

Circuito	Descrição	Esquema	Método de inst.	V (V)	Iluminação (W) 150	Pot. total. (VA)	Pot. total. (W)	Fases	Pot. - R (W)	Pot. - S (W)	Pot. - T (W)	FCT	FCA	In' (A)	Seção (mm2)	Ic (A)	Disj (A)	dV parc (%)	dV total (%)	Status
1	ILUMINAÇÃO 01	F+N+T	D	220 V	16	2449	2400	R	2400			1.00	0.80	13.9	10	63.0	20.0	3.90	4.18	Ok
2	ILUMINAÇÃO 02	F+N+T	D	220 V	17	2602	2550	S		2550		1.00	0.80	14.8	10	63.0	20.0	3.25	3.53	Ok
TOTAL					33	5051	4950	R+S	2400	2550	0									

Lista de Materiais

Elétrica	Acessórios uso geral	
	Fita isolante autofusão 20m	1 pç
	Cabo Unipolar (cobre)	
	Isol.PVC - 450/750V (ref. Pirelli Piras Ecoplus Flexível)	
	2,5 mm²	1379.00 m
	10 mm²	2887.40 m
	16 mm²	62.90 m
	Caixa de passagem - embutir	
	Aço pintada (ref Brum) 400x400x150 mm	34 pç
	Aterramento	
	Haste de aterramento 2400mm x 3/4"	33 pç
	Grampo p/ haste de aterramento Reforçado	33 pç
	Dispositivo de Proteção	
	Disjuntor Unipolar Termomagnético - norma DIN 20 A	2 pç
	Disjuntor bipolar termomagnético - norma DIN 50 A	1 pç
	Dispositivo de proteção contra surto 275 V - 40 KA	3 pç
	Dispositivo de Comando	
	Contator Tripolar 12 A	1 pç
	Relé fotoelétrico 4 pinos 1000 W	1 pç
	Base p/ Relé fotoelétrico 4 pinos	1 pç
	Eletroduto PVC flexível	
	Eletroduto leve 3/4"	453.40 m
	Eletroduto pesado 3"	1424.00 m
	Lâmpada LED	
	Luminária LED Iluminação Pública Luminária 150W	33 pç
	Poste Ornamental Iluminação Pública	
	Poste aço galvanizado com braço 3 metros Poste 10m	33 pç
	Material p/ entrada serviço	
	Padrão de energia bifásico	1 pç
	Ramal de Entrada Fases, Neutro e Terra	10 mm²
	Haste de aterramento aço/cobre D=3/4", comprimento 2,4 m	1 pç
	Caixa inspeção aterramento 250x250x400 mm	1 pç
	Caixa CMI-02	1 pç
	Poste de Concreto duplo T 100 daN, L=7,0m	1 pç
	Quadro distrib. chapa pintada - embutir	
	Bifásico Cap. 24 disj. unip.	1 pç

Legenda

☒	Caixa de passagem de embutir no piso
⊸	Entrada de serviço aérea - Saída aérea
◎ 150 LED	Luminária 150W
◢	Quadro de distribuição - embutir a 1,50m do piso
⧗	Quadro de medição embutir a 1,50m do piso

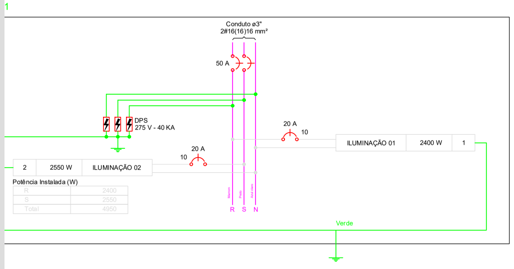

Potência Instalada (W)

R	2400
S	2550
Total	4950

BREVE DESCRITIVO DO EMPREENDIMENTO

Projeto elétrico iluminação pública da Marginal Sul, Luzimangues, Porto Nacional - TO

OBSERVAÇÃO

Sem observações.

DADOS DO PROJETO:

Endereço: Marginal Sul
Cidade / Setor: Porto Nacional -TO/Luzimangues
Proprietário: Prefeitura Municipal de Porto Nacional - TO
Autor do Projeto: Rodrigo Neres Lompa
Resp. Técnico: Rodrigo Neres Lompa
Coordenadas Geográficas: Fuso: 22L
X: Latitude 780054 Y: Longitude 8872137

Prefeitura Municipal de Porto Nacional - TO
Proprietário:

RODRIGO NERES LOMPA:03398659110 Assinado de forma digital por RODRIGO NERES LOMPA:03398659110

Rodrigo Neres Lompa
Autor do Projeto
2418403335
Nº Crea:

Rodrigo Neres Lompa
Resp. Técnico:
2418403335
Nº Crea:

PROJETO ELETRICO
Nº DESENHO

PROJETO ELÉTRICO ILUMINAÇÃO PÚBLICA MARGINAL SUL.
2/2

Projetista: Rodrigo Neres Lompa
Data Completa: 14/01/2026
Escala: DIVERSAS

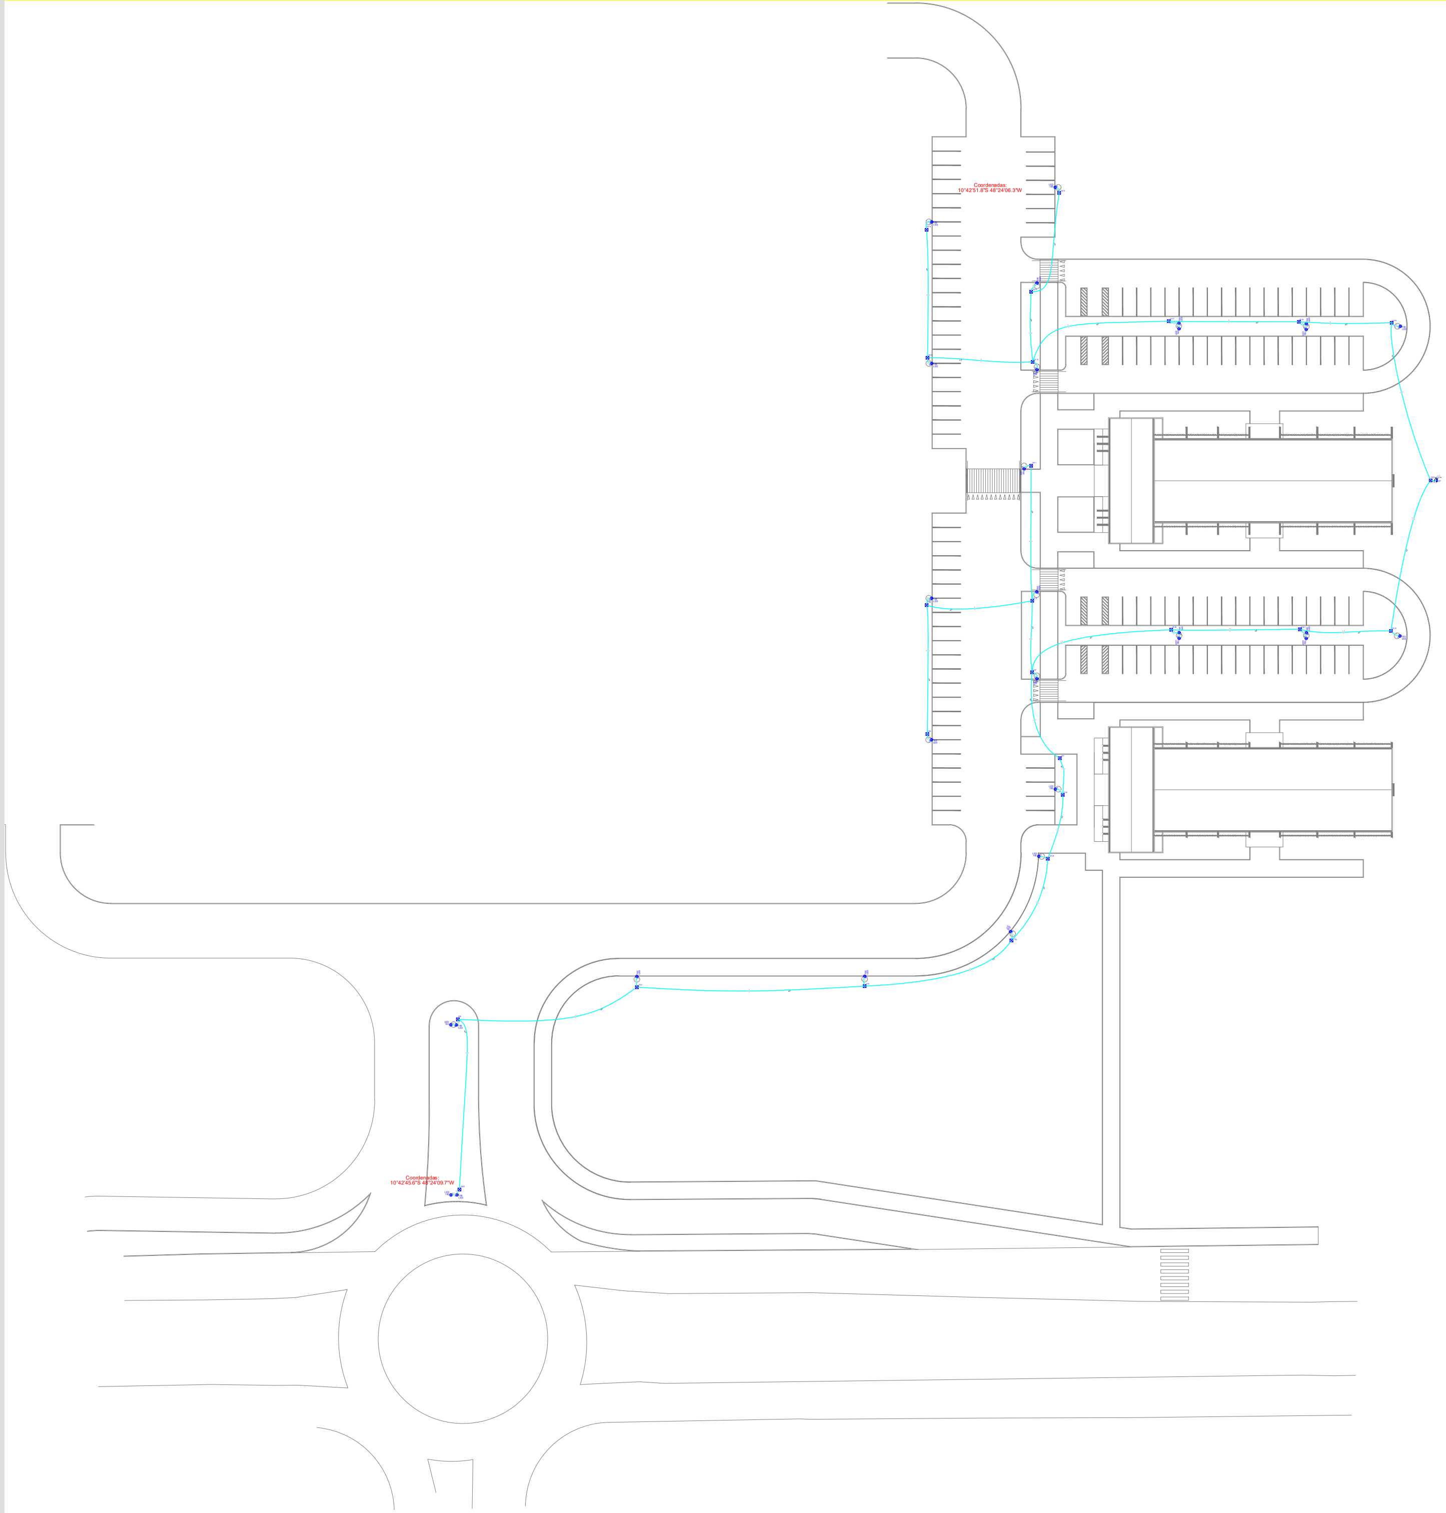

QD1

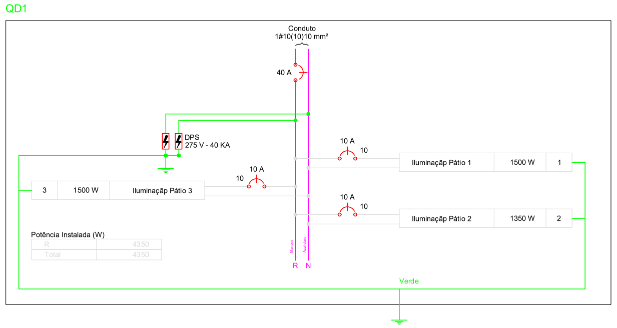

Quadro de Cargas (QD1)

Circuito	Descrição	Esquema	Método de inst.	V (V)	Iluminação (W) 150	Pot. total. (VA)	Pot. total. (W)	Fases	Pot. - R (W)	Pot. - S (W)	Pot. - T (W)	FCT	FCA	In' (A)	Seção (mm2)	Ic (A)	Disj (A)	dV parc (%)	dV total (%)	Status
1	Iluminaçãp Pátio 1	F+N+T	D	220 V	10	1531	1500	R	1500			1.00	0.70	9.9	10	63.0	10.0	2.39	2.39	Ok
2	Iluminaçãp Pátio 2	F+N+T	D	220 V	9	1378	1350	R	1350			1.00	0.70	8.9	10	63.0	10.0	0.94	0.94	Ok
3	Iluminaçãp Pátio 3	F+N+T	D	220 V	10	1531	1500	R	1500			1.00	0.70	9.9	10	63.0	10.0	1.01	1.01	Ok
TOTAL					29	4439	4350	R	4350	0	0									

Lista de Materiais

Elétrica	**Cabo Unipolar (cobre)**	
	Isol.PVC - 450/750V (ref. Pirelli Ecoplus BWF Flexível)	
	10 mm²	1020.00 m
	2.5 mm²	1149.80 m
	Caixa de passagem - solo	
	Alvenaria ou pré-moldado	
	400x400x400 mm	25 pç
	Aterramento	
	Haste de aterramento	
	2400mm x 3/4"	23 pç
	Grampo p/ haste de aterramento	
	Reforçado	23 pç
	Dispositivo de Proteção	
	Disjuntor Unipolar Termomagnético - norma DIN	
	10 A	3 pç
	Dispositivo de proteção contra surto	
	275 V - 40 KA	2 pç
	Dispositivo de Comando	
	Contator Tripolar	
	12 A	1 pç
	Relé fotoelétrico 4 pinos	
	1000 W	1 pç
	Base p/ Relé fotoelétrico	
	4 pinos	1 pç
	Eletroduto PVC flexível	
	Eletroduto leve	
	3/4"	254.80 m
	Eletroduto pesado	
	2"	568.10 m
	Lâmpada LED	
	Luminária LED Iluminação Pública	
	Luminária 150W	29 pç
	Poste Ornamental Iluminação Pública	
	Poste aço galvanizado com braço 3 metros	
	Poste 10m	17 pç
	Poste aço galvanizado com 2 braço 3 metros	
	Poste 10m	6 pç
	Quadro distrib. chapa pintada - embutir	
	Sem barr. - DIN (Ref. Cemar)	
	Cap. 12 disj. unip.	1 pç

Legenda

☒	Caixa de passagem de embutir no piso
1 ◎ 150 LED	Luminária 150W
▮	Quadro de distribuição - embutir a 1,50m do piso

BREVE DESCRITIVO DO EMPREENDIMENTO

Projeto elétrico iluminação pública do Anel Viáriol de Porto Nacional - TO

OBSERVAÇÃO

Sem observações.

DADOS DO PROJETO:

Endereço: Centro Administrativo, TO 050, Vila Militar, Aeroclube
Cidade / Setor: Porto Nacional -TO
Proprietário: Prefeitura Municipal de Porto Nacional - TO
Autor do Projeto: Rodrigo Neres Lompa
Resp. Técnico: Rodrigo Neres Lompa
Coordenadas Geográficas: Fuso: 22L
X: Latitude 784109 Y: Longitude 8814431

Prefeitura Municipal de Porto Nacional - TO
Proprietário:

Rodrigo Neres Lompa
Autor do Projeto
2418403335
Nº Crea:

Rodrigo Neres Lompa
Resp. Técnico:
2418403335
Nº Crea:

RODRIGO NERES LOMPA:03398659110
Assinado de forma digital por RODRIGO NERES LOMPA:03398659110

PROJETO ELETRICO

PROJETO ELÉTRICO ILUMINAÇÃO PÚBLICA CENTRO ADIMINISTRATIVO

Nº DESENHO
1/1

Projetista: Rodrigo Neres Lompa
Data Completa: 14/01/2026
Escala: DIVERSAS

Lista de Materiais

Elétrica	
Acessórios uso geral	
Fita isolante autofusão 20m	2 pç
Cabo Unipolar (cobre)	
Isol.PVC - 450/750V (ref. Pirelli Ecoplus BWF Flexível) 10 mm²	9602.62 m
Isol.PVC - 450/750V (ref. Pirelli Ecoplus BWF Flexível) 2.5 mm²	6023.07 m
Caixa de passagem - embutir	
Aço pintada (ref Brum) 400x400x150 mm	106 pç
Aterramento	
Haste de aterramento 2400mm x 3/4"	106 pç
Grampo p/ haste de aterramento Reforçado	106 pç
Dispositivo de Proteção	
Disjuntor Unipolar Termomagnético - norma DIN 16 A	8 pç
Disjuntor bipolar termomagnético (380 V/220 V) - DIN 32 A - 4.5 kA	2 pç
Dispositivo de proteção contra surto 275 V - 40 KA	6 pç
Eletroduto PVC flexível	
Eletroduto leve 3/4"	1956.00 m
Eletroduto pesado 2"	4677.70 m
Lâmpada LED	
Luminária LED Iluminação Pública Luminária 150W	106 pç
Poste Ornamental Iluminação Pública	
Poste aço galvanizado com 1 braço de 3 metros Poste 10m	106 pç
Material p/ entrada serviço	
Padrão de energia bifásico	1 pç
Ramal de Entrada Fases, Neutro e Terra	10 mm²
Haste de aterramento aço/cobre D=3/4", comprimento 2,4 m	1 pç
Caixa inspeção aterramento 250x250x400 mm	1 pç
Caixa CMI-02	1 pç
Poste de Concreto duplo T 100 daN, L=7,0m	1 pç
Quadro distrib. chapa pintada - embutir	
Bifásico Cap. 12 disj. unip.	2 pç

Legenda

▮	Caixa de medição embutir a 1,60m do piso
☒	Caixa de passagem de embutir no piso
⊶	Entrada de serviço aérea - Saída aérea
◎ 1 150 LED	Luminária 150W
◢	Quadro de distribuição - embutir a 1,50m do piso

Quadro de Cargas (QD1)

Circuito	Descrição	Esquema	Método de inst.	V (V)	Iluminação (W) 150	Pot. total. (VA)	Pot. total. (W)	Fases	Pot. - R (W)	Pot. - S (W)	Pot. - T (W)	FCT	FCA	In' (A)	Seção (mm2)	Ic (A)	Disj (A)	dV parc (%)	dV total (%)	Status
1	Iluminação 1	F+N+T	D	220 V	13	1990	1950	R	1950			1.00	0.65	13.9	10	63.0	16.0	3.05	3.92	Ok
2	Iluminação 2	F+N+T	D	220 V	13	1990	1950	S		1950		1.00	0.65	13.9	10	63.0	16.0	2.68	3.55	Ok
3	Iluminação 3	F+N+T	D	220 V	14	2143	2100	R	2100			1.00	0.65	15.0	10	63.0	16.0	3.93	4.81	Ok
4	Iluminação 4	F+N+T	D	220 V	13	1990	1950	S		1950		1.00	0.65	13.9	10	63.0	16.0	3.07	3.95	Ok
TOTAL					53	8112	7950	R+S	4050	3900	0									

Quadro de Cargas (QD2)

Circuito	Descrição	Esquema	Método de inst.	V (V)	Iluminação (W) 150	Pot. total. (VA)	Pot. total. (W)	Fases	Pot. - R (W)	Pot. - S (W)	Pot. - T (W)	FCT	FCA	In' (A)	Seção (mm2)	Ic (A)	Disj (A)	dV parc (%)	dV total (%)	Status
1	Iluminação 5	F+N+T	D	220 V	13	1990	1950	R	1950			1.00	0.65	13.9	10	63.0	16.0	3.01	3.95	Ok
2	Iluminação 6	F+N+T	D	220 V	13	1990	1950	S		1950		1.00	0.65	13.9	10	63.0	16.0	2.68	3.62	Ok
3	Iluminação 7	F+N+T	D	220 V	13	1990	1950	R	1950			1.00	0.65	13.9	10	63.0	16.0	3.41	4.35	Ok
4	Iluminação 8	F+N+T	D	220 V	14	2143	2100	S		2100		1.00	0.65	15.0	10	63.0	16.0	3.55	4.49	Ok
TOTAL					53	8112	7950	R+S	3900	4050	0									

QD1

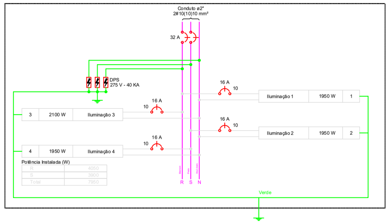

Potência Instalada (W)

R	4050
S	3900
Total	7950

QD2

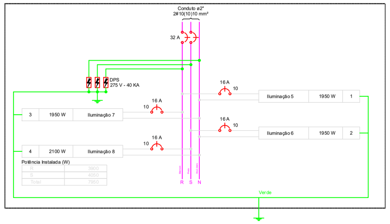

Potência Instalada (W)

R	3900
S	4050
Total	7950

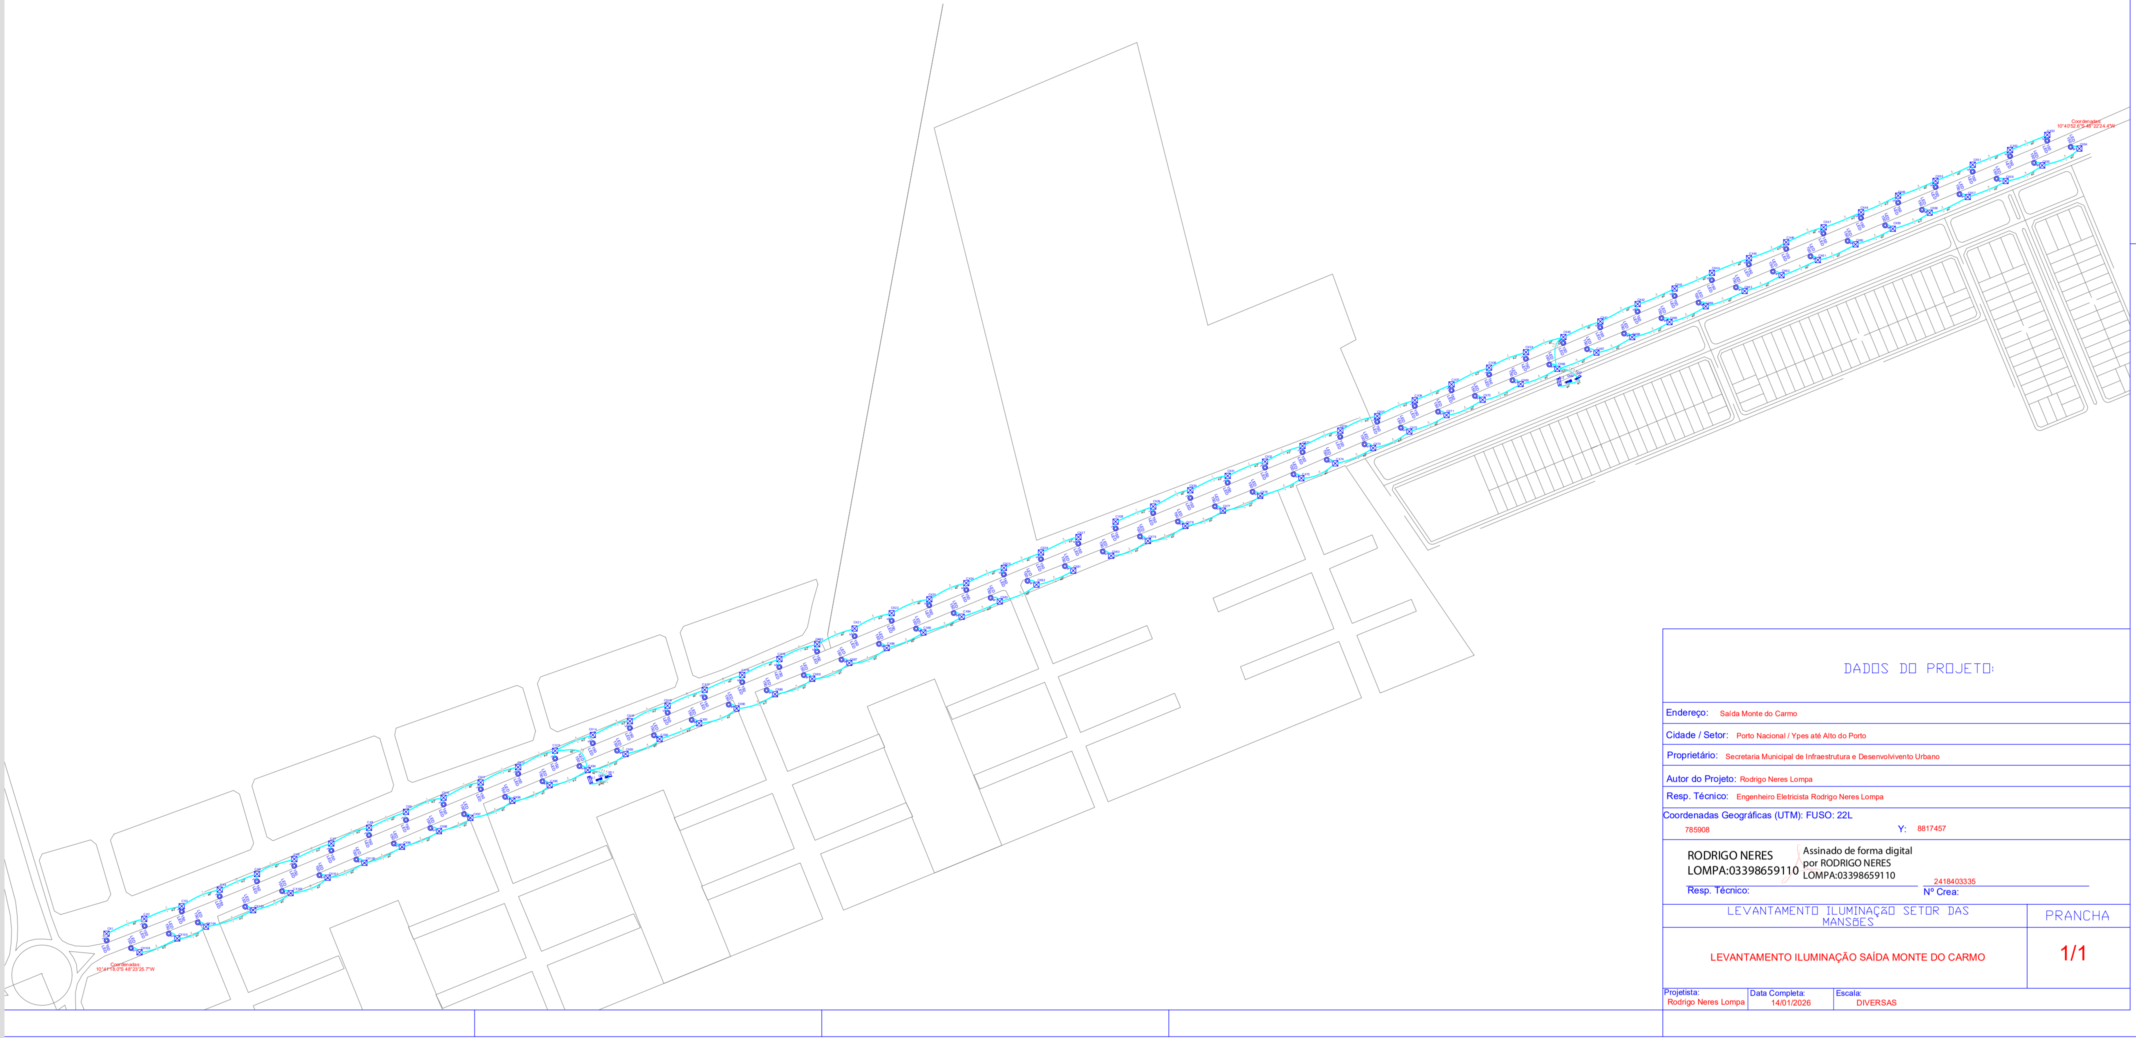

DADOS DO PROJETO:

Endereço: Saída Monte do Carmo

Cidade / Setor: Porto Nacional / Ypes até Alto do Porto

Proprietário: Secretaria Municipal de Infraestrutura e Desenvolvivento Urbano

Autor do Projeto: Rodrigo Neres Lompa

Resp. Técnico: Engenheiro Eletricista Rodrigo Neres Lompa

Coordenadas Geográficas (UTM): FUSO: 22L

785908 Y: 8817457

RODRIGO NERES LOMPA:03398659110 Assinado de forma digital por RODRIGO NERES LOMPA:03398659110

Resp. Técnico:

Nº Crea: 2418403335

LEVANTAMENTO ILUMINAÇÃO SETOR DAS MANSÕES

PRANCHA

LEVANTAMENTO ILUMINAÇÃO SAÍDA MONTE DO CARMO

1/1

Projetista: Rodrigo Neres Lompa

Data Completa: 14/01/2026

Escala: DIVERSAS

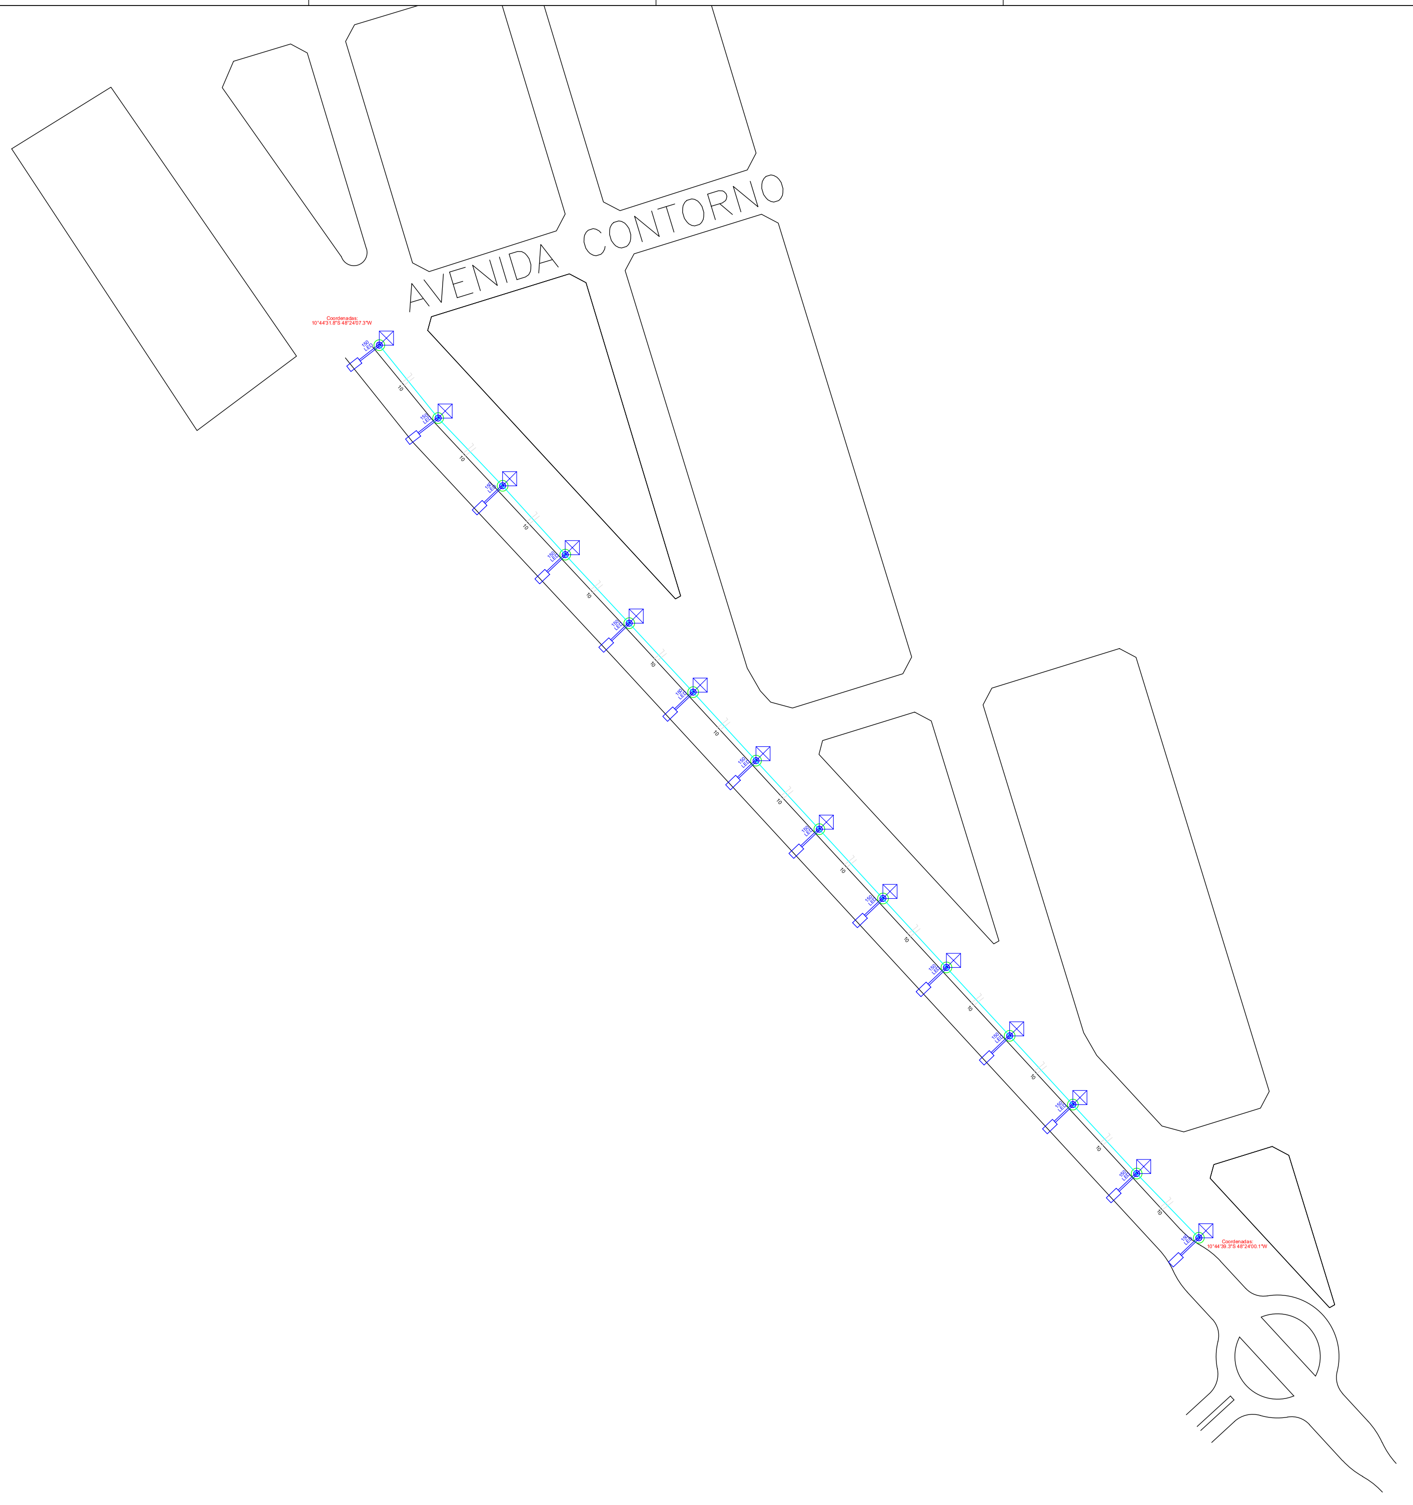

Legenda

☒	Caixa de passagem de embutir no piso
1 ◎ 150 LED	Luminária 150W
○	Poste Cônico Contínuo

Lista de Materiais

Elétrica	**Acessórios uso geral**	
	Fita isolante autofusão 20m	1 pç
	Cabo Unipolar (cobre)	
	Isol.PVC - 450/750V (ref. Pirelli Ecoplus BWF Flexível) 10 mm²	1176.00 m
	2,5 mm²	140.00 m
	Caixa de passagem - solo	
	Alvenaria ou pré-moldado 400x400x400 mm	14 pç
	Aterramento	
	Haste de aterramento 2400mm x 3/4"	14 pç
	Grampo p/ haste de aterramento Reforçado	14 pç
	Dispositivo de Proteção	
	Disjuntor Unipolar Termomagnético - norma DIN 20 A	1 pç
	Disjuntor Unipolar Termomagnético - norma DIN 50 A	1 pç
	Dispositivo de proteção contra surto 275 V - 40 KA	2 pç
	Dispositivo de Comando	
	Contator Tripolar 12 A	1 pç
	Relé fotoelétrico 4 pinos 1000 W	1 pç
	Base p/ Relé fotoelétrico 4 pinos	1 pç
	Eletroduto PVC flexível	
	Eletroduto pesado 2"	588.00 m
	Lâmpada LED	
	Luminária LED Iluminação Pública Luminária 150W	14 pç
	Poste Ornamental Iluminação Pública	
	Poste aço galvanizado com braço 3 metros Poste 10m	14 pç
	Material p/ entrada serviço	
	Padrão de energia monofásico	1 pç
	Ramal de Entrada Fases, Neutro e Terra	10 mm²
	Haste de aterramento aço/cobre D=3/4", comprimento 2,4 m	1 pç
	Caixa inspeção aterramento 250x250x400 mm	1 pç
	Caixa CMI-02	1 pç
	Poste de Concreto duplo T 100 daN, L=7,0m	1 pç
	Quadro distrib. chapa pintada - embutir	
	Bifásico Cap. 12 disj. unip.	1 pç

DADOS DO PROJETO:

Endereço: Saída Silvanópolis

Cidade / Setor: Porto Nacional / Imperial

Proprietário: Secretaria Municipal de Infraestrutura e Desenvolvivento Urbano

Autor do Projeto: Rodrigo Neres Lompa

Resp. Técnico: Engenheiro Eletricista Rodrigo Neres Lompa

Coordenadas Geográficas (UTM): FUSO: 22L
784244 Y: 8811207

RODRIGO NERES LOMPA:03398659110
Assinado de forma digital por RODRIGO NERES LOMPA:03398659110
Resp. Técnico:

2418403335
Nº Crea:

LEVANTAMENTO ILUMINAÇÃO SETOR DAS MANSÕES

PRANCHA

LEVANTAMENTO ILUMINAÇÃO SAÍDA SILVANÓPOLIS

1/1

Projetista: Rodrigo Neres Lompa
Data Completa: 14/01/2026
Escala: DIVERSAS

Lista de Materiais	
Conjunto de poste ornamental Solar 9 metros 90w	23 pç

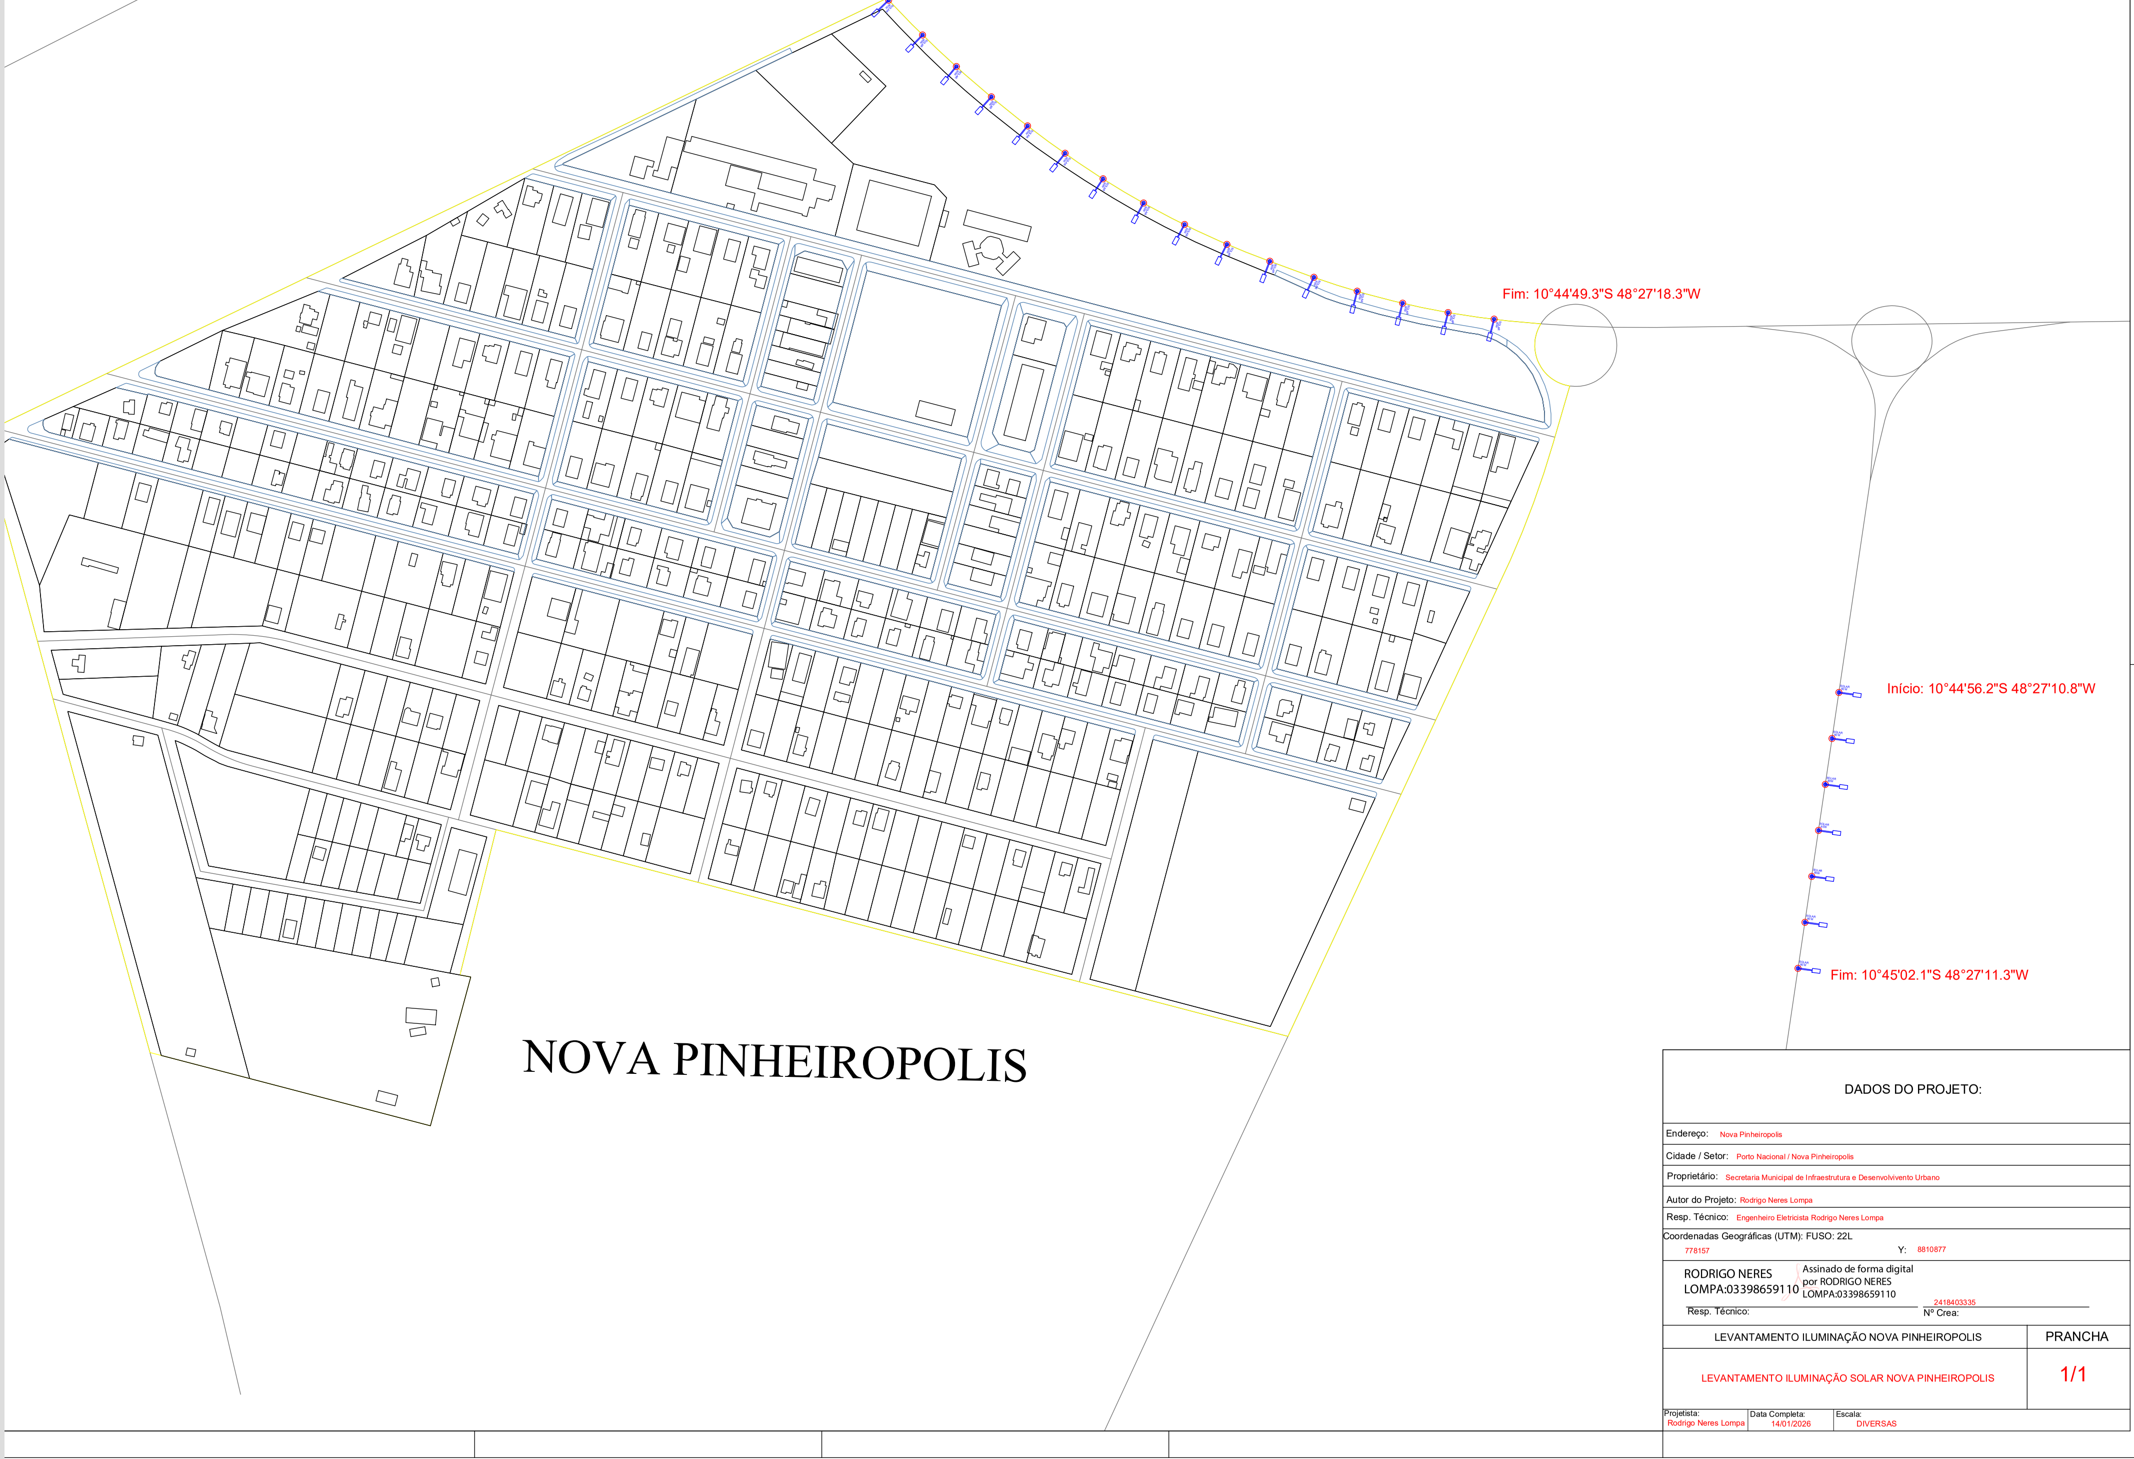
Início: 10°44'42.7"S 48°27'31.0"W
Fim: 10°44'49.3"S 48°27'18.3"W
Início: 10°44'56.2"S 48°27'10.8"W
Fim: 10°45'02.1"S 48°27'11.3"W
NOVA PINHEIROPOLIS

DADOS DO PROJETO:

Endereço: Nova Pinheiropolis

Cidade / Setor: Porto Nacional / Nova Pinheiropolis

Proprietário: Secretaria Municipal de Infraestrutura e Desenvolvivento Urbano

Autor do Projeto: Rodrigo Neres Lompa

Resp. Técnico: Engenheiro Eletricista Rodrigo Neres Lompa

Coordenadas Geográficas (UTM): FUSO: 22L
778157 Y: 8810877

RODRIGO NERES LOMPA:03398659110 Assinado de forma digital por RODRIGO NERES LOMPA:03398659110

Resp. Técnico:

Nº Crea: 2418403335

LEVANTAMENTO ILUMINAÇÃO NOVA PINHEIROPOLIS

PRANCHA

LEVANTAMENTO ILUMINAÇÃO SOLAR NOVA PINHEIROPOLIS

1/1

Projetista: Rodrigo Neres Lompa
Data Completa: 14/01/2026
Escala: DIVERSAS